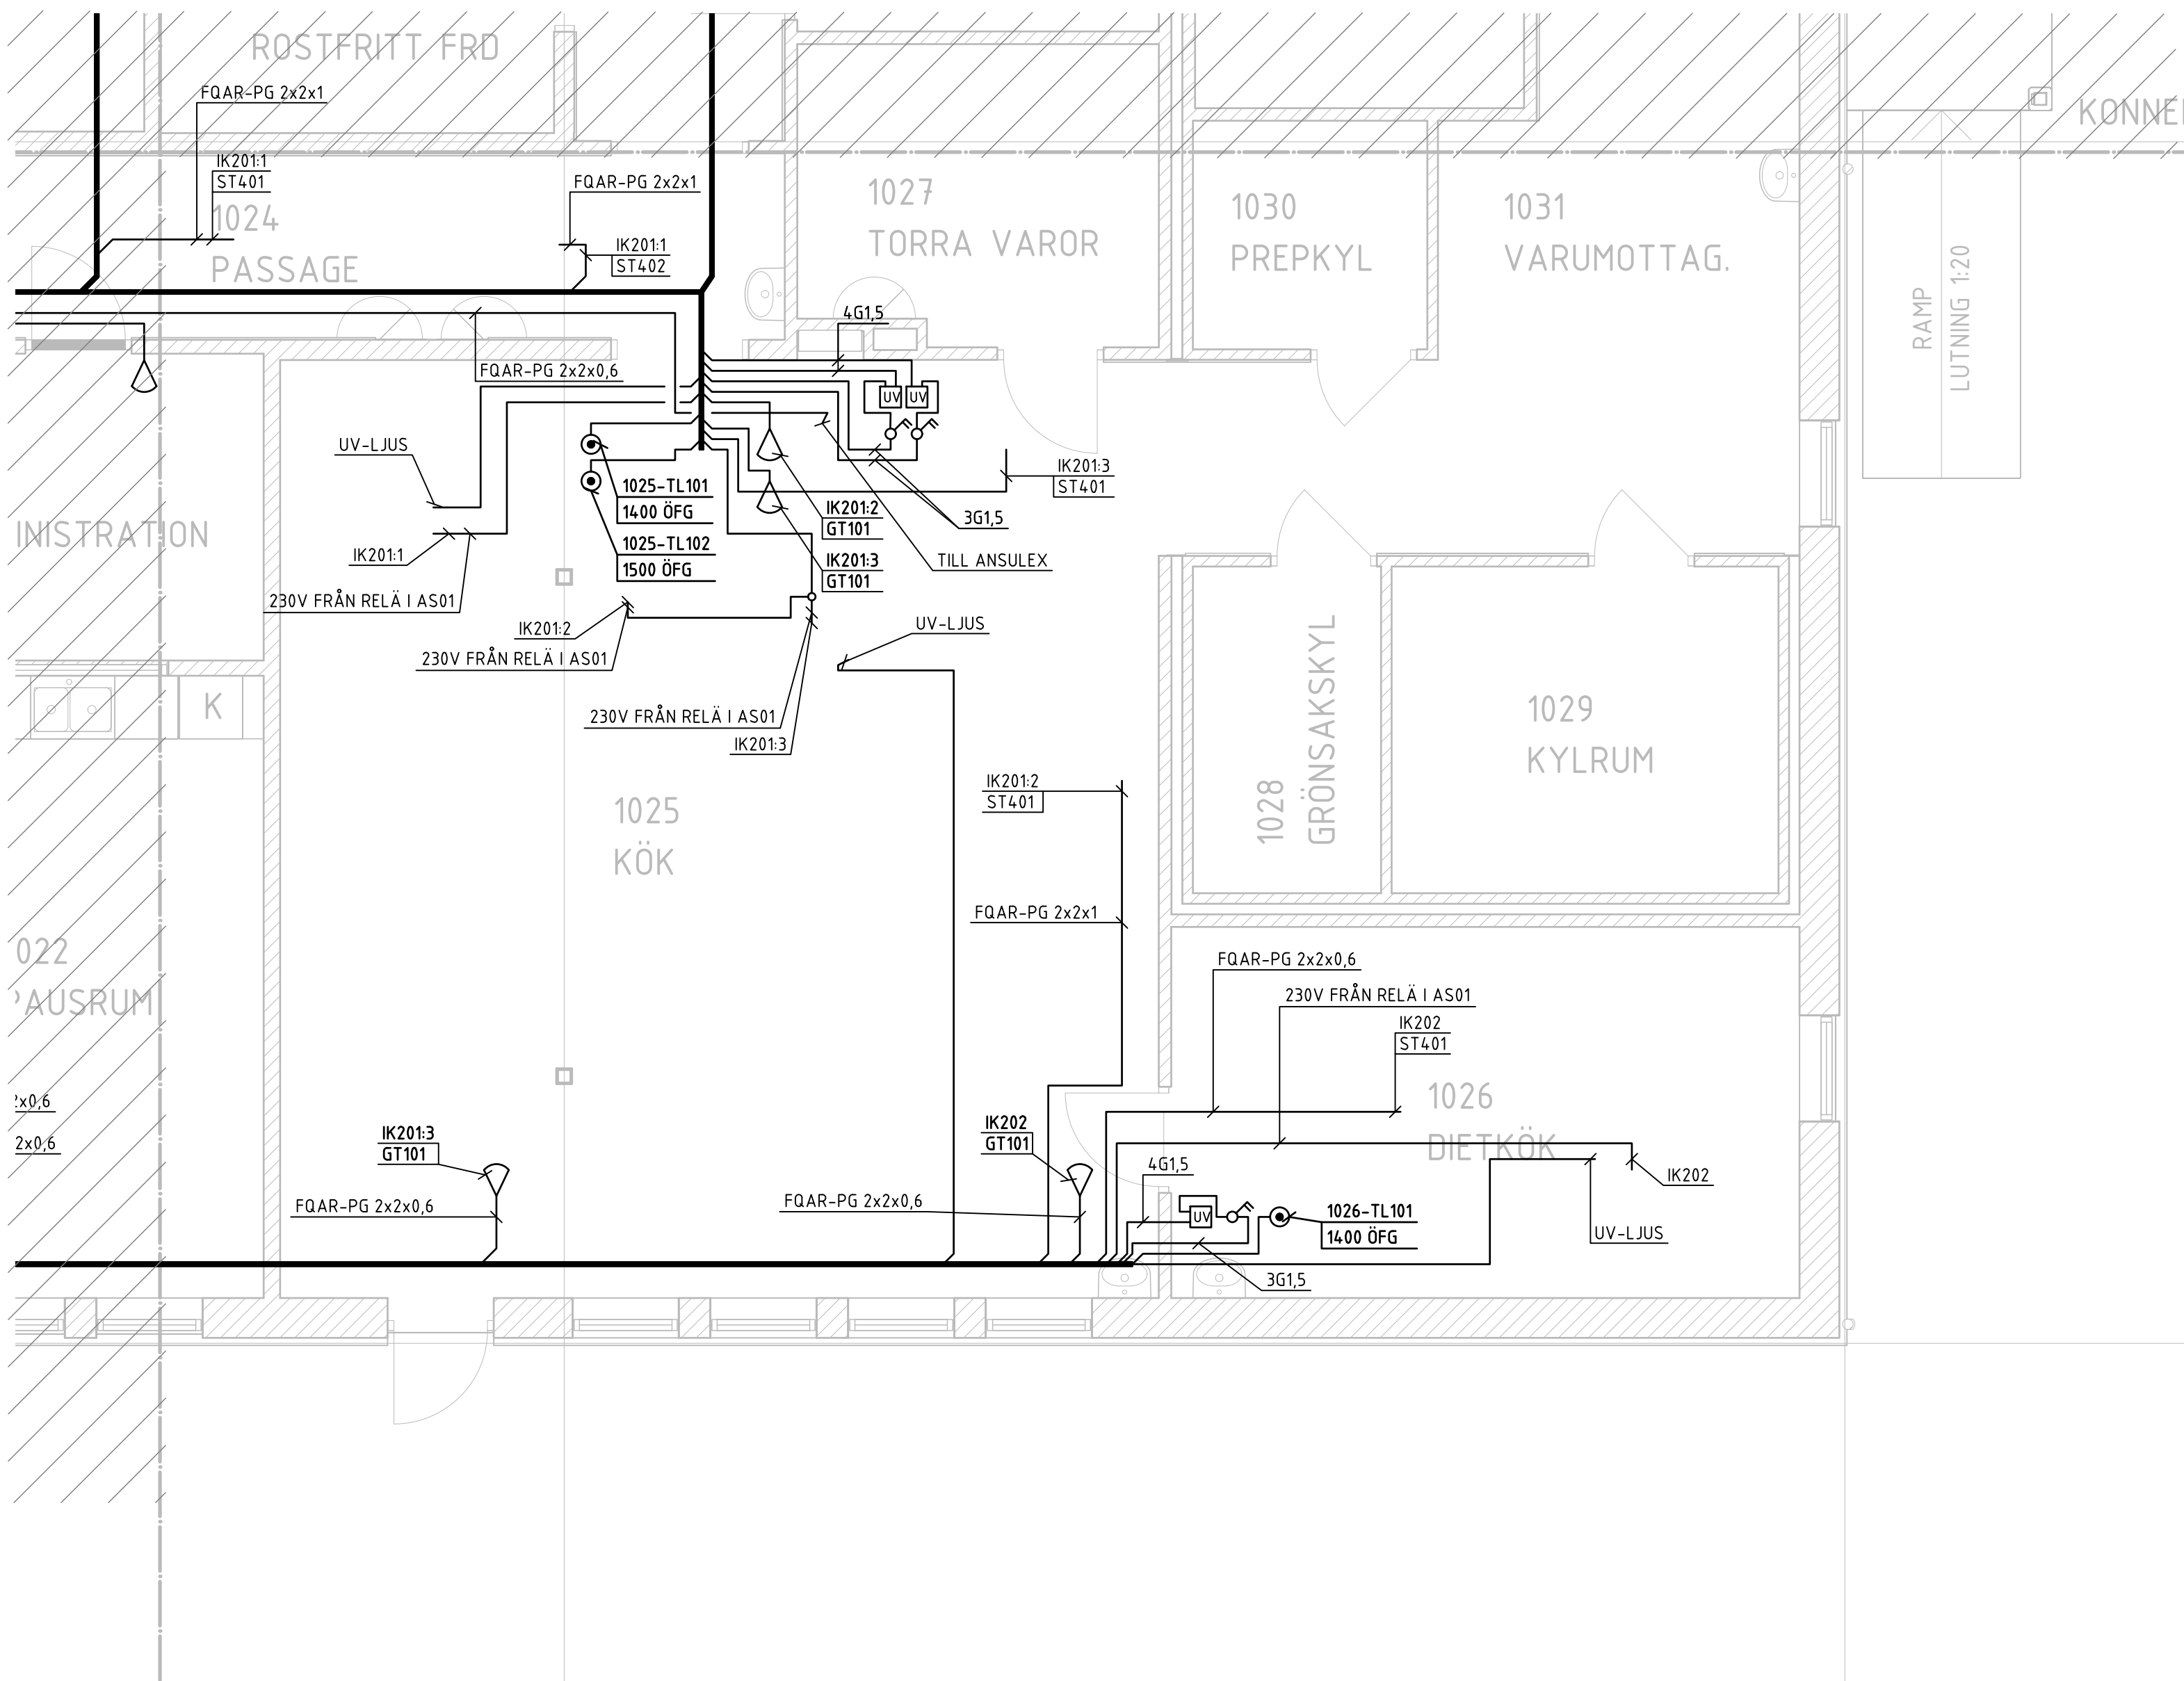
**ANVISNINGAR**

DÄR INGET ANNAT ANGES GÄLLER:
INFÄLLT MONTAGE PRIORITERAS DÄR BYGGNADES
KONSTRUKTIONEN TILLÅTER. VID UPL. MONTAGE FÖRLÄGGS
KABLAG I EL-LIST
BRANDTÄTNING I SAMMA KLASS SOM VÄGGENS
BRANDKLASS.
HÖJD ANGES METER ÖFG.
HALOGENFRITT MATERIAL
KABEL 3G1,5

SYMBOLFÖRKLARINGAR

- ⊗ BLIXTLJUS
- ▷ TEMPGIVARE GOLVVÄRME, HÖJD +1,5 ÖFG
- UV UV KONTROLLER
- ⚡ 2POLIG SÄKERHETSBRYTARE
- APPARATSKÅP

HÄNVISNINGAR

SE AVEN:
- STYR-UNDERLAG

SEKTION		
ORIENTERINGSFIGUR		
STATUS		
FÖRFRÅGNINGSUNDERLAG		
HANDLING		
BYGGHANDLING		
DATUM	2024-12-20	ANSÖKAN AV
DIREKTÖR	GIN	ÄNDRINGAR PM
BESTÄLLARE		
 ROBERTSFORS KOMMUN		
PROJEKTNAMN		
CENTRALKÖK		
KÖRARE		
ROBERTSFORS KOMMUN		
PROJEKTNUMMER	ADRESS	
YTTRE RINGVÄGEN 4		
DIREKTÖR	FÖRETAG	
FORDONET 1		
DISCIPLIN	FÖRETAG	
NORCONSULT SVERIGE AB		
UPPDRAGSNUMMER	SKAPAD AV	
1088371	GIN	
TELEFON	KONTAKTPERSON	
010 141 80 00	TOMAS BERGSTRÖM	
BYGGNADSVÄRDE	BYGGNADSVÄRDE	
+45,54 (FG)		
VÄNINGSPLAN	VÄNINGSDEL	DELOMRÅDE
1		DEL 5.4
SYSTEM		
EL I STYR		
SPECIFIKATION		
PLAN 1		
BYGGNADSVÄRDE	SKALA	FORMAT
PLANER	1:50	A1
DOCUMENTNUMMER	ÄNDRING	
E-81-1-514		