



ANVISNINGAR
DÄR INGET ANNAT ANGES GÄLLER:
KABELSKYDDSRÖR Ø50
HALOGENFRITT MATERIAL

SYMBOLFÖRKLARINGAR

--- KABELSKYDDSRÖR

HÄNVISNINGAR

- SE ÄVEN
- TEKNISK BESKRIVNING EL
- SITUATIONSPLAN KRAFT &
BELYSNING

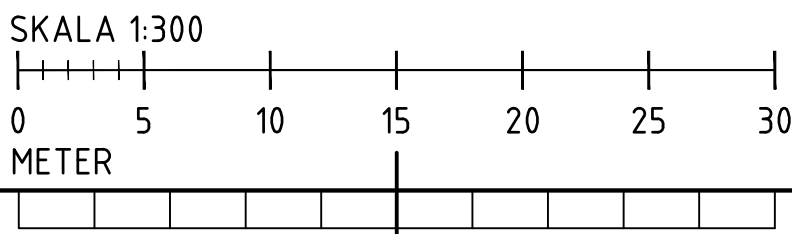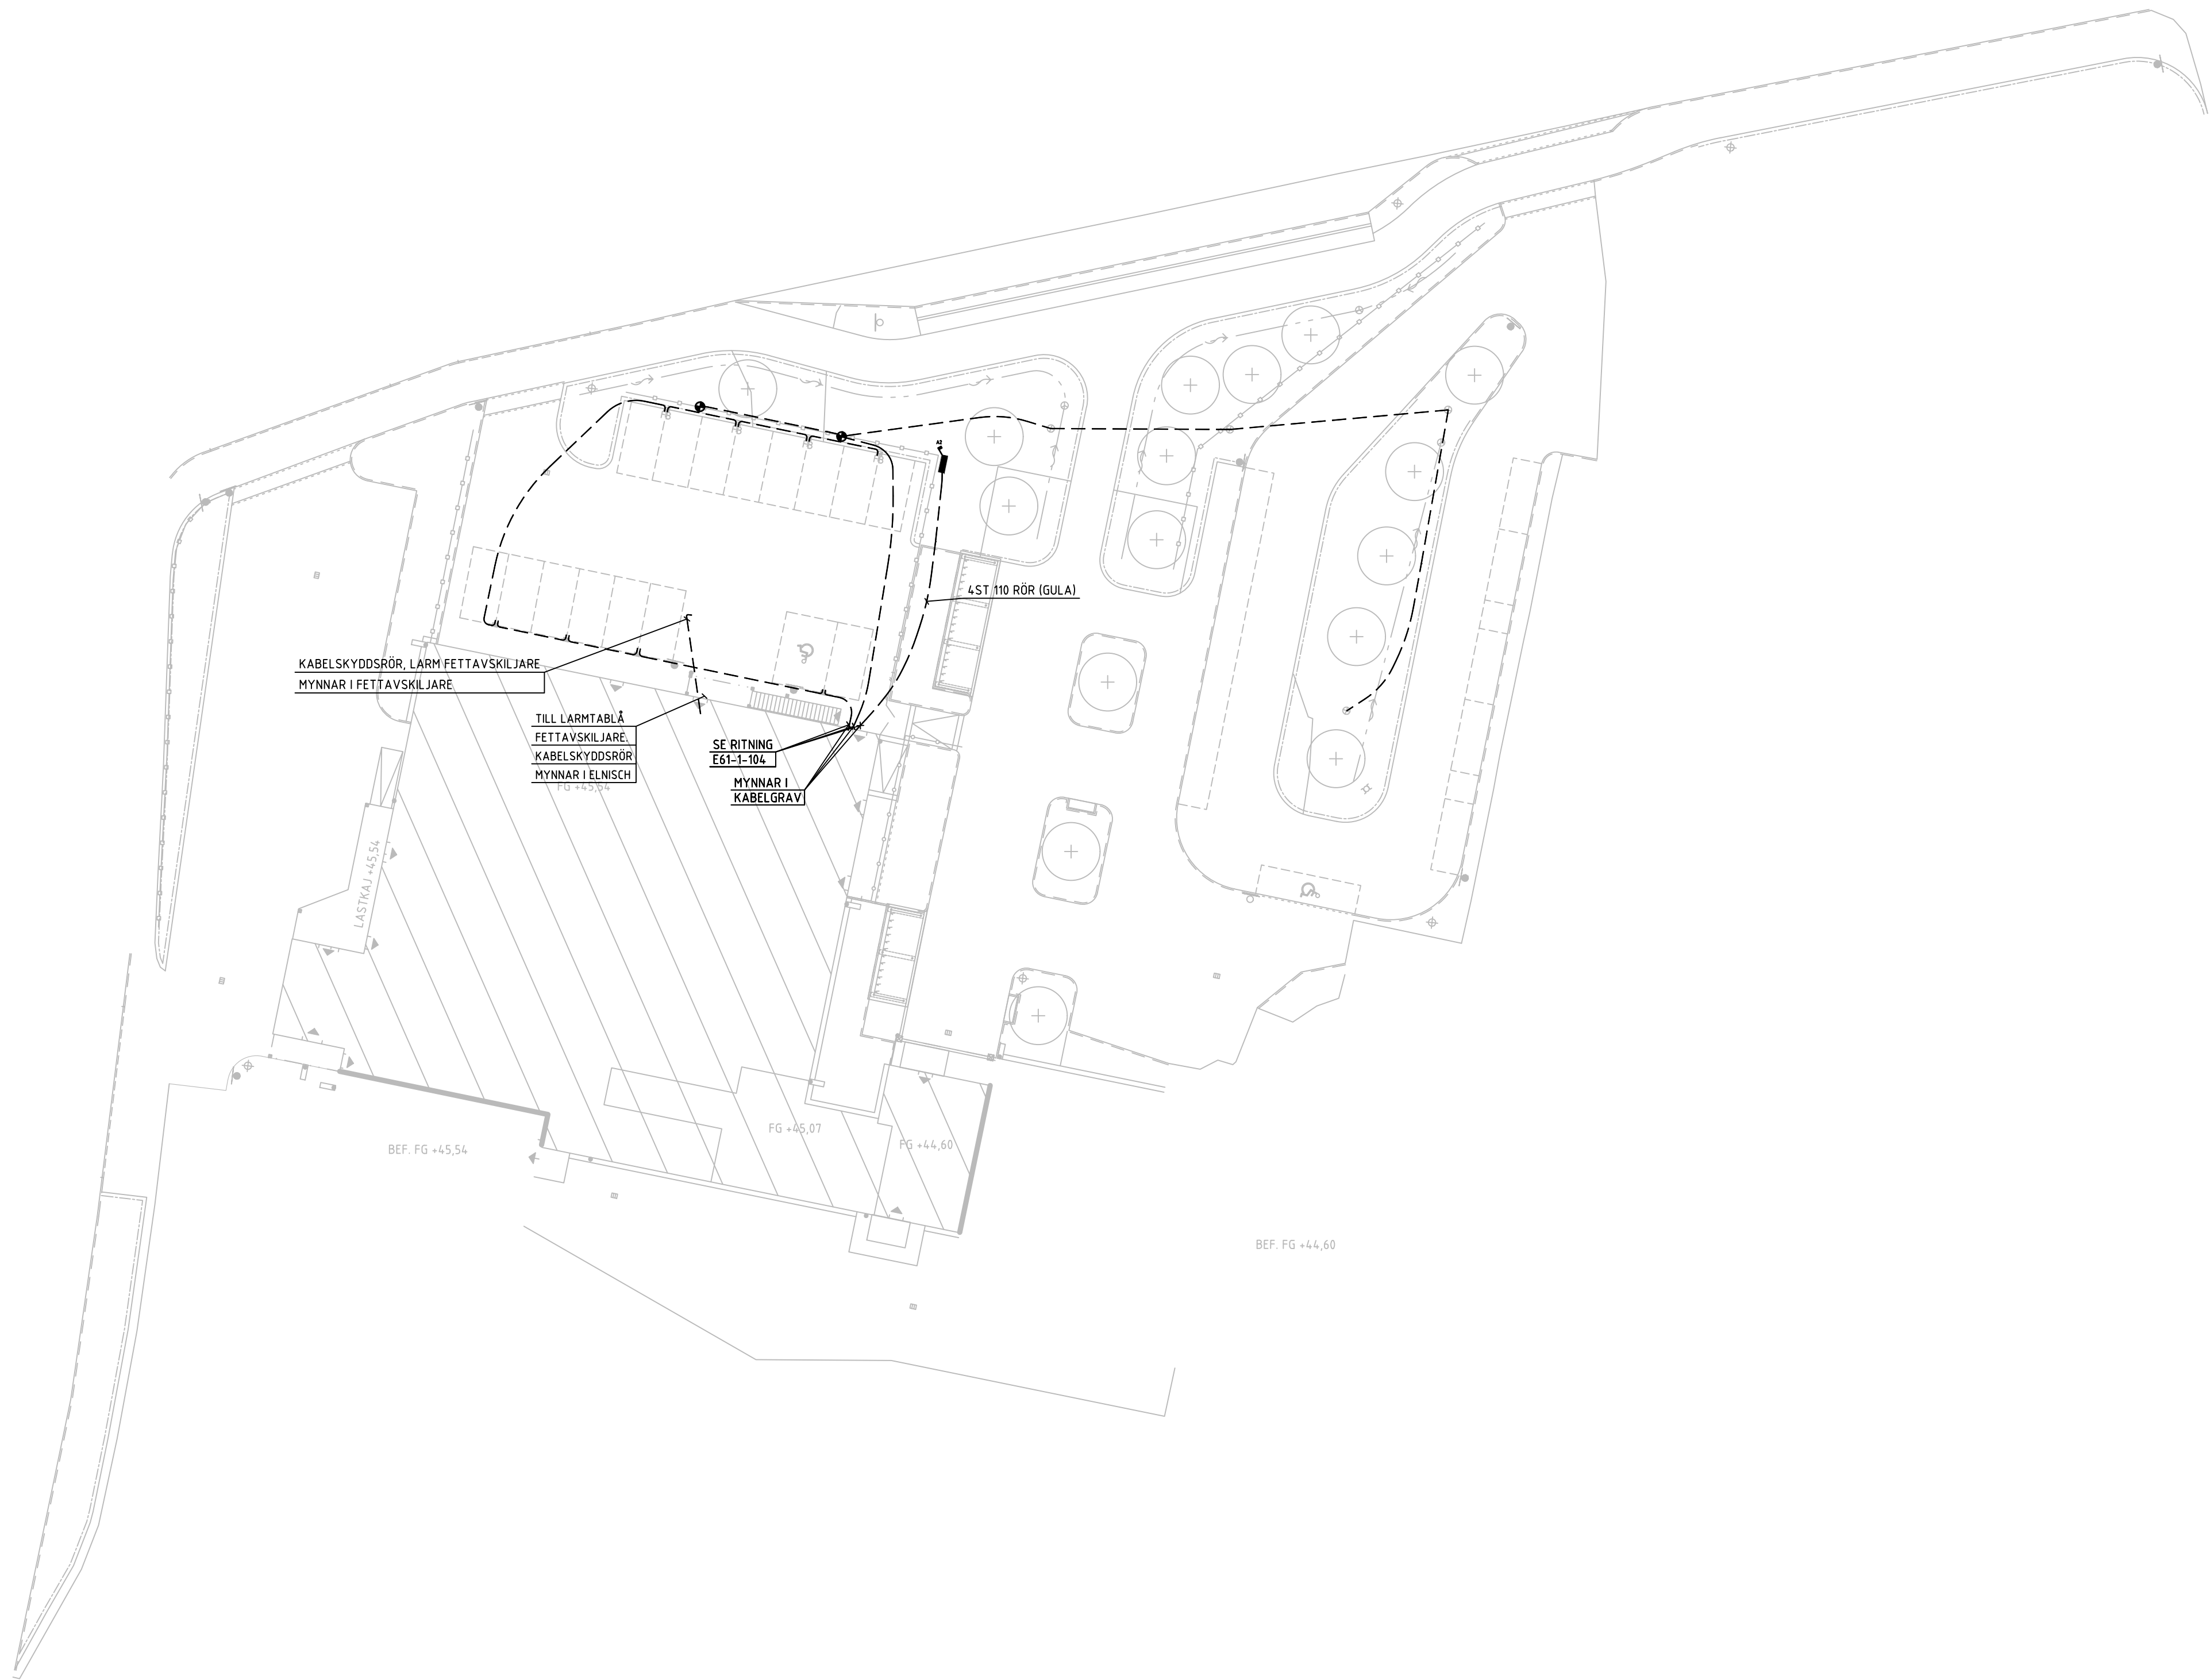

STATUS FÖRFRÅGNINGSUNDERLAG			
HANDLING BYGGHANDLING			
DATUM 2024-12-20	GÖRÖKAN AV GIN	ÄNDRINGS PM -	
BESTÄLLARE  ROBERTSFORS KOMMUN			
PROJEKTNAMN CENTRALKÖK			
OMRÅDE ROBERTSFORS KOMMUN			
PROJEKTNUMMER 108 83 71	ADRESS YTTRE RINGVÄGEN 4		
DÅRSKEDNUMMER	FASTIGHET FORDONET 1		
DISCIPLIN E	FÖRETAG NORCONSULT SVERIGE AB		
UPPDRAGSNUMMER 1088371	SKAPAD AV GIN		
TELEFON 010 141 80 00	KONTAKTPERSON TOMAS BERGSTRÖM		
BYGGNADSTYP BYGGNADSTYP	PÅLÖSNING (RIT 2000)		
VÄNINGSPLAN	VÄNINGSDEL	DELOMRÅDE	
SYSTEM KANALISATION			
SPECIFIKATION SITUATIONSPLAN			
TEKNIKGRUPP PLANER	SKALA 1:300	FORMAT A1	ÄNDRING
DOKUMENTNUMMER E61-1-001	-		