


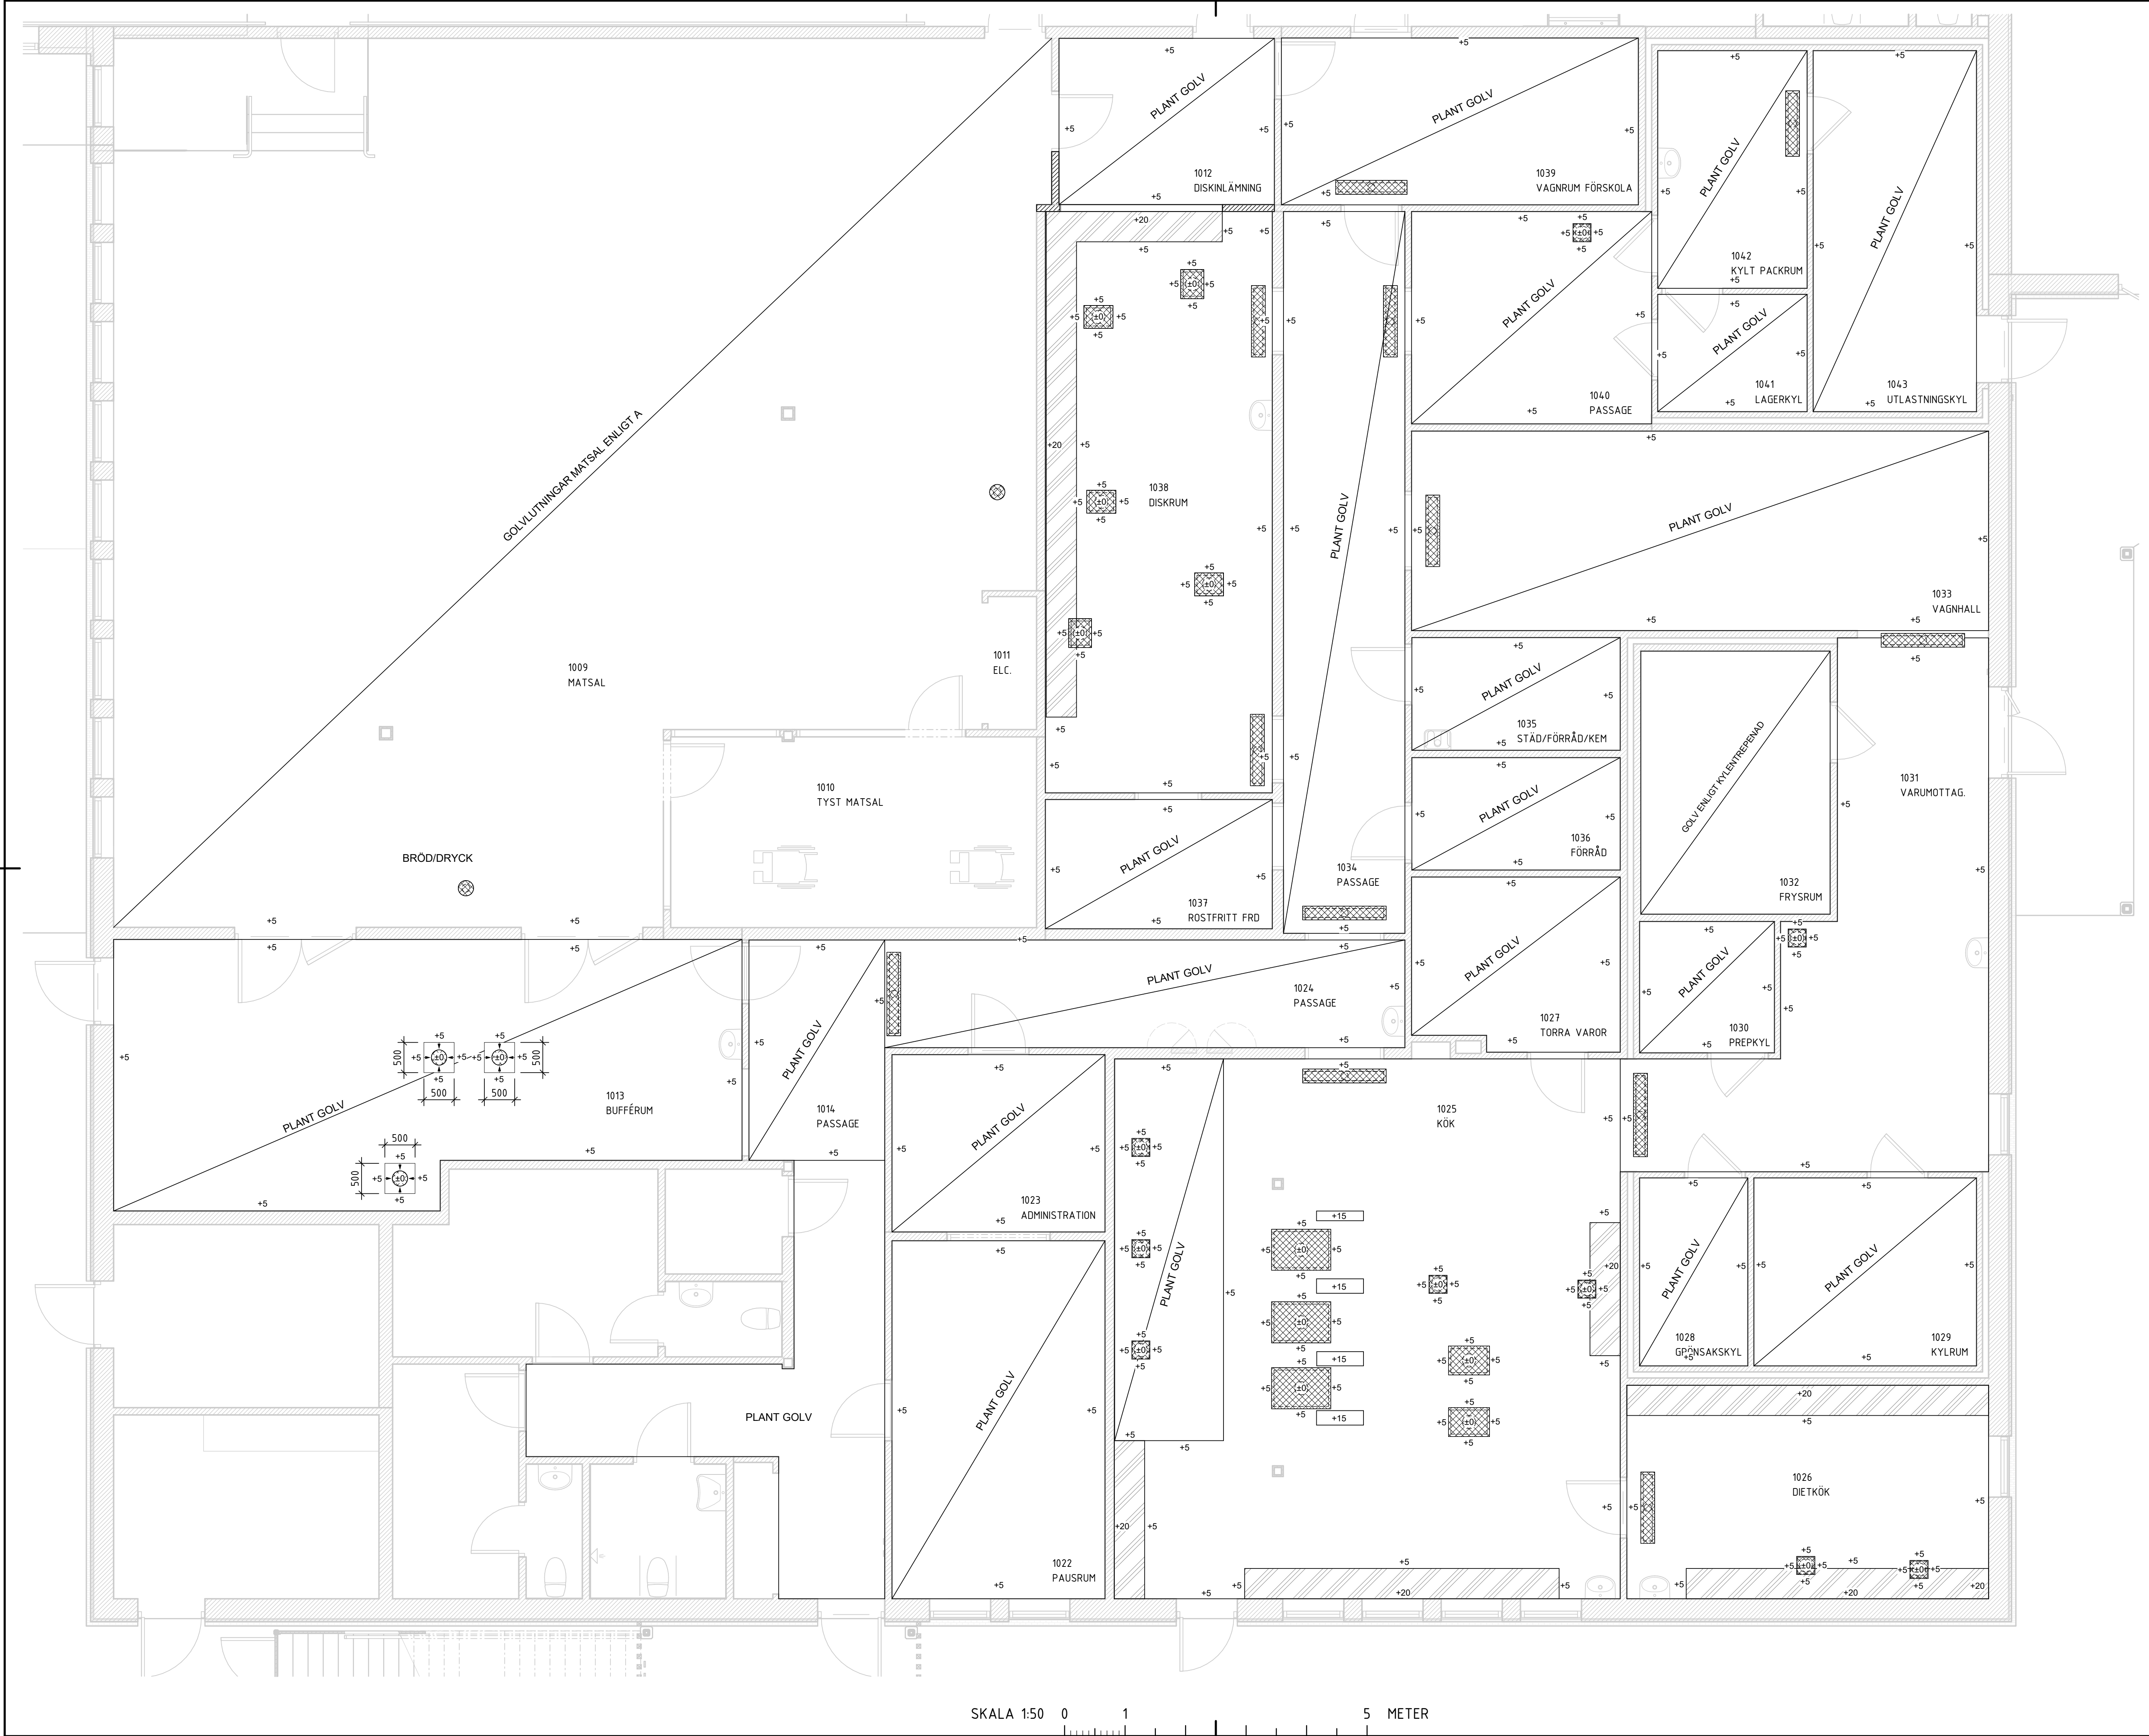


FÖRESKRIFTER

MARKERAD YTA REDOVISAR DÄR GOLVBELÄGGNING SKALL UTFÖRAS EXTRA BLANK FÖR FÖRBÄTTRAD VATTENAVRINNING.

OBS! SPÄRRBRUNNAR PLACERADE I ELLER NÄRA DÖRRÖPPNINGAR SAMT PASSAGER SKA UTFÖRAS UTAN NIVÅSKILLNAD MOT FÄRDIGT GOLV.

DVS. GOLVBRUNNENS GALLER SKALL INTE VARA FÖRHÖJD ELLER FÖRSANKT.

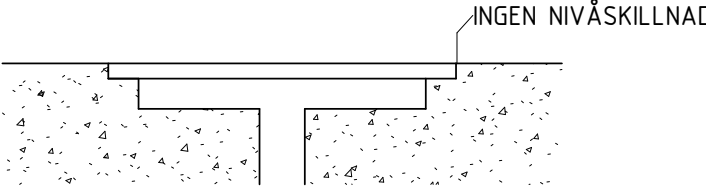

BERTON

OBIKTERINGSFIGUR

STATUS

HANDLING

DATUM

LOSRÄD

ANDRINGS

BESTÄLLARE

PROJEKTNAMN

OMRÅDE

PROJEKTNUMMER

ADRESS

QUARTALSNUMMER

FASTIGHET

DISCIPLIN

FÖRETAG

UPPGIFTSNUMMER

SKAPAD AV

108 83 71

ALG

TELEFON

KONTAKTPERSON

070-55 55 221

ANDREAS LAGERSKOG

STÖDSYSTEM

FLÖDESHÖJD

+ 45,54 (FG)

VÄNNINGSPLAN

1

VÄNNINGSDEL

5

SYSTEM

44 GOLVPLANER

SPECIFIKATION

UNDERLAG TILL GOLVPLAN, DEL 5

UTVÄRDERINGSKOD

PLAN

SKALA

1:50

FORMAT

A1

ANDRINGS

SK-44-1-150

DEL 7

DEL 2

DEL 3

DEL 4

DEL 6

DEL 5

DEL 1

ROBERTSFORS

KOMMUN

CENTRAKKÖK

ROBERTSFORS KOMMUN

YTTRE RINGVÄGEN 4

FORDONET 1

NORCONSULT SVERIGE AB

ANDREAS LAGERSKOG

+ 45,54 (FG)

44 GOLVPLANER

UNDERLAG TILL GOLVPLAN, DEL 5

PLAN

SKALA

1:50

FORMAT

A1

ANDRINGS

SK-44-1-150