




SKALA 1:50 0 1 5 METER

POSITIONSLISTA	
POS	Beteckning
1	Plats för varuskrinda
2	Rostfri arbetsbänk, höj- & sänkbar med el
3	Rostfri vägghylla 2-plan
4	Plats för bordvagn
5	Golvrengöringsanläggning
6	Redskaps-/borsthållare
7	Lytvagn
8	Balpress/sopkompressor
9	VAKANT
10	Gallerhyllställning
11	Hyllställning
12-14	VAKANT
15	Uppställningsplats för mobilt värmeskåp
16	VAKANT
17	Rostfri vägghylla 1-plan
18	Rostfri vägghylla 1-plan
19	VAKANT
20	Hyllställning
21	Hyllställning
22	Hyllställning
23-24	VAKANT
25	Golvrengöringsanläggning
26	Redskaps-/borsthållare
27	Redskaps-/borsthållare
28-29	VAKANT
30	Visp- och blandningsmaskin 60 L
31	Rostfri diskbänk med stor ho
32	Förspolningsdusch
33	Rostfri vägghylla 2-plan
34-35	VAKANT
36	Grönsaksskärmaskin, golvmödel
37	Redskapsvagn till grönsaksskärare
38	Kantinvagn till grönsaksskärare
39	VAKANT
40	Rostfri arbetsbänk, höj- & sänkbar med el
41	Rostfri arbetsbänk, höj- & sänkbar med el
42	Rostfri arbetsbänk, höj- & sänkbar med el
43	Rostfri överhylla på ståndare, 2-plan
44	VAKANT
45	Frys-skåp för C-kyla
46	Kylskåp för C-kyla
47	Kombiugn 15 x GN1/1
48	Plats för ugnsvagn
49	VAKANT
50	Uppställningsplats för mobilt värmeskåp
51	Mobilt rostfritt arbetsbord, höj- & sänkbart med vev
52-54	VAKANT
55	Induktionsspis 4 zoner
56	Rostfri diskbänk med utslagsvask
57	Rostfri överhylla på ståndare, 2-plan
58	Stekbord, höj- & sänkbart med eltopp
59	Stekbord, höj- & sänkbart med eltopp
60	Rostfri installationskanal
61-64	VAKANT
65	Kokgryta 200 L med omrörare
66	Kokgryta 200 L med omrörare
67	Kokgryta 100 L med omrörare
68	Redskapsvagn till kokgrytor
69-70	VAKANT
71	Kylskåp för C-kyla
72	Frys-skåp för C-kyla
73	Laminathögs-kåp på rostfria ben
74	Uppställningsplats för mobilt värmeskåp
75	Rostfri arbetsbänk, höj- & sänkbar med el
76	Rostfri vägghylla 2-plan
77	BEF Förslutningsmaskin bänkmodell
78-79	VAKANT
80	Stackad kombiugn 5+5 GN1/1
81	Plats för kantinvagn
82	Induktionsspis 4 zoner
83	Rostfri diskbänk med stor ho
84	Rostfri vägghylla 2-plan
85-89	VAKANT
90	Kantinvagn
91	Hyllställning
92-93	VAKANT
94	Inmatningsrullbana för grovdisk
95	Förspolningsdusch inkl blandare
96	Kombimaskin grov-/findisk med granuler
97	Utmatningsrullbana för grovdisk
98	VAKANT
99	Redskaps-/borsthållare
100	Rostfri tallriksbana
101	Diskinlämningsbänk 5 korgar med överhylla
102	Bassängrullbana med integrerat stänkskydd
103	Förspolningsdusch inkl blandare
104	Förspolningstunnel inkl matning
105	Tunneldiskmaskin
106	Utmatningsrullbana med ändlägesbrytare
107	Rostfri vägghylla 2-plan

POSITIONSLISTA	
POS	Beteckning
108	Plats för tallriksdispenser
109-110	VAKANT
111	Golvrengöringsanläggning
112	Redskaps-/borsthållare
113	Hyllställning
114	Snabbnedkylningsrum för C-kyla
115-117	VAKANT
118	Rostfri arbetsbänk, höj- & sänkbar med el
119	Rostfri överhylla på ståndare, 2-plan
120	BEF Förslutningsmaskin på rullbord
121	Rostfri arbetsbänk, höj- & sänkbar med el
122	Rostfri överhylla på ståndare, 2-plan
123	BEF Förslutningsmaskin på rullbord
124	Hyllställning
125	Hyllställning
126-129	VAKANT
129	Laminatskåp
130	Uppställningsplats för mobilt värmeskåp
131	Plats för avdelningsvagn
132	Rostfri arbetsbänk, höj- & sänkbar med el
133	Rostfri vägghylla 2-plan
134	Plats för korgvagn
135	Plats för tallriksdispenser
136	BEF Kylskåp med glasörr
137-139	VAKANT
140	Värmeskåp för genomräckning
141	Tallriksdispenser
142	Kylskåp med inbyggd kompressor
143	Rostfri toppskiva på laminatskåpsunderrede
144	Rostfri vägghylla 2-plan
145	Mikrovågsugn
146	Värmeri skolmodell, 2 x GN 1/1
147-149	VAKANT
150	Kall buffé, 3 x GN1/1
151	Varm buffé, 3 x GN1/1
152	Varm buffé, 2 x GN1/1
153	Neutral buffé
154	VAKANT
155	Rostfri toppskiva på laminatskåpsunderrede
156	Infäld vattensifon med spillbricka
157	Plats för kylid mjölkdispenser
158-159	VAKANT
160	Plats för korgvagn
161	Rostfri toppskiva på laminatskåpsunderrede
162	Infäld vattensifon med spillbricka
163	Plats för kylid mjölkdispenser
164	VAKANT
165	Rostfri avfallsstation, 2 stös

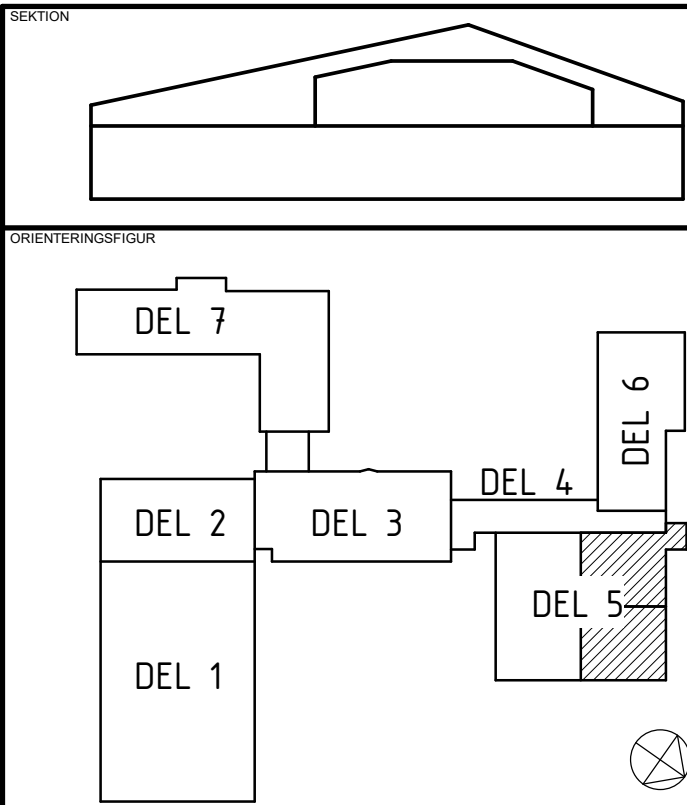

STATUS		
FÖRFRÅGNINGSUNDERLAG		
HANDLING		
BYGGHANDLING		
DATUM	FÖRBEREDARE	ÄNDRINGAR
2024-12-20	T. BERGSTRÖM	
BESTÄLLARE		
 ROBERTSFORS KOMMUN		
PROJEKTNAMN		
CENTRAKÖK		
ORÄDADE		
ROBERTSFORS KOMMUN		
PROJEKTNUMMER	YTTRE RINGVÄGEN 4	
DOKUMENTNUMMER	FORDONET 1	
ANSÖKAN	FÖRETAG	
SK	NORCONSULT SVERIGE AB	
UPPDRAGSNUMMER	BRADAP AV	
108 83 71	ALG	
TELEFON	KONTAKTPERSON	
070-55 55 221	ANDREAS LAGERSKOG	
STYCKPRIS	KONTAKTPERSON	
	+ 45 54 (FG)	
VÄRNINGSPÅN	VÄRNINGSDI	DELAVRÄD
1		5,2, 5,4
SYSTEM		
46 RUMSKOMPLETTERINGAR		
SPECIFIKATION		
PLAN 1, DEL 5.2, 5.4		
BYGGNADSTYP	SKALA	FORMAT
PLAN	1:50	A1
DOKUMENTNUMMER	ÄNDRING	
SK-46-1-152		