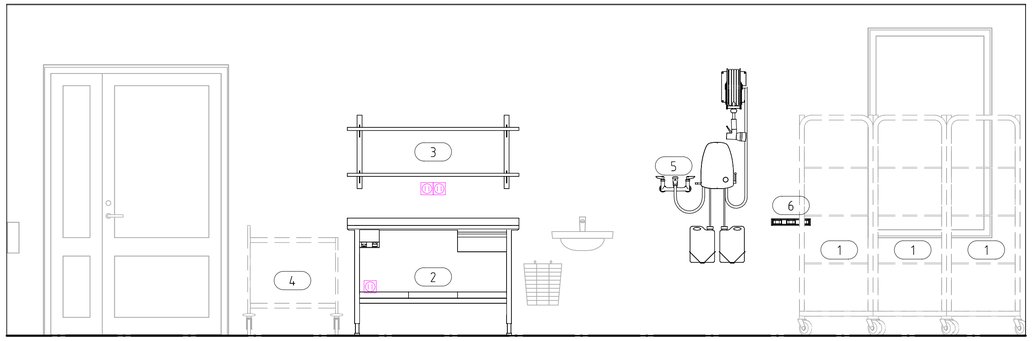

A

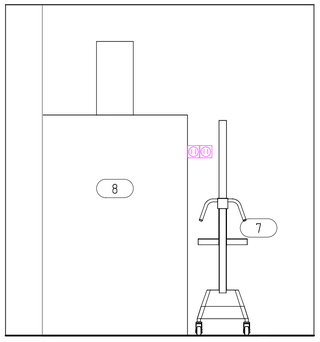

B

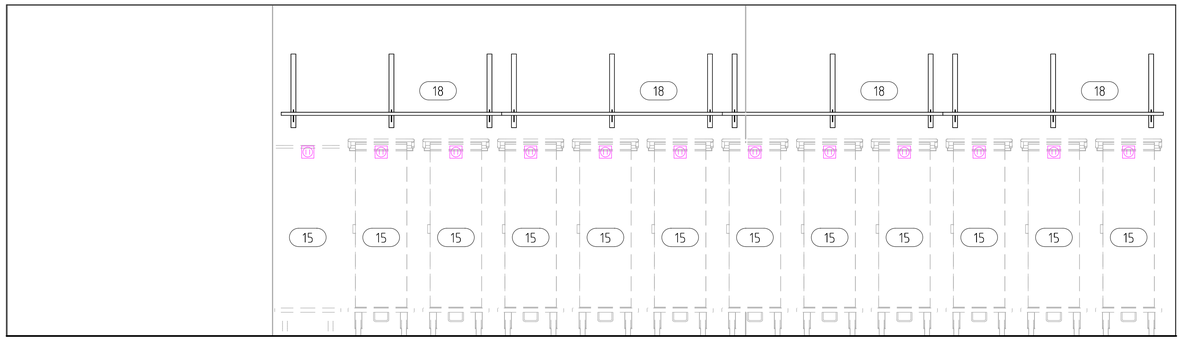

D

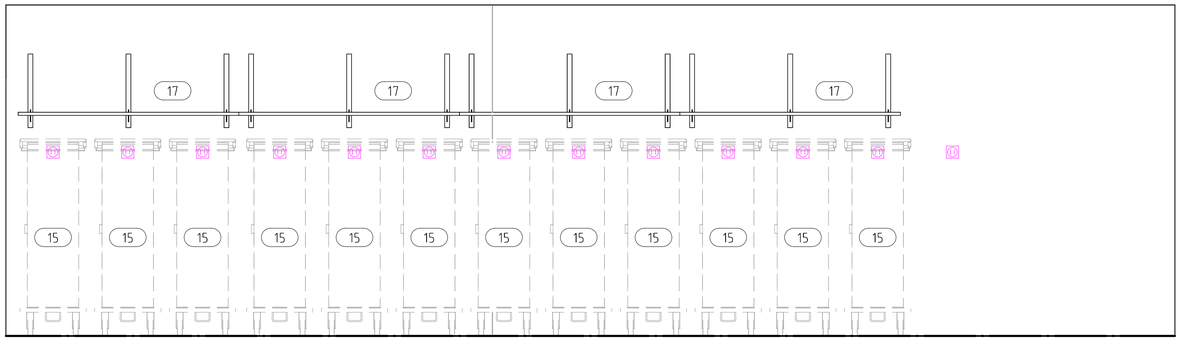

E

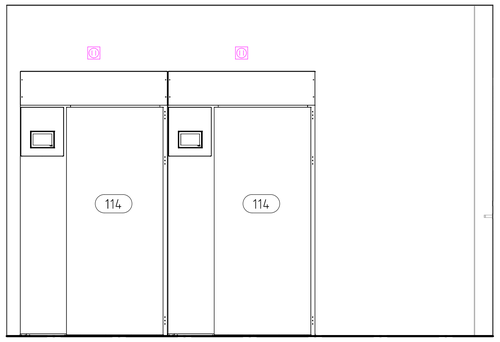

F

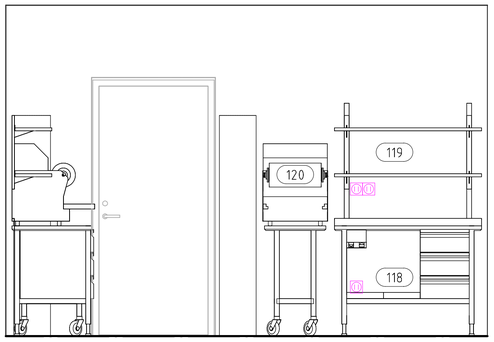

G

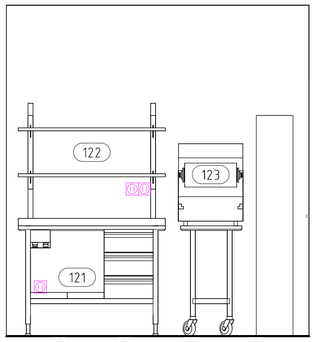

H

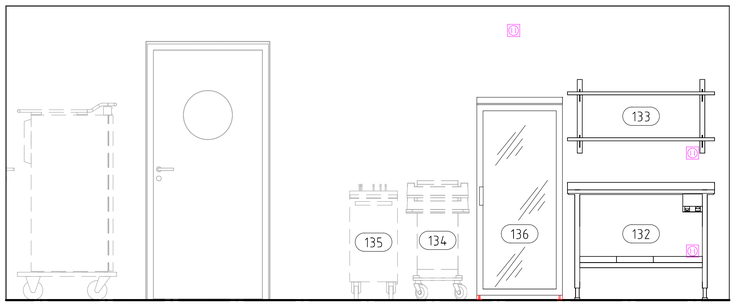

I

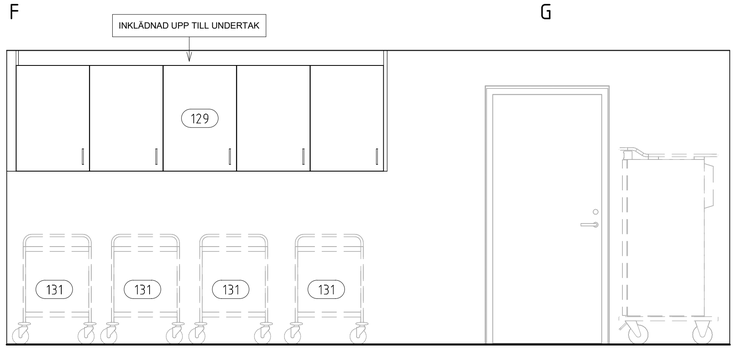

J

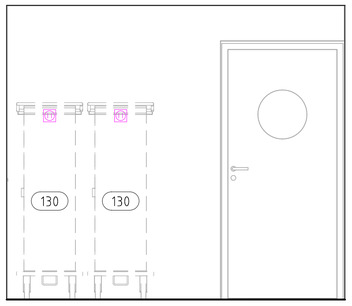

K

SEKTION

ORIENTERINGSFIGUR

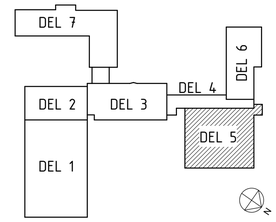

STATUS
FÖRFRÅGNINGSUNDERLAG

HANDLING
BYGGHANDLING

DATUM	GODKÄND AV	ÄNDRINGS PM
2024-12-20	T. BERGSTRÖM	

BESTÄLLARE
ROBERTSFORS KOMMUN

PROJEKTNAMN
CENTRALKÖK

OMRÅDE
ROBERTSFORS KOMMUN

PROJEKTNUMMER	ADRESS
	YTTRE RINGVÄGEN 4
DIARIENUMMER	FASTIGHET
	FORDONET 1
DISCIPLIN	FÖRETAG
SK	NORCONSULT SVERIGE AB
UPPDRAGSNUMMER	SKAPAD AV
108 83 71	ALG
TELEFON	KONTAKTPERSON
070-55 55 221	ANDREAS LAGERSKOG
BYGGNADSVERK	PLUSHÖJD (RH 2000)
VÅNINGSPLAN / VÅNINGSDEL	DELOMRÅDE
1	5

SYSTEM
46.4 UPPSTÄLLNINGAR

SPECIFIKATION
UPPSTÄLLNINGAR A-K

RITNINGSKATEGORI	SKALA	FORMAT
		A1

DOKUMENTNUMMER	ÄNDRING
SK-46-4-150	

SKALA 1:25 (A3 1:50)
0 0.5 1 2.5
METER

FILNAMN: C:\Users\AL Storkokskonsult\OneDrive - AL Storkokskonsult AB\AL Storkokskonsult AB\01 Projekt\Norconsult AB\1088371 - Centralkök Robertsfors\5 Arbetsmaterial\02 BIM\3D_Modell\(R24)1088371 - Centralkök Robertsfors(GH).rvt

2025-01-09 03:58:13