




PRINCIPDETALJ A-A

1 : 20

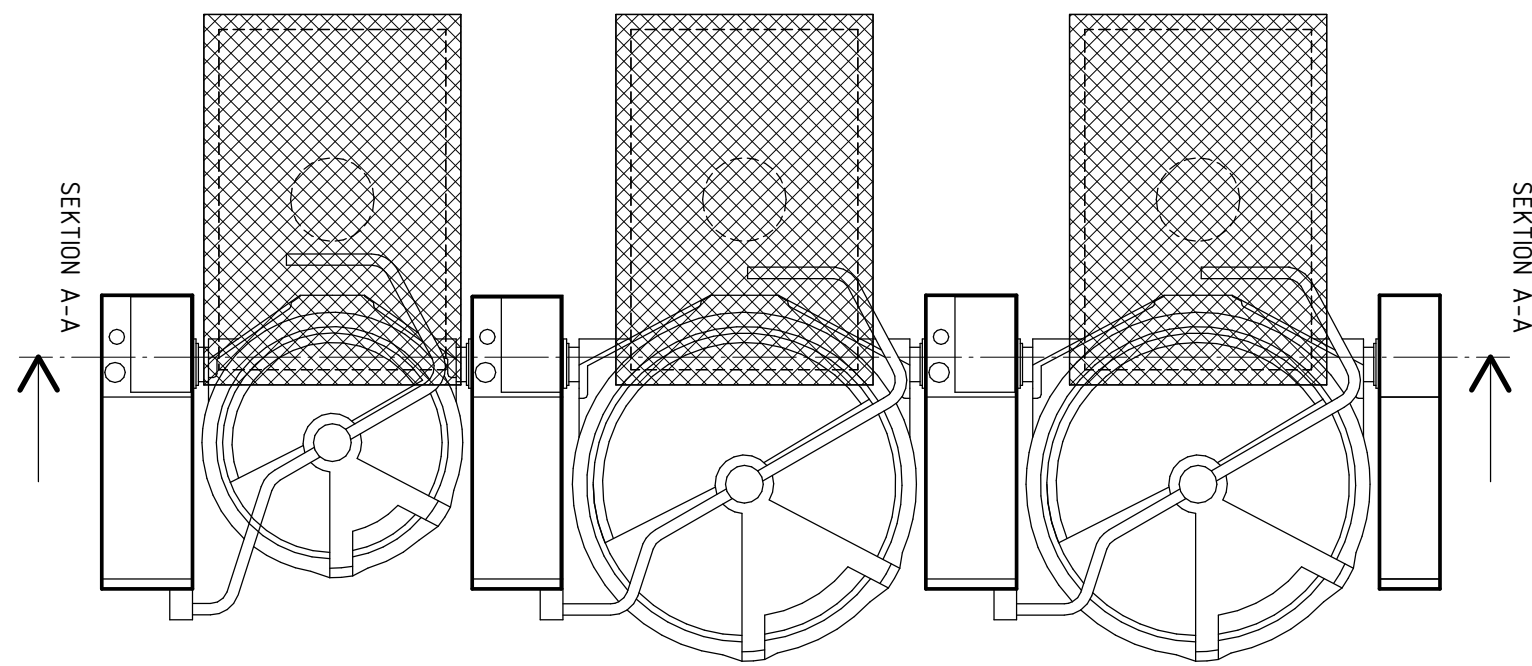

SEKTION A-A

1 : 20

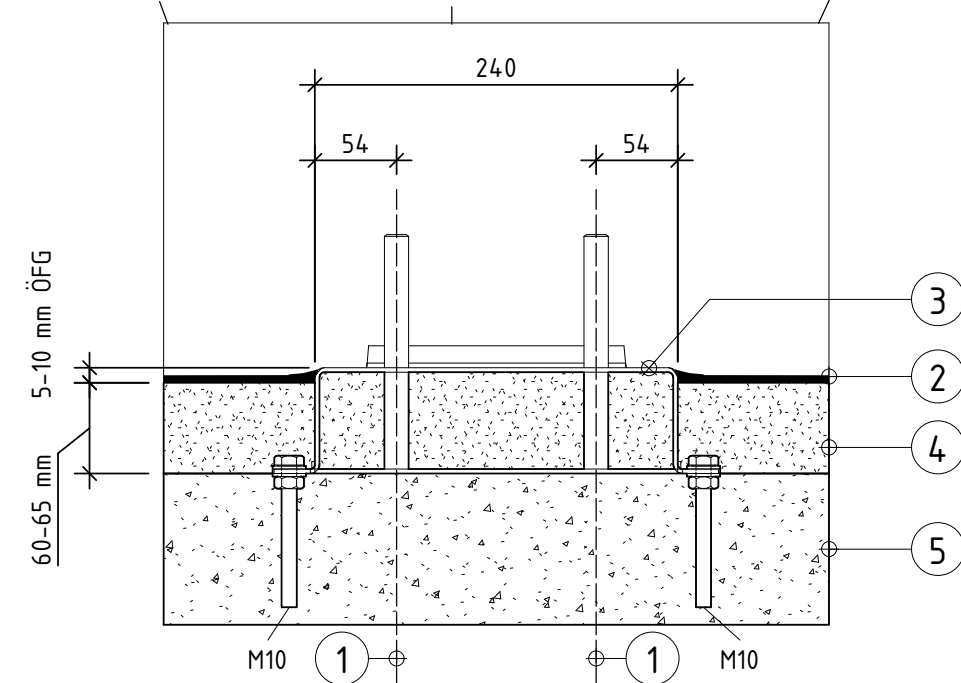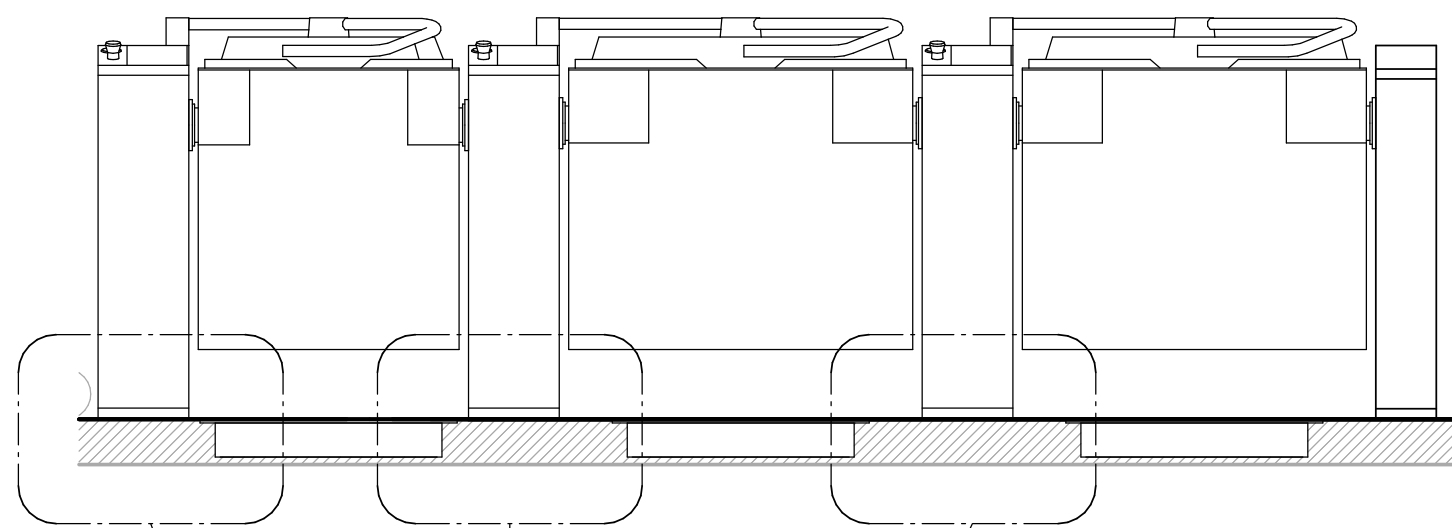


1. EL- OCH VS-ANSLUTNINGAR
2. PLASTMATTA MED UPPVIK
3. INGJUTNINGSRAM
4. BETONG/ÖVERBETONG
5. BETONG

DETALJ A-A

1 : 5



PRINCIPDETALJ B-B

1 : 20

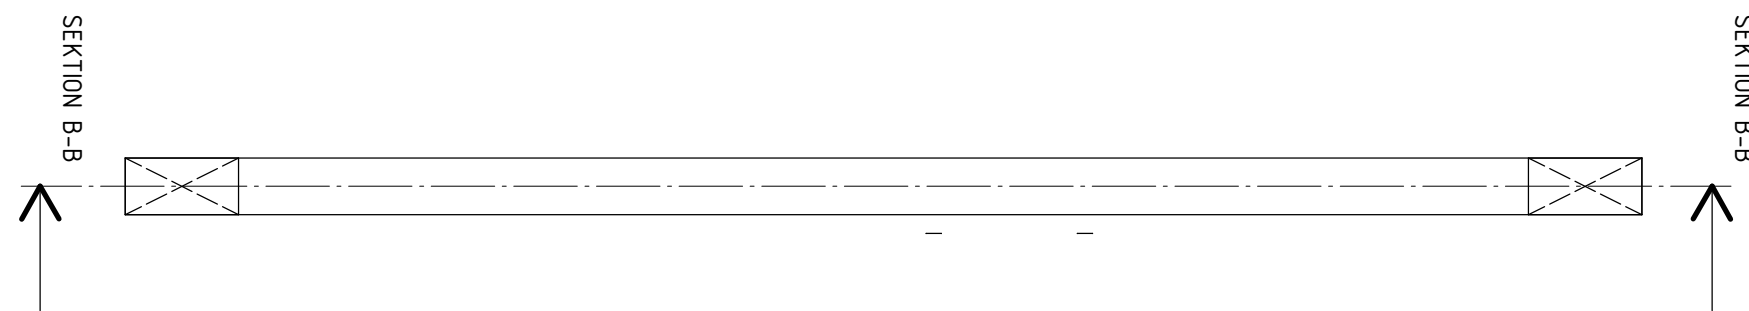

SEKTION B-B

1 : 20

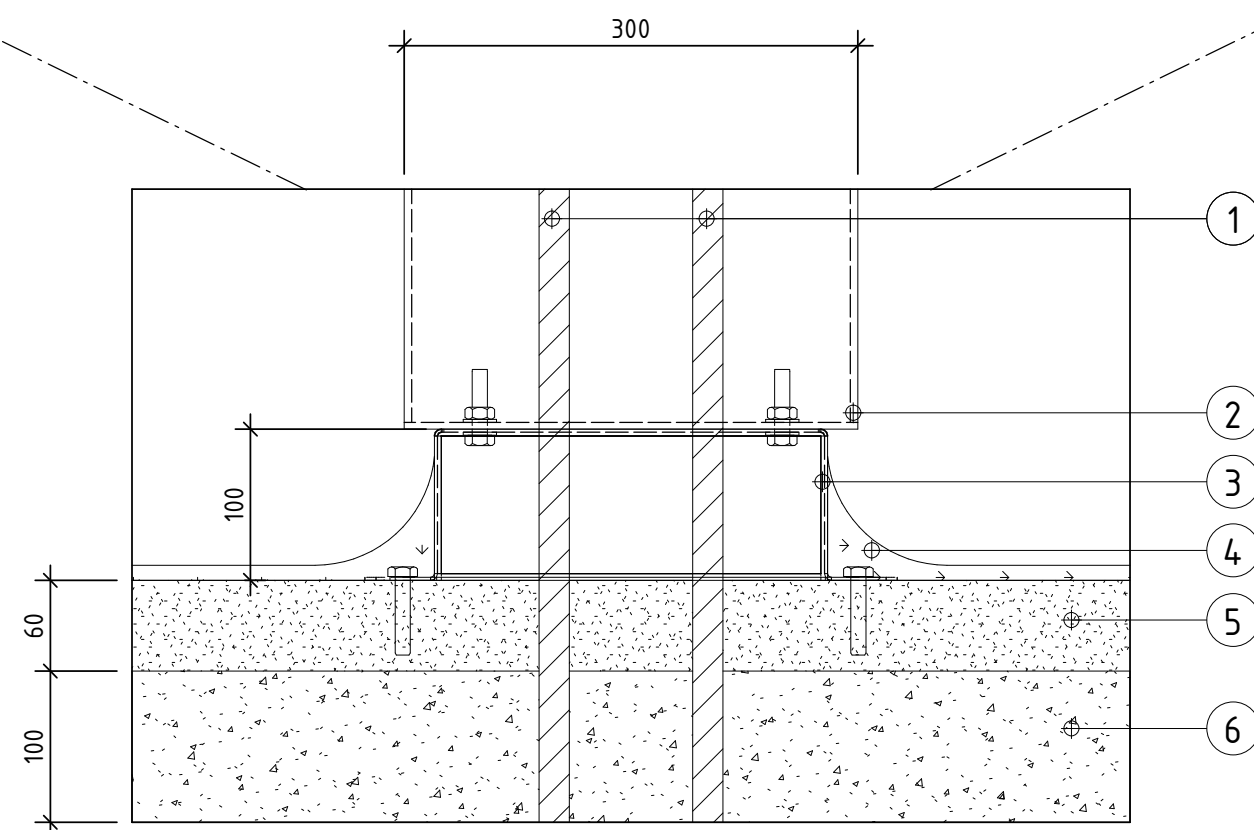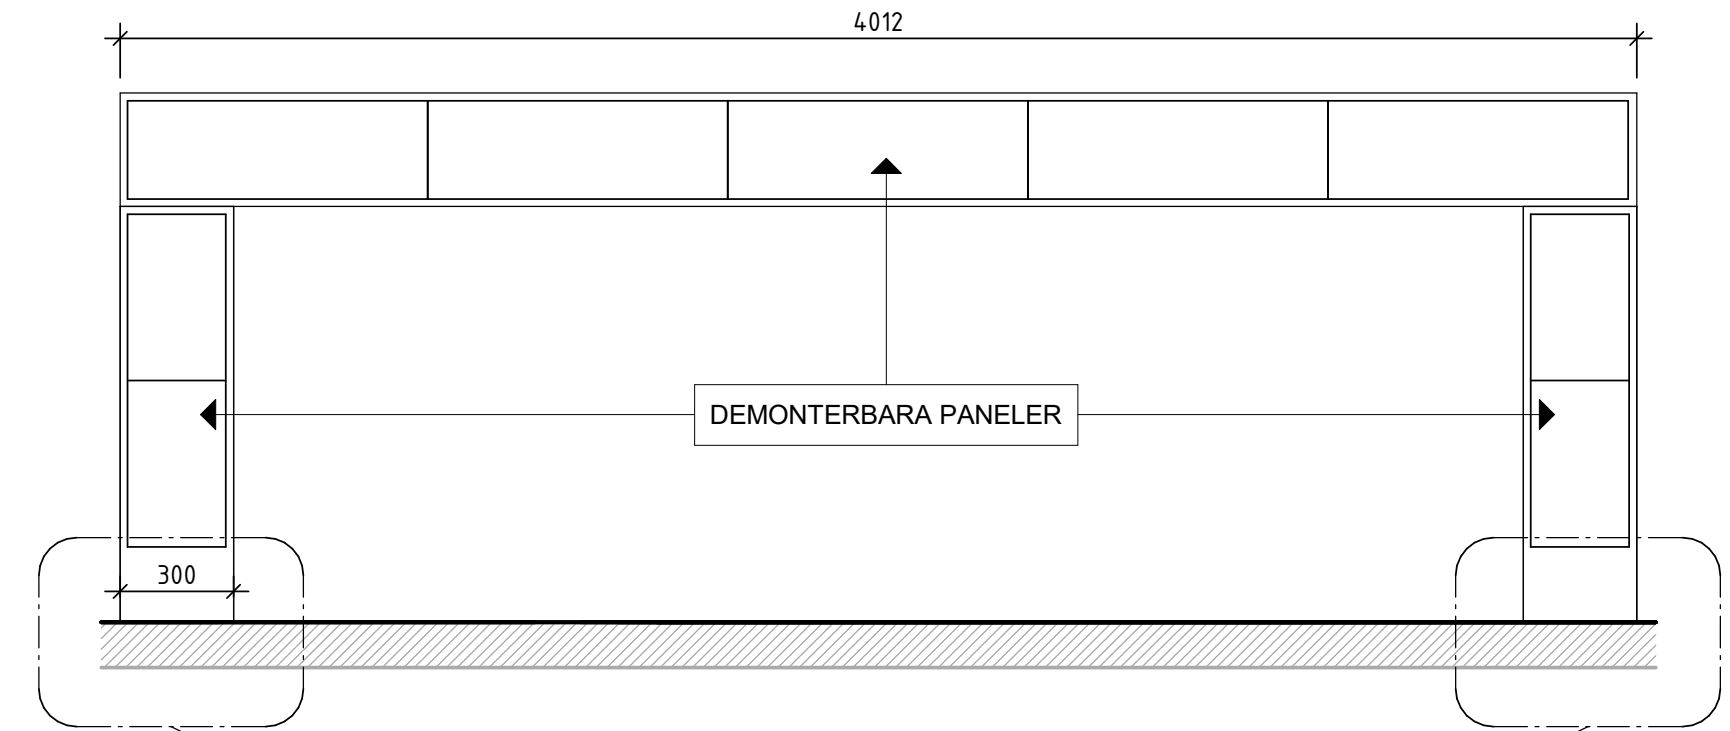

1. EL- OCH VS-ANSLUTNINGAR
2. ROSTFRI INSTALLATIONSKANAL
3. GOLVSTOS
4. ACRYLMASSA M. UPPVIK
5. BETONG/ÖVERBETONG
6. BETONG

DETALJ B-B



1 : 5

FÖRESKRIFTER

MARKERAD YTA REDOVISAR DÅR
GOLVBELÄGGNING SKALL UTFÖRAS EXTRA
BLANK FÖR FÖRBÄTTRAD
VATTENAVRINNING.

OBS! SPÄRRBRUNNAR PLACERADE I ELLER NÄRA
DÖRRÖPPNINGAR SAMT PASSAGER SKA UTFÖRAS
UTAN NIVÅSKILLNAD MOT FÄRDIGT GOLV.

DVS. GOLVBRUNNENS GALLER SKALL INTE VARA
FÖRHÖJD ELLER FÖRSÄNK.

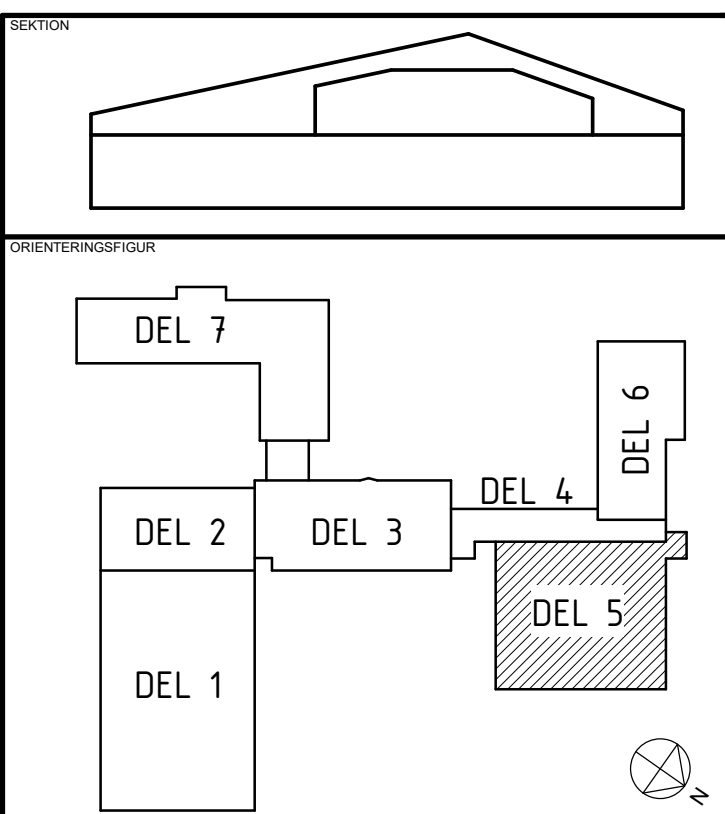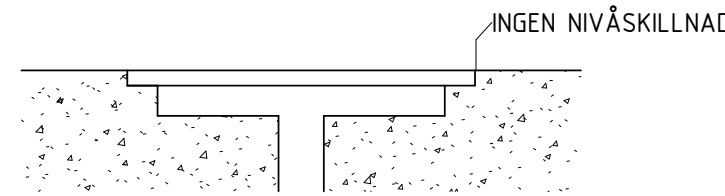

STATUS		
FÖRFRÅGNINGSUNDERLAG		
HANDLING		
BYGGHANDLING		
DATUM	LOSRÄDD AV	ÄNDRINGS PM
2024-12-20	T. BERGSTRÖM	
BESTÄLLARE		
 ROBERTSFORS KOMMUN		
PROJEKTNAMN		
CENTRALEKÖK		
OMRÅDE		
ROBERTSFORS KOMMUN		
PROJEKTNUMMER	ADRESS	
	YTTRE RINGVÄGEN 4	
DIARIENUMMER	FASTIGHET	
	FORDONET 1	
DISCIPLIN	FÖRETAG	
SK	NORCONSULT SVERIGE AB	
UPPDRAGSNUMMER	SKAPAD AV	
108 83 71	ALG	
TELEFON	KONTAKTPERSON	
070-55 55 221	ANDREAS LAGERSKOG	
BYGGKOSTPRIS	FÖLJESKED PRIS	
	+ 45,54 (FG)	
VÄRNINGSPÅN	VÄRNINGSDI	
1	5	
SYSTEM		
46.6 DETALJER		
SPECIFIKATION		
PRINCIPDETALJER 1		
RIKTNINGSKATEGORI	SKALA	FORMAT
		A1
DOCUMENTNUMMER	ÄNDRING	
SK-46-6-151		