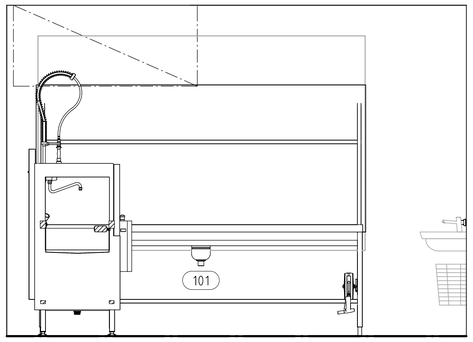
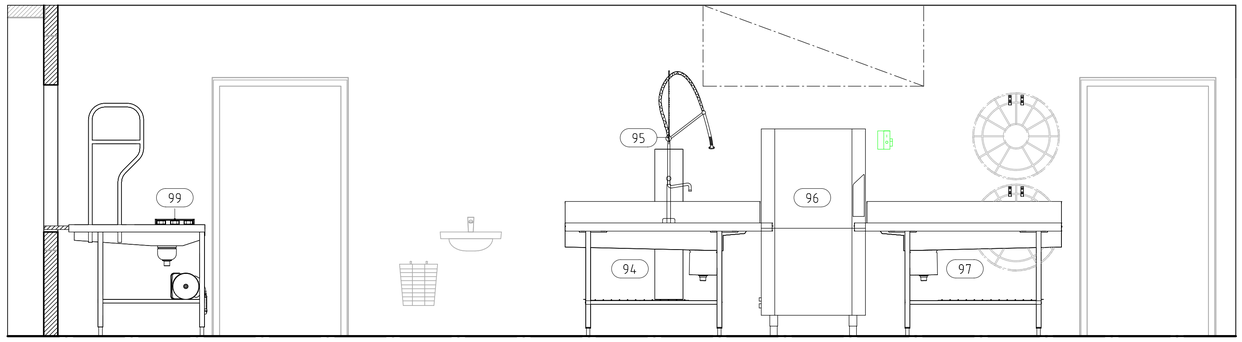
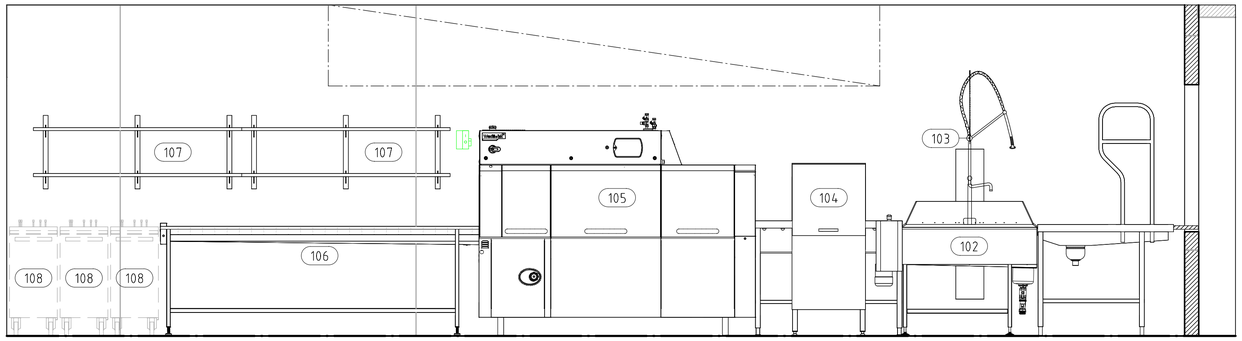


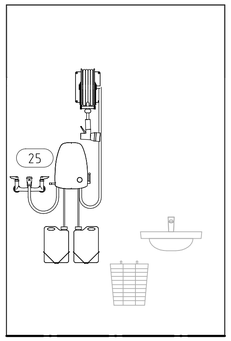

L



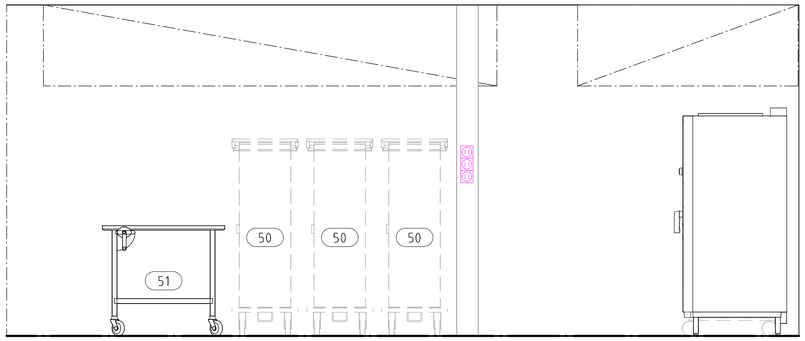

M



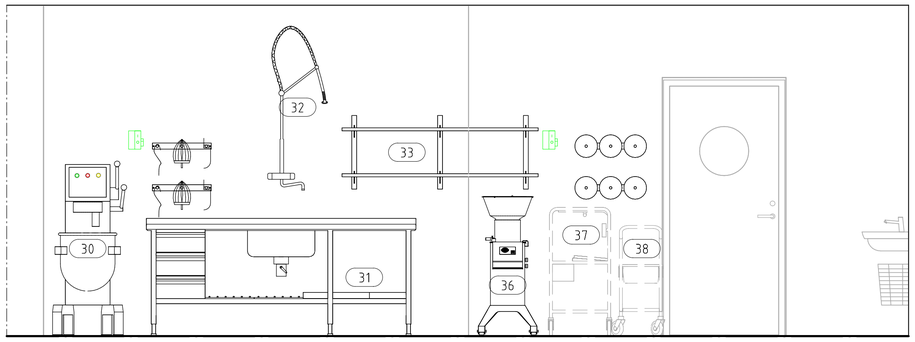

N



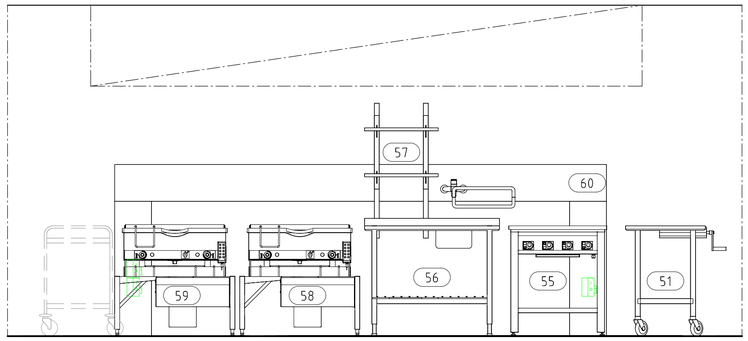

O



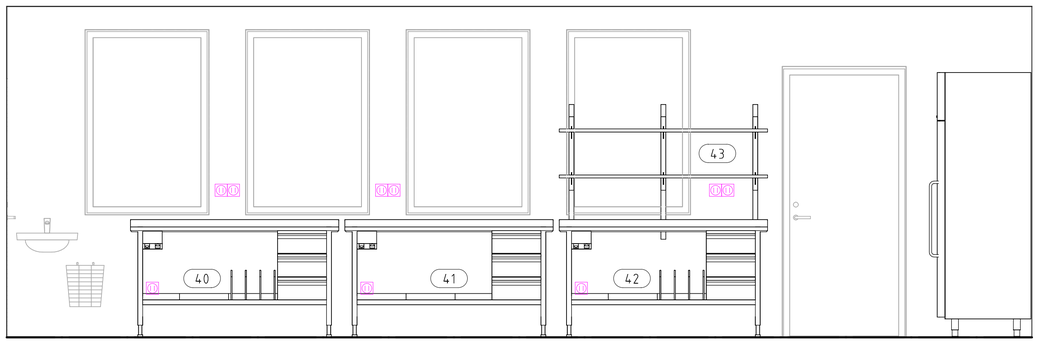

P




Q




R




S

SKALA 1:25 (A3 1:50)

0 0.5 1 2.5

METER

SEKTION



ORIENTERINGSFIGUR




STATUS
FÖRFRÅGNINGSUNDERLAG

HANDLING
BYGGHANDLING

DATUM 2024-12-20
GODKÄND AV T. BERGSTRÖM
ÄNDRINGS PM

BESTÄLLARE
ROBERTSFORS KOMMUN

PROJEKTNAMN
CENTRALKÖK

OMRÅDE
ROBERTSFORS KOMMUN

PROJEKTNUMMER
ADRESS YTTRE RINGVÄGEN 4

DIARIENUMMER
FASTIGHET FORDONET 1

DISCIPLIN SK
FÖRETAG NORCONSULT SVERIGE AB

UPPDRAGSNUMMER 108 83 71
SKAPAD AV ALG

TELEFON 070-55 55 221
KONTAKTPERSON ANDREAS LAGERSKOG

BYGGNADSVERK
PLUSHÖJD (RH 2000) + 45,54 (FG)

VÅNINGSPLAN 1
VÅNINGSDEL
DELOMRÅDE

SYSTEM 46.4 UPPSTÄLLNINGAR

SPECIFIKATION UPPSTÄLLNING L-S

RITNINGSKATEGORI
SKALA
FORMAT A1

DOKUMENTNUMMER SK-46-4-151
ÄNDRING

2025-01-09 03:29:51

FILNAMN: C:\Users\AL Storkokskonsult\OneDrive - AL Storkokskonsult AB\AL Storkokskonsult AB\01 Projekt\Norconsult AB\1088371 - Centralkök Robertsfors\5 Arbetsmaterial\02 BIM\3D_Modell\(R24)1088371 - Centralkök Robertsfors(GH).rvt