

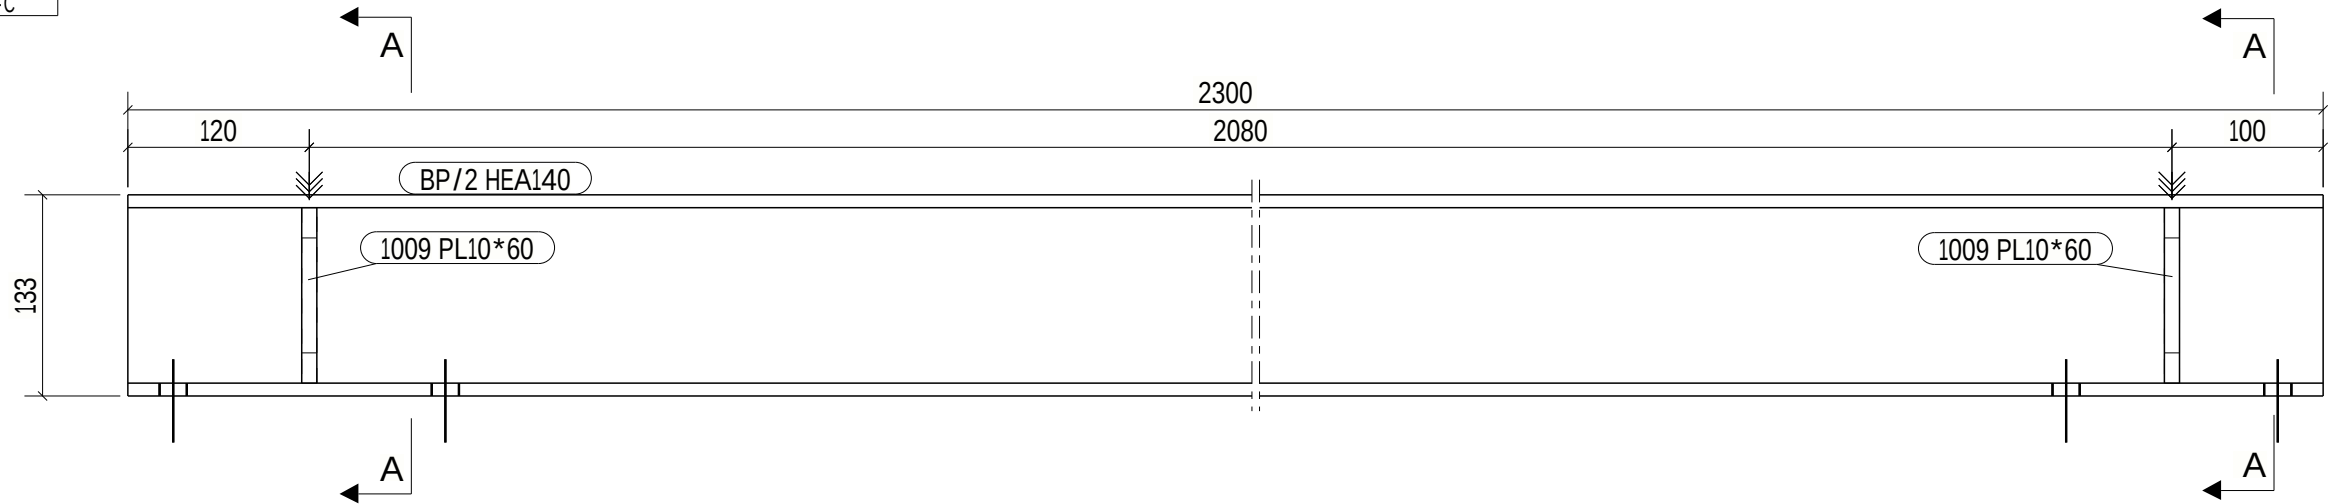


PLACERING I STOMNÄT	
NUMMER	SYSTEMLINJE
B/1	6-7/B
B/1	6-7/B-C

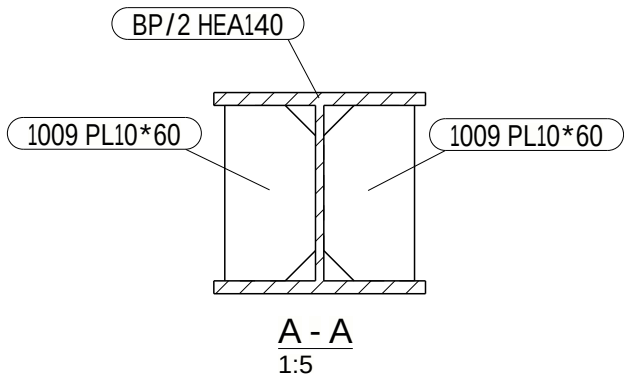

UTVÄNDIGT STÅL VARMFÖRZINKAS ENLIGT ALLMÄNNA FÖRESKRIFTER K-01-0-001 -- 003

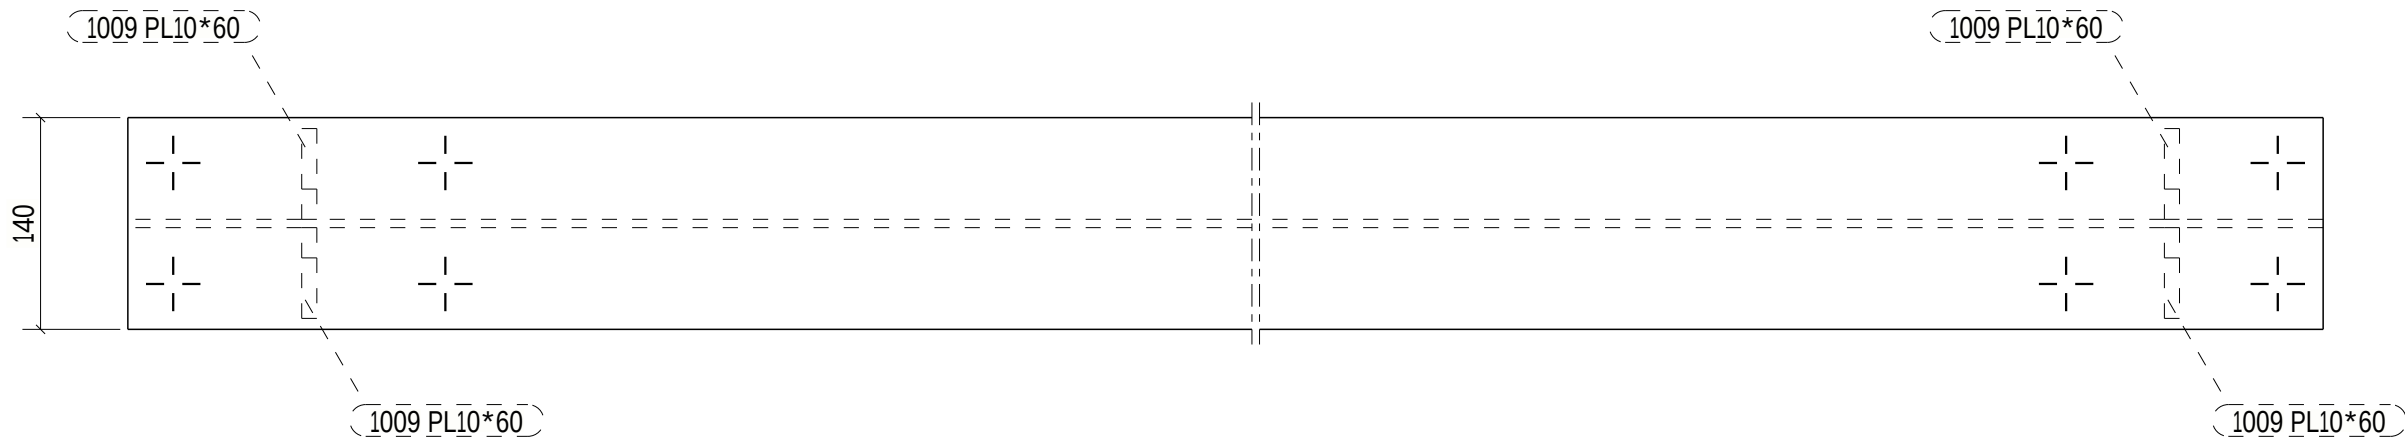

ALLMÄNNA NOTERINGAR: ALLA SVETSAR ÄR KÄLSVETS a5 OM EJ ANNAT ANGES

MATERIALLISTA FÖR ETT GODS MÄRKT: B/1 2 st. TILLVERKAS						
STYCKLIT.	PROFIL	MATERIAL	ANT.	LÄNGD	AREA/st	VIKT/st
BP/2	HEA140	S355J2	1	2300	1.8	56.7
1009	PL10*60	S355J2	4	116	0.0	0.5
TOTALT					1.9	58.8

Norconsult	ANSVARIG PART	PROJEKT	FÖRFRÅGNINGSUNDERLAG		STATUS
	KONTAKTPERSON	CENTRALEKÖB ROBERTSFORS KOMMUN	BYGGHANDLING		HANDLING
	GODKÄND AV	TILLVERKNINGSRITNINGAR STÅL	ÄNDRING		FORMAT
	SKAPAD AV	INNEHÅLL	2024-12-20	DATUM	A3
PARTS			NUMMER	1:5	SKALA
			B/1	BET	