


PLACERING I STOMNÄT	
NUMMER	SYSTEMLINJE
B/10	3/A-B

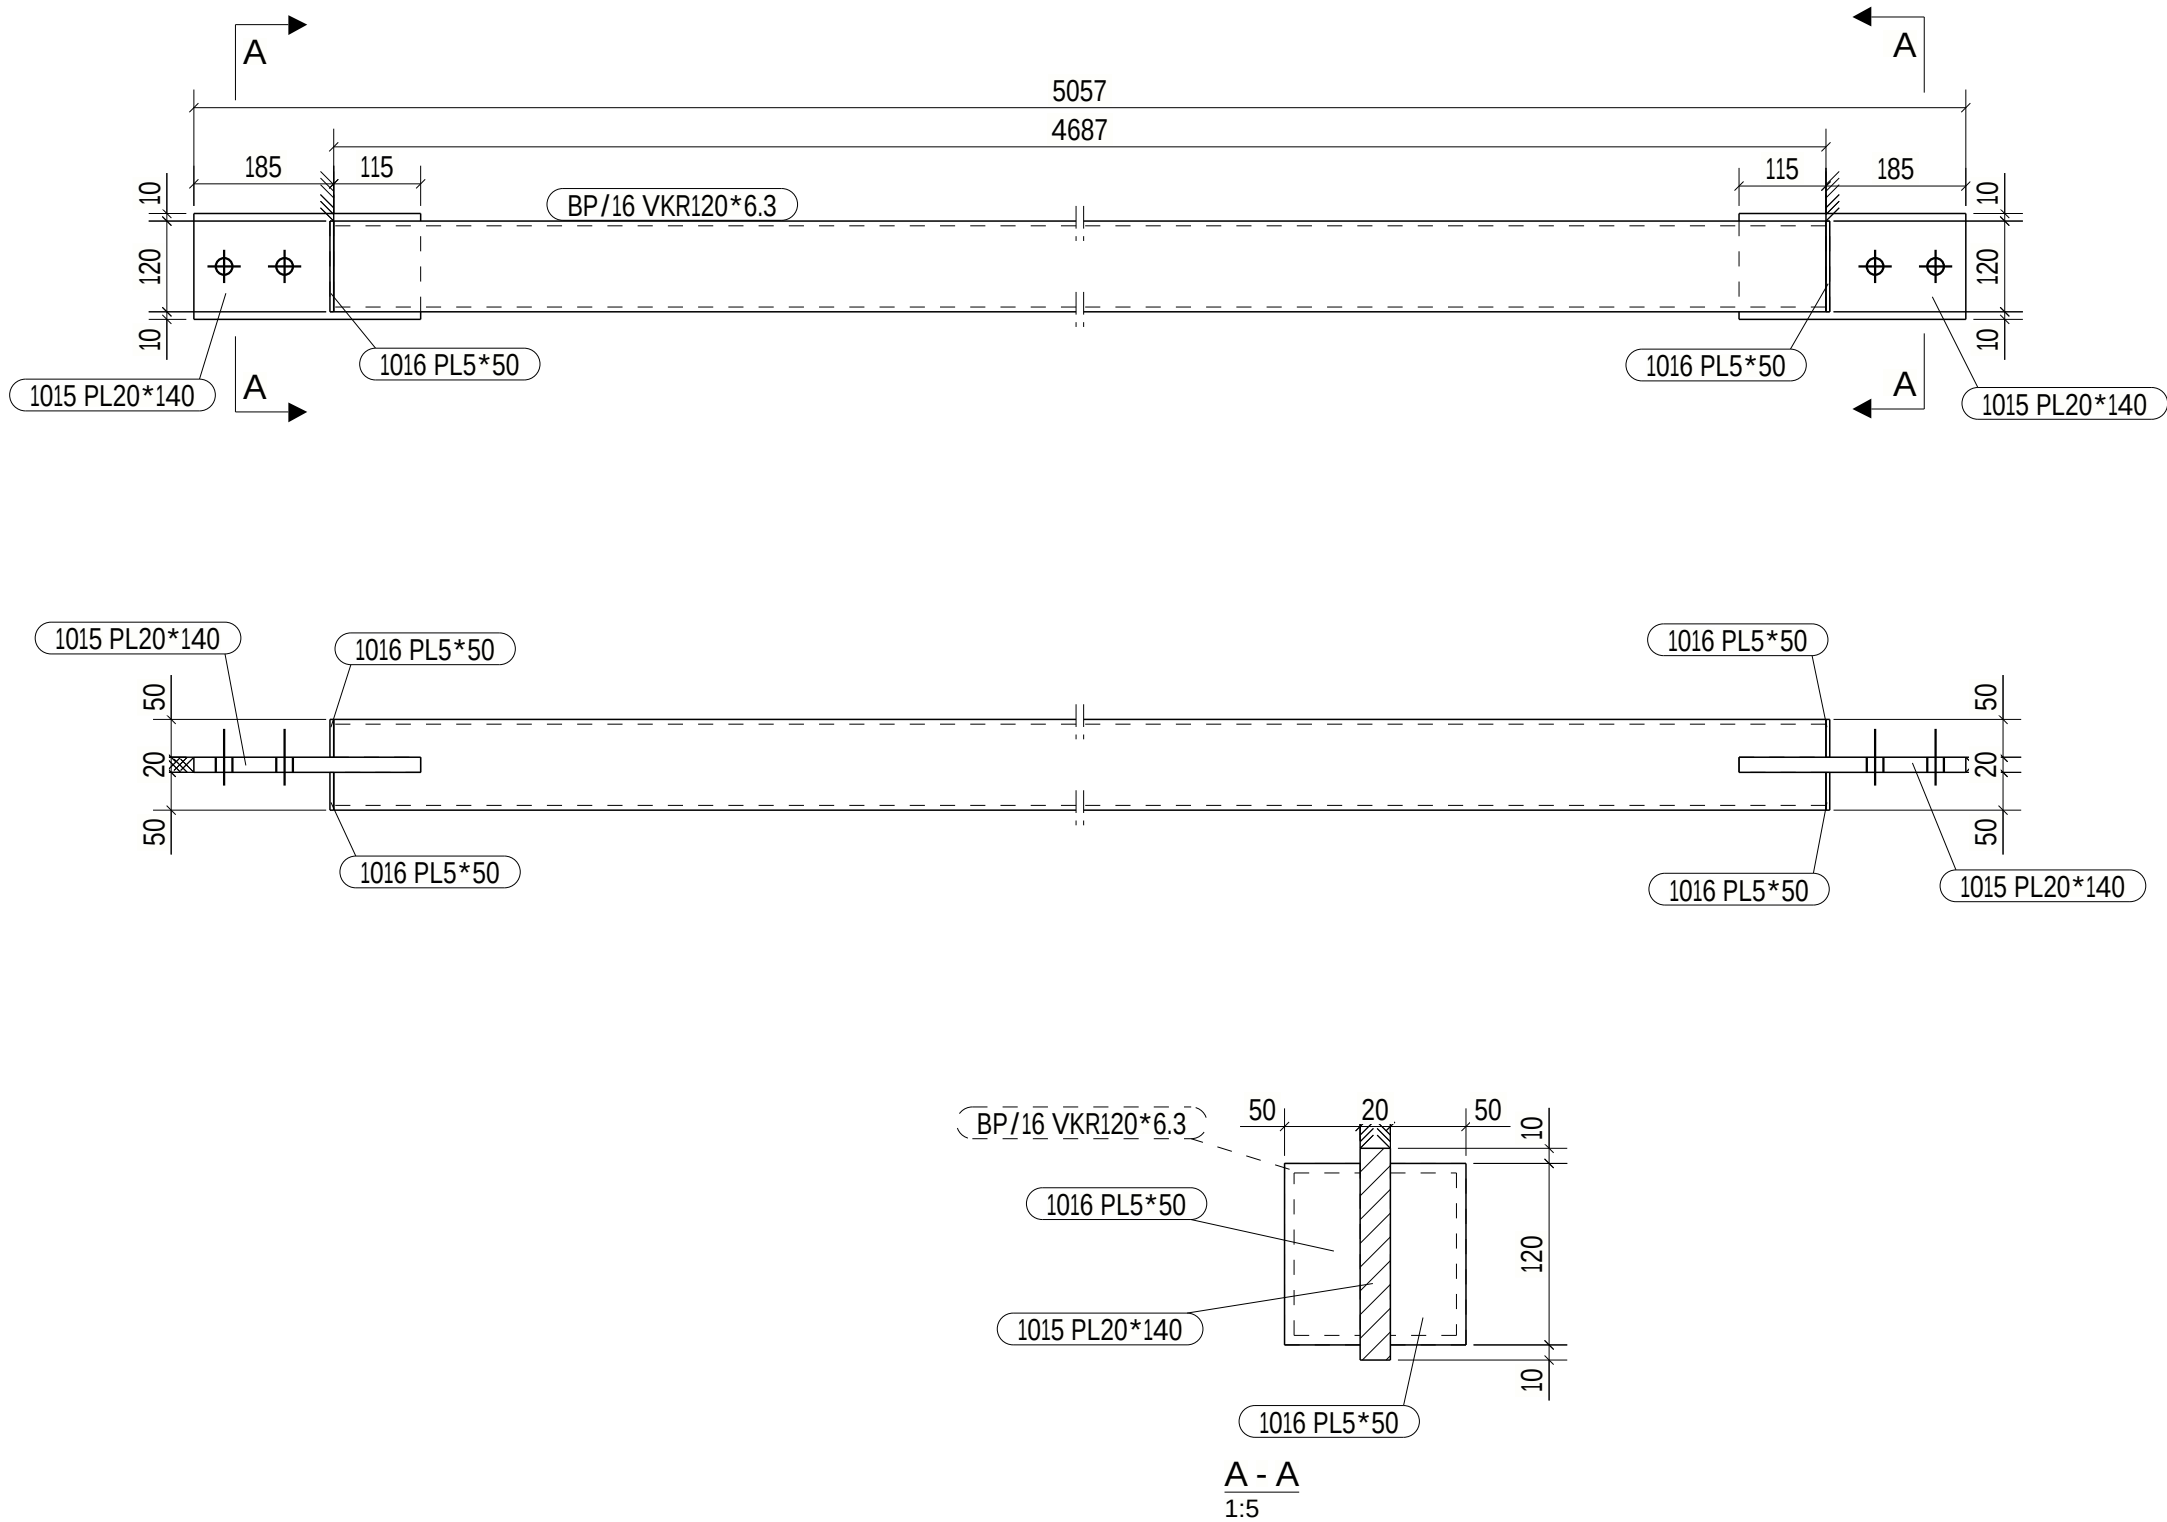

ALLMÄNNA NOTERINGAR: ALLA SVETSAR ÄR KÄLSVETS a5 OM EJ ANNAT ANGES

MATERIALLISTA FÖR ETT GODS MÄRKT: B/10						1 st. TILLVERKAS
STYCKLIT.	PROFIL	MATERIAL	ANT.	LÄNGD	AREA/st	VIKT/st
BP/16	VKR120*6.3	S355J2H	1	4687	2.2	103.8
1015	PL20*140	S355J2	2	300	0.1	6.6
1016	PL5*50	S355J2	4	120	0.0	0.2
TOTALT					2.4	117.9

Norconsult 	ANSVARIG PART	PROJEKT	FÖRFRÅGNINGSUNDERLAG		STATUS
	KONTAKTPERSON	CENTRALEKÖ ROBERTSFORS KOMMUN	BYGGHANDLING		HANDLING
	GODKÄND AV	TILLVERKNINGSRITNINGAR STÅL	ÄNDRING		FORMAT
	SKAPAD AV	INNEHÅLL	2024-12-20		DATUM
PARTS			1:5		SKALA
			B/10		BET