
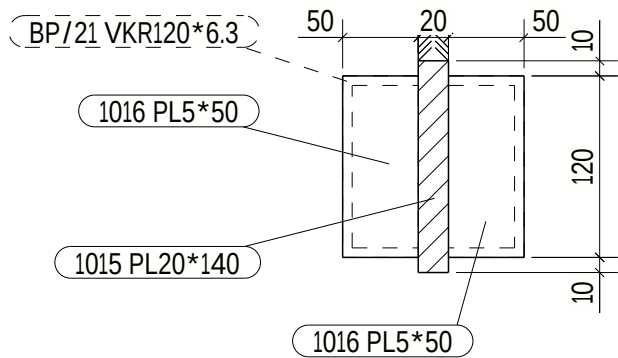
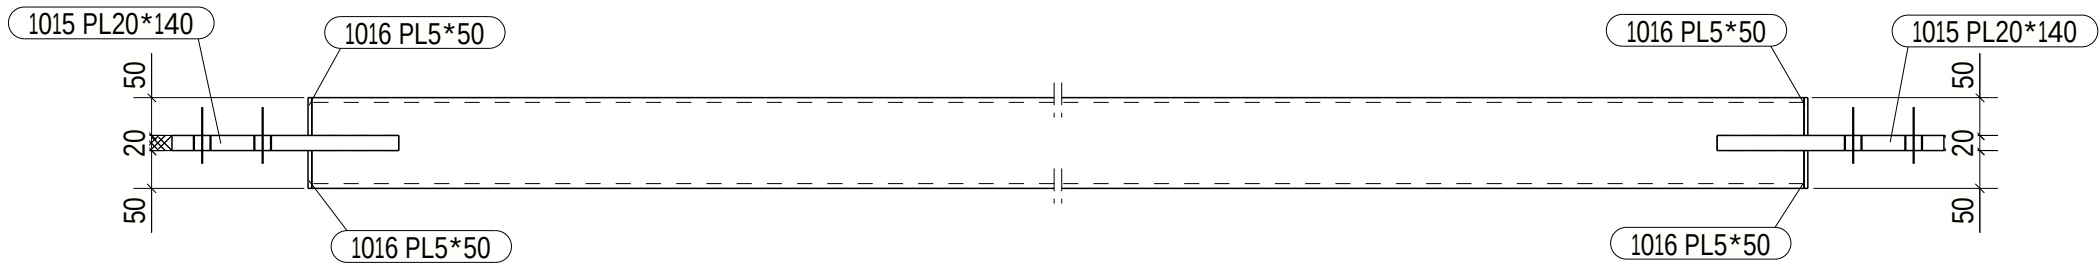


PLACERING I STOMNÄT	
NUMMER	SYSTEMLINJE
B/15	4-5/D

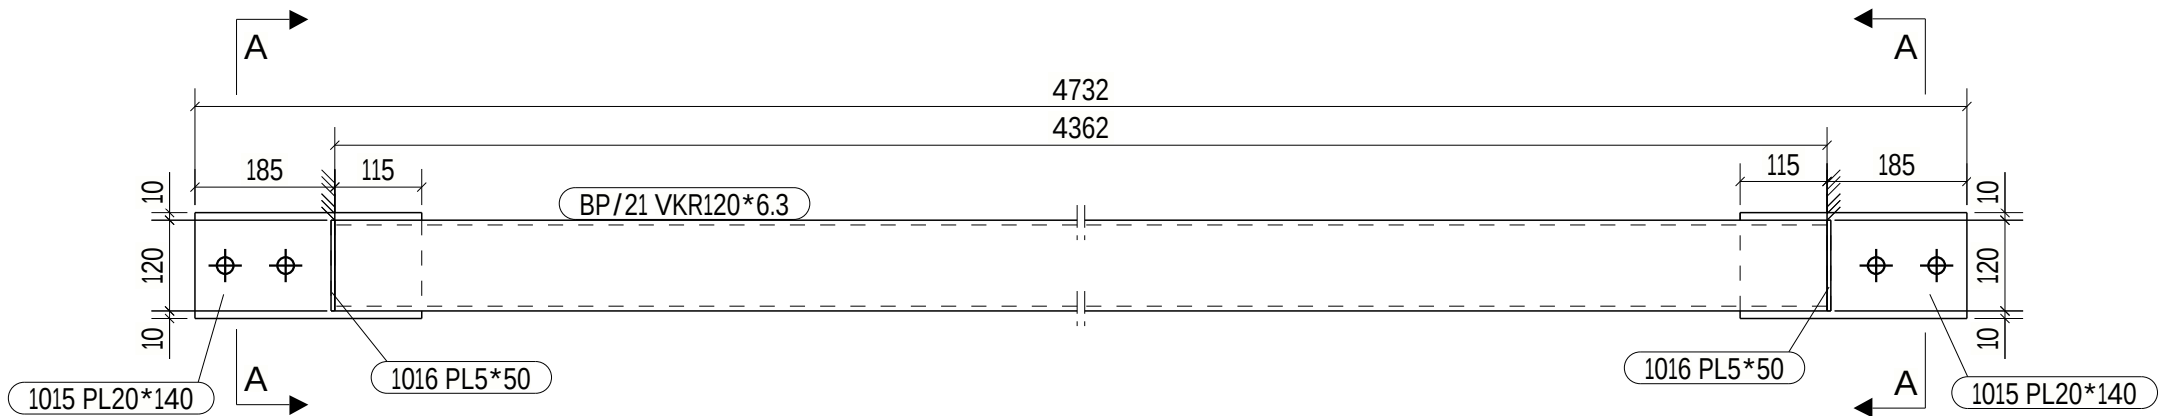

A - A
1:5

ALLMÄNNA NOTERINGAR: ALLA SVETSAR ÄR KÄLSVETS a5 OM EJ ANNAT ANGES

MATERIALLISTA FÖR ETT GODS MÄRKT: B/15						1 st. TILLVERKAS
STYCKLIT.	PROFIL	MATERIAL	ANT.	LÄNGD	AREA/st	VIKT/st
BP/21	VKR120*6.3	S355J2H	1	4362	2.0	96.6
1015	PL20*140	S355J2	2	300	0.1	6.6
1016	PL5*50	S355J2	4	120	0.0	0.2
TOTALT					2.3	110.7

Norconsult 	ANSVARIG PART	PROJEKT	FÖRFRÅGNINGSUNDERLAG		STATUS
	KONTAKTPERSON	CENTRALEKÖ ROBERTSFORS KOMMUN	BYGGHANDLING		HANDLING
	GODKÄND AV	TILLVERKNINGSRITNINGAR STÅL	ÄNDRING		FORMAT
	SKAPAD AV	INNEHÅLL	2024-12-20	DATUM	A3
PARTS			NUMMER	1:5	SKALA
			B/15	BET	