
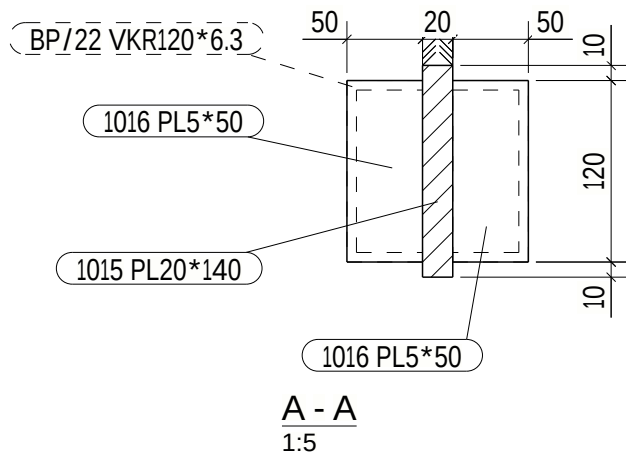
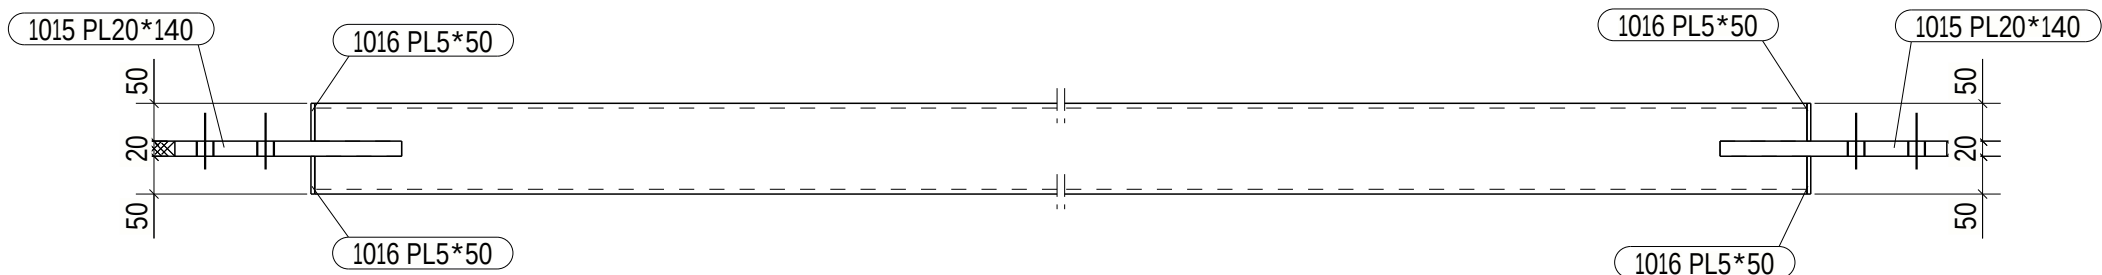


PLACERING I STOMNÄT	
NUMMER	SYSTEMLINJE
B/16	4-5/D

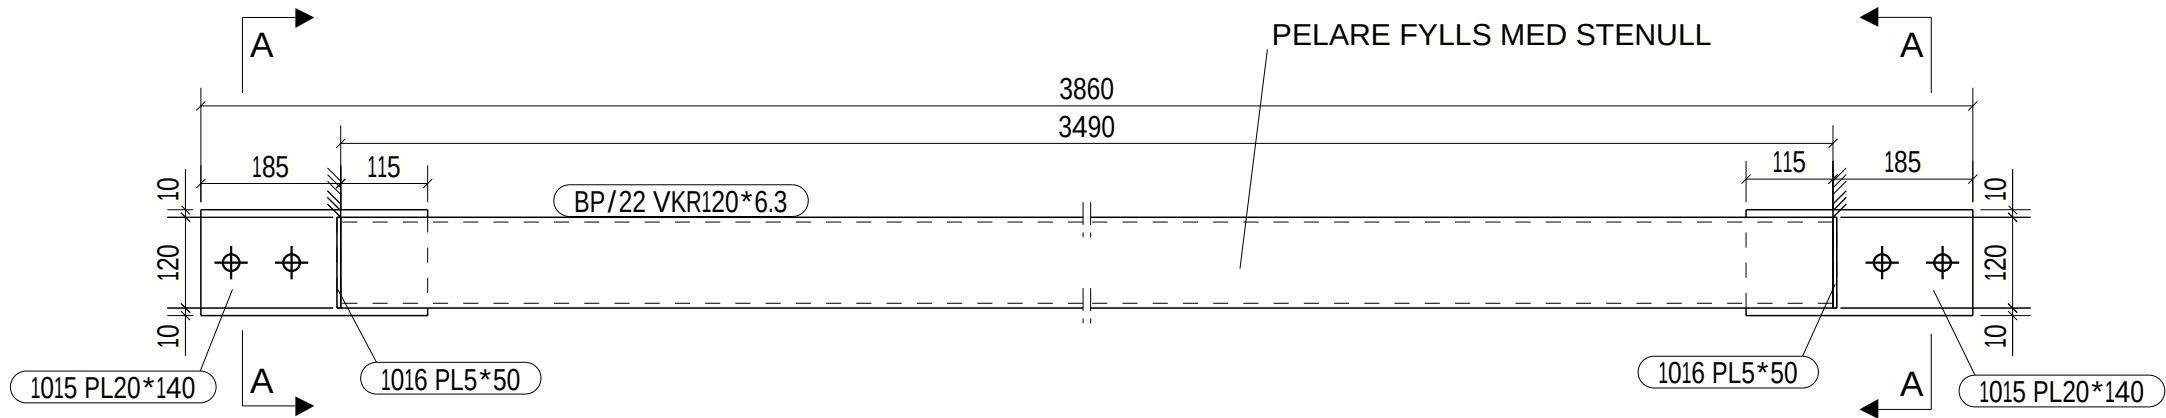

ALLMÄNNA NOTERINGAR: ALLA SVETSAR ÄR KÄLSVETS a5 OM EJ ANNAT ANGES

MATERIALLISTA FÖR ETT GODS MÄRKT: B/16 1 st. TILLVERKAS						
STYCKLIT.	PROFIL	MATERIAL	ANT.	LÄNGD	AREA/st	VIKT/st
BP/22	VKR120*6.3	S355J2H	1	3490	1.6	77.3
1015	PL20*140	S355J2	2	300	0.1	6.6
1016	PL5*50	S355J2	4	120	0.0	0.2
TOTALT					1.9	91.4

Norconsult  ANSVARIG PART BJÖRN LIDSTRÖM KONTAKTPERSON BJÖRN LIDSTRÖM GODKÄND AV ARVID WENNERBERG SKAPAD AV	CENTRALE KÖ ROBERTSFORS KOMMUN		FÖRFRÅGNINGSUNDERLAG		STATUS	
	TILLVERKNINGSRITNINGAR STÅL		BYGGHANDLING		HANDLING	
	PARTS		2024-12-20		A3	
			B/16		1:5	