
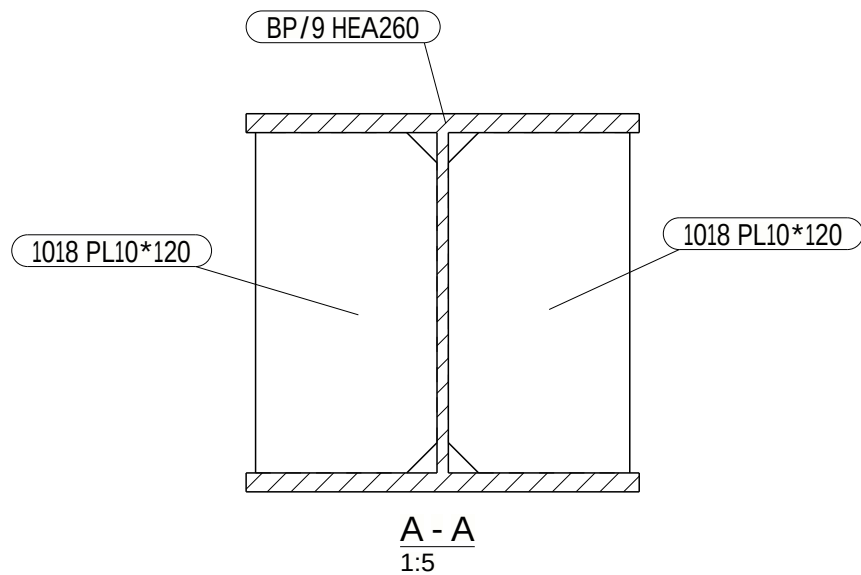
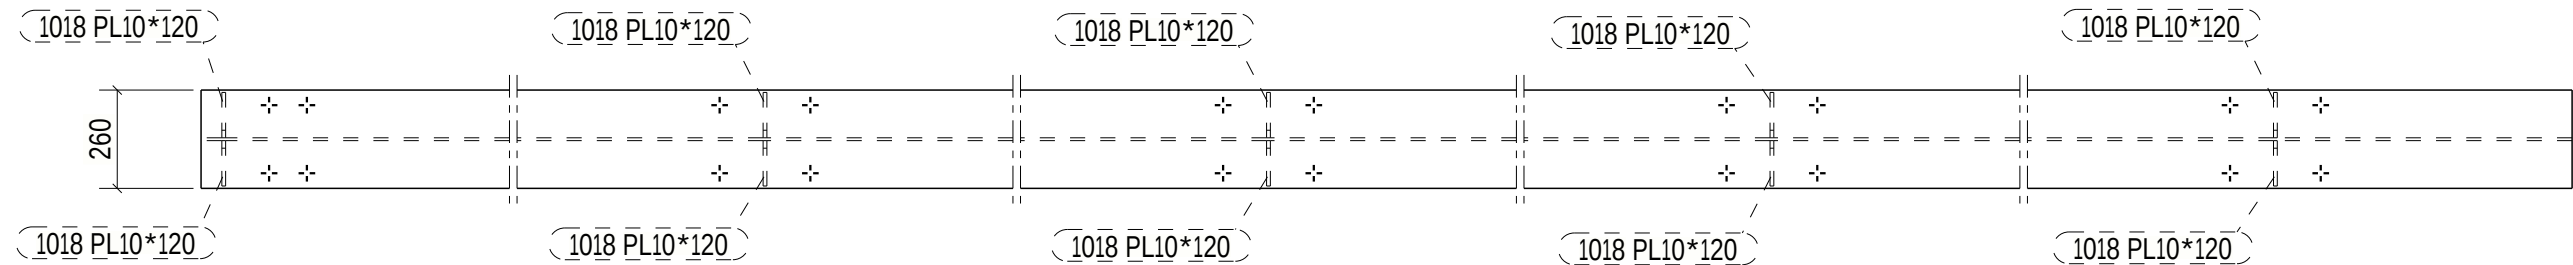


PLACERING I STOMNÄT	
NUMMER	SYSTEMLINJE
B/18	5/A-C

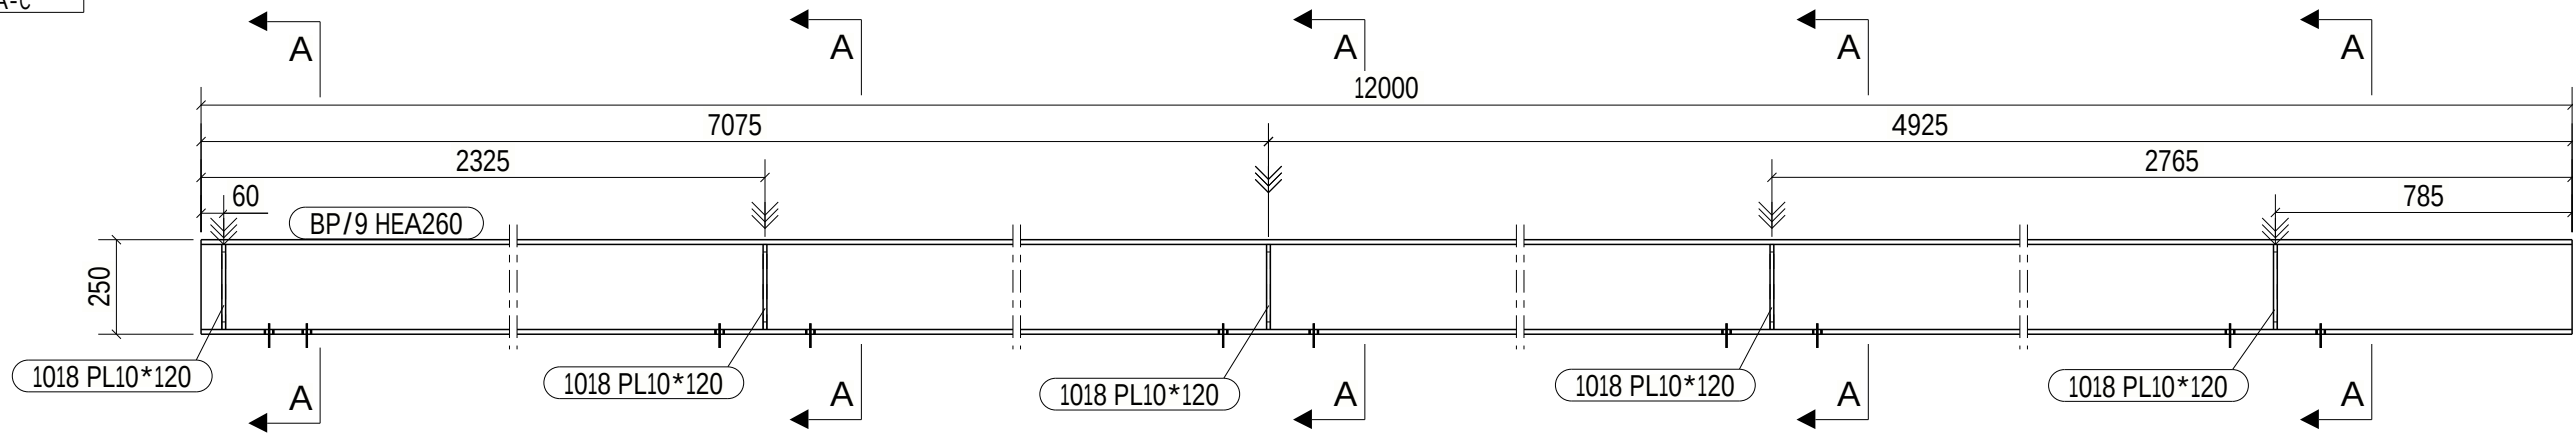

ALLMÄNNA NOTERINGAR: ALLA SVETSAR ÄR KÄLSVETS a5 OM EJ ANNAT ANGES

MATERIALLISTA FÖR ETT GODS MÄRKT: B/18 1 st. TILLVERKAS						
STYCKLIT.	PROFIL	MATERIAL	ANT.	LÄNGD	AREA/st	VIKT/st
BP/9	HEA260	S355J2	1	12000	17.8	817.8
1018	PL10*120	S355J2	10	225	0.1	2.1
TOTALT					18.4	838.7

Norconsult	ANSVARIG PART	PROJEKT	FÖRFRÅGNINGSUNDERLAG		STATUS
	KONTAKTPERSON	CENTRALKÖK ROBERTSFORS KOMMUN		BYGGHANDLING	
	GODKÄND AV	TILLVERKNINGSRITNINGAR STÅL		ÄNDRING	FORMAT
	SKAPAD AV	INNEHÅLL		DATUM	SKALA
PARTS		2024-12-20		1:20	BET
		B/18		NUMMER	