
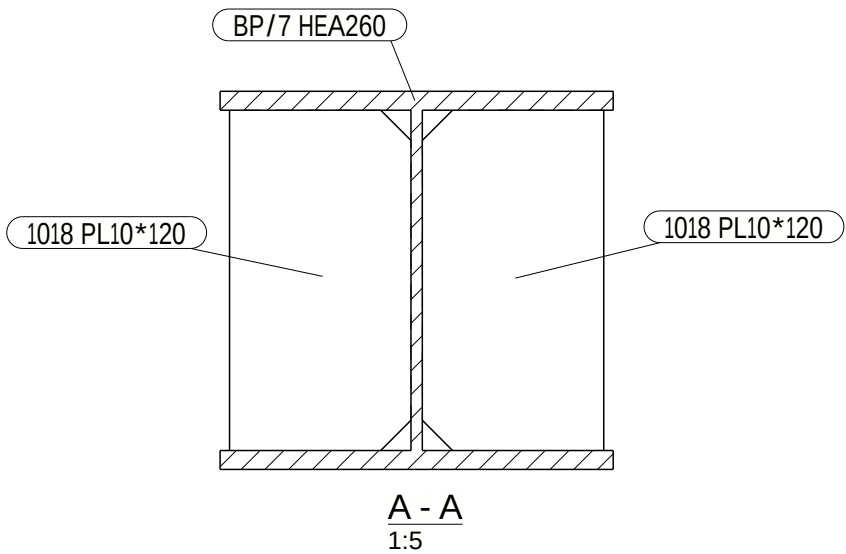
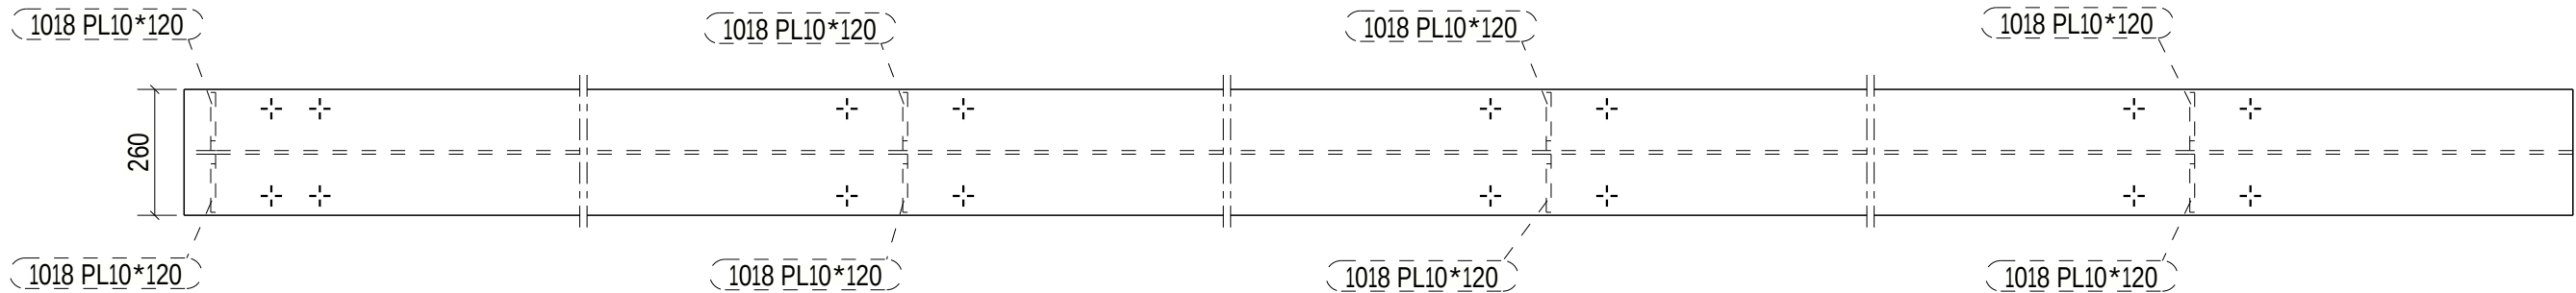


PLACERING I STOMNÄT	
NUMMER	SYSTEMLINJE
B/19	3/A-C

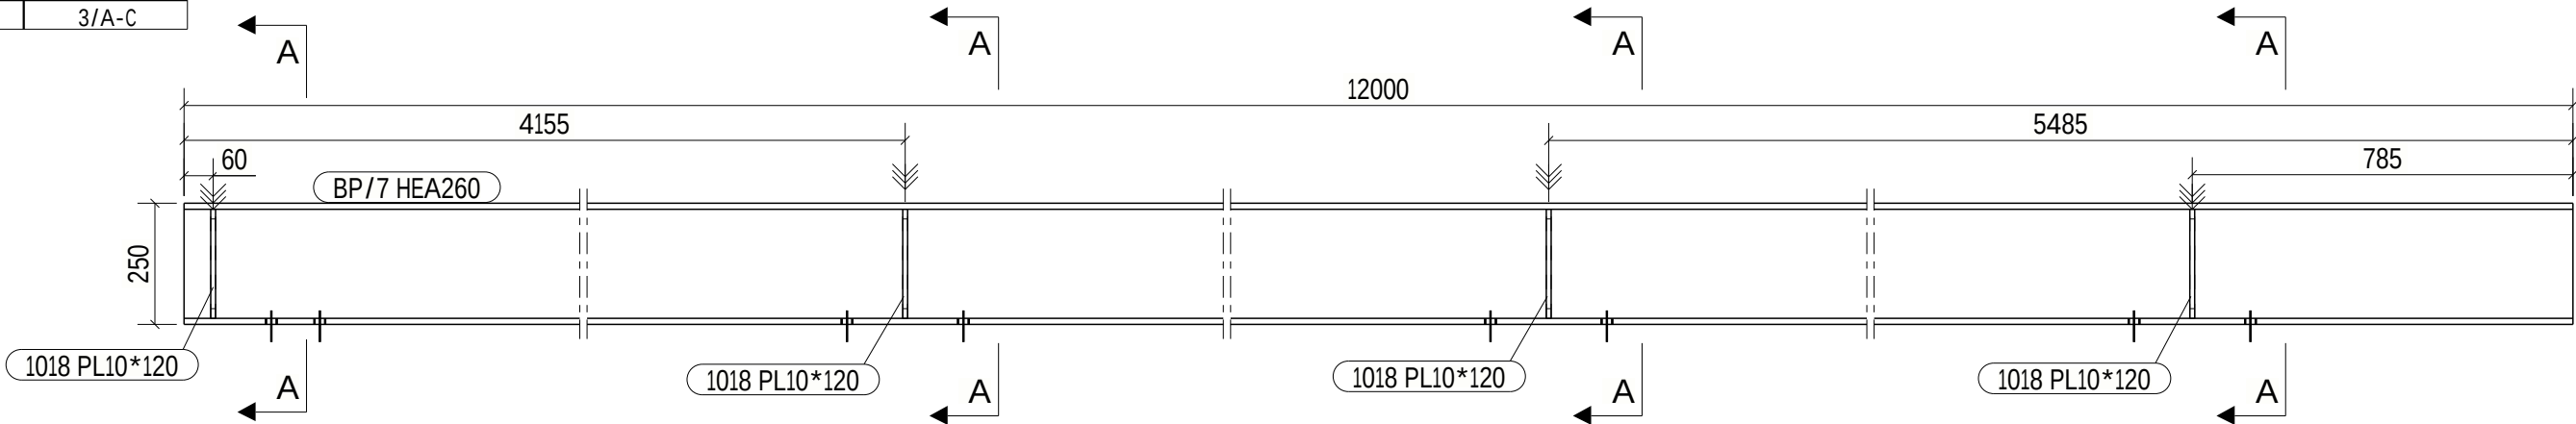

ALLMÄNNA NOTERINGAR: ALLA SVETSAR ÄR KÄLSVETS a5 OM EJ ANNAT ANGES

MATERIALLISTA FÖR ETT GODS MÄRKT: B/19 1 st. TILLVERKAS						
STYCKLIT.	PROFIL	MATERIAL	ANT.	LÄNGD	AREA/st	VIKT/st
BP/7	HEA260	S355J2	1	12000	17.8	817.8
1018	PL10*120	S355J2	8	225	0.1	2.1
TOTALT					18.3	834.5

Norconsult	ANSVARIG PART	PROJEKT	FÖRFRÅGNINGSUNDERLAG		STATUS
	KONTAKTPERSON	CENTRALKÖK ROBERTSFORS KOMMUN		BYGGHANDLING	HANDLING
	GODKÄND AV	TILLVERKNINGSRITNINGAR STÅL		ÄNDRING	FORMAT
	SKAPAD AV	2024-12-20		DATUM	SKALA
PARTS		B/19		NUMMER	BET