
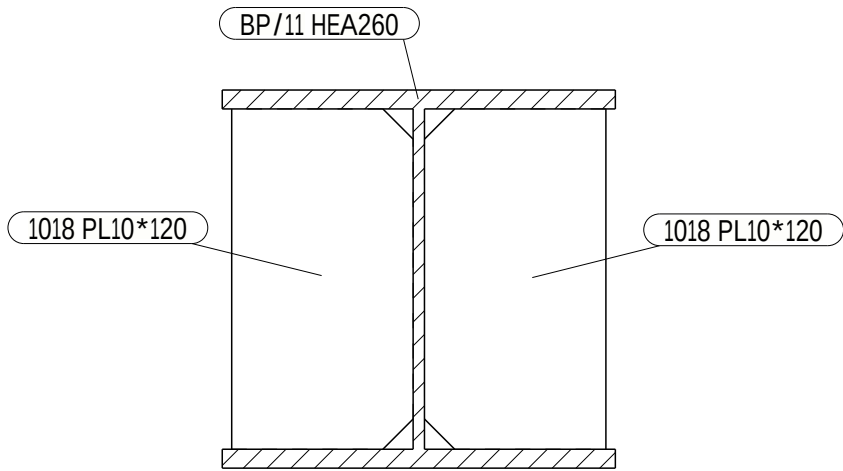
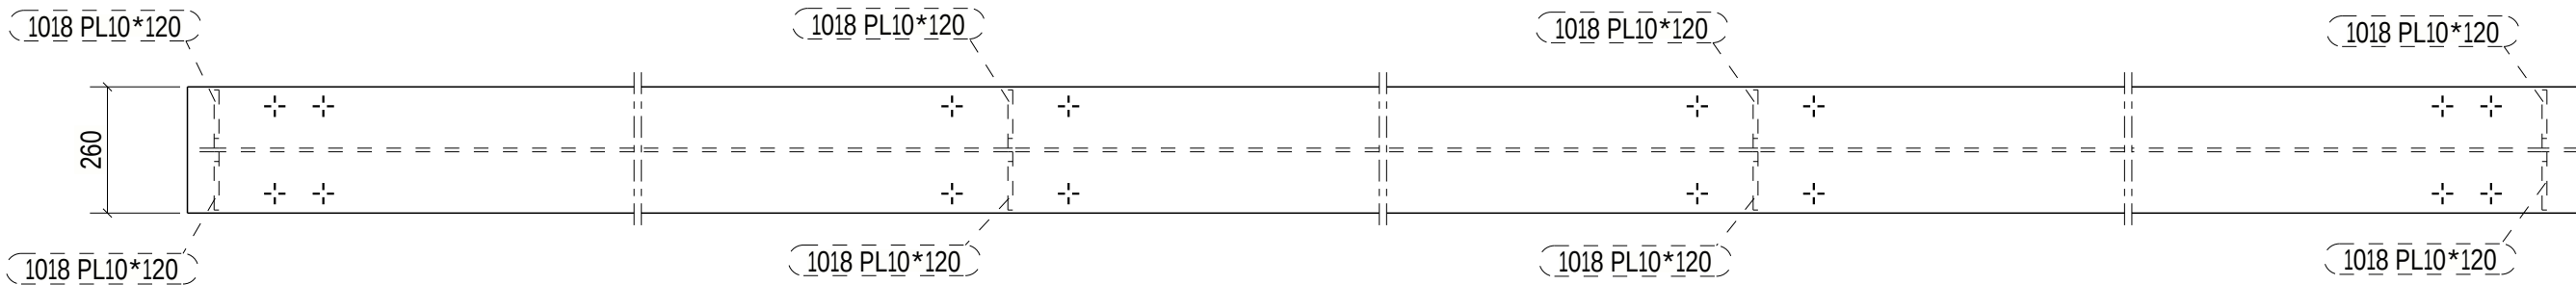


PLACERING I STOMNÄT	
NUMMER	SYSTEMLINJE
B/20	5/B-D

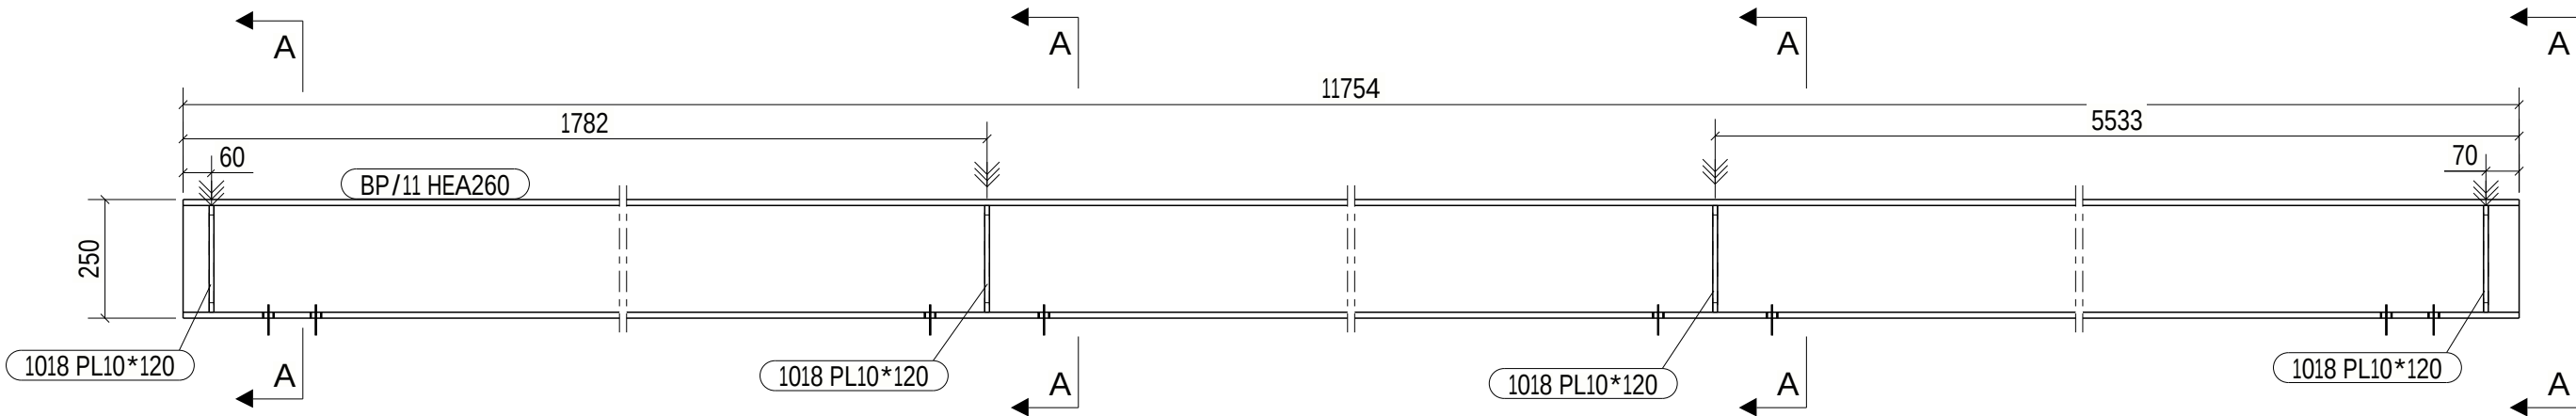

A - A
1:5

ALLMÄNNA NOTERINGAR: ALLA SVETSAR ÄR KÄLSVETS a5 OM EJ ANNAT ANGES

MATERIALLISTA FÖR ETT GODS MÄRKT: B/20						1 st. TILLVERKAS
STYCKLIT.	PROFIL	MATERIAL	ANT.	LÄNGD	AREA/st	VIKT/st
BP/11	HEA260	S355J2	1	11754	17.4	801.1
1018	PL10*120	S355J2	8	225	0.1	2.1
TOTALT					17.9	817.8

Norconsult	ANSVARIG PART	PROJEKT	FÖRFRÅGNINGSUNDERLAG		STATUS
	KONTAKTPERSON	CENTRALEKÖK ROBERTSFORS KOMMUN	BYGGHANDLING		HANDLING
	GODKÄND AV	TILLVERKNINGSRITNINGAR STÅL	ÄNDRING	FORMAT	A3
	SKAPAD AV	INNEHÅLL	DATUM	SKALA	1:15
PARTS			2024-12-20	NUMMER	BET
			B/20		