
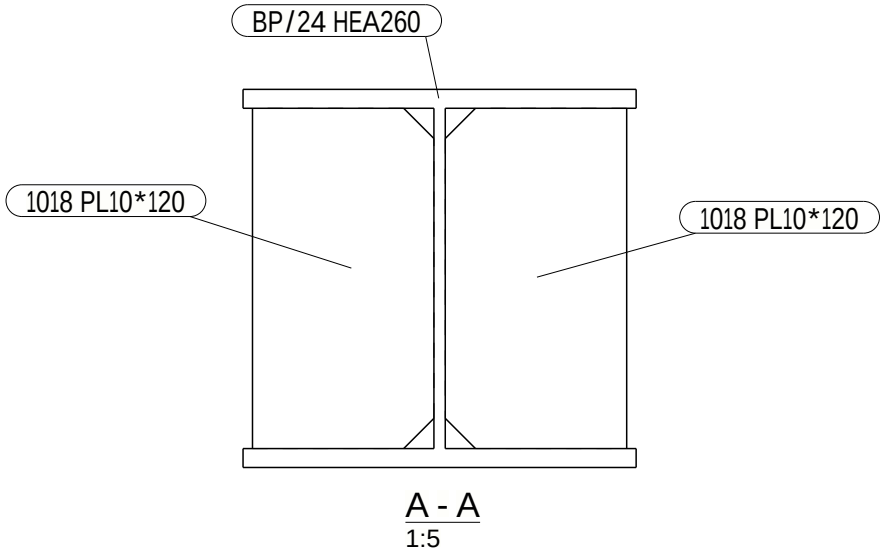


PLACERING I STOMNÄT	
NUMMER	SYSTEMLINJE
B/21	4/B-C

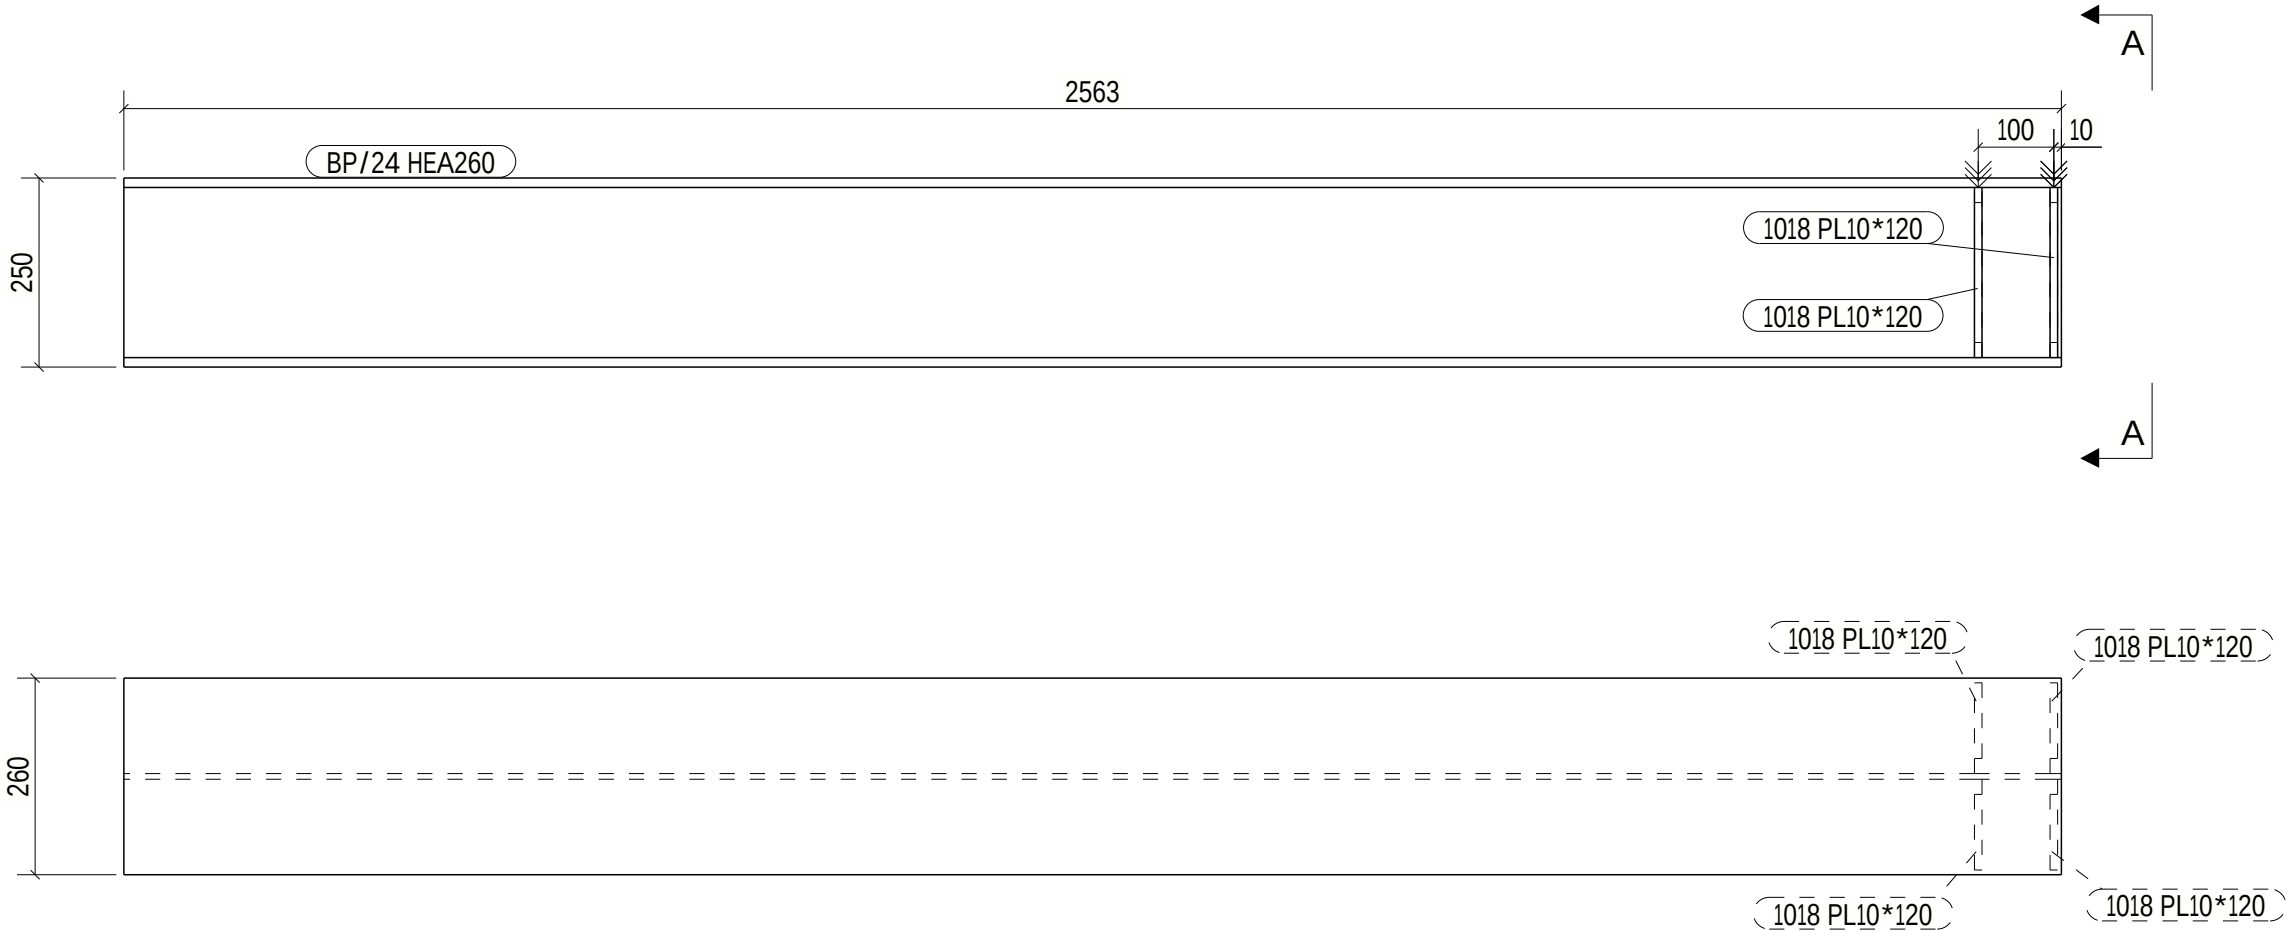

ALLMÄNNA NOTERINGAR: ALLA SVETSAR ÄR KÄLSVETS a5 OM EJ ANNAT ANGES

MATERIALLISTA FÖR ETT GODS MÄRKT: B/21 1 st. TILLVERKAS						
STYCKLIT.	PROFIL	MATERIAL	ANT.	LÄNGD	AREA/st	VIKT/st
BP/24	HEA260	S355J2	1	2563	3.8	174.7
1018	PL10*120	S355J2	4	225	0.1	2.1
TOTALT					4.0	183.0

Norconsult ANSVARIG PART BJÖRN LIDSTRÖM BJÖRN LIDSTRÖM ARVID WENNERBERG	CENTRALKÖK ROBERTSFORS KOMMUN		FÖRFRÅGNINGSUNDERLAG	
	TILLVERKNINGSRITNINGAR STÅL		BYGGHANDLING	
	PARTS		2024-12-20	A3
			B/21	