
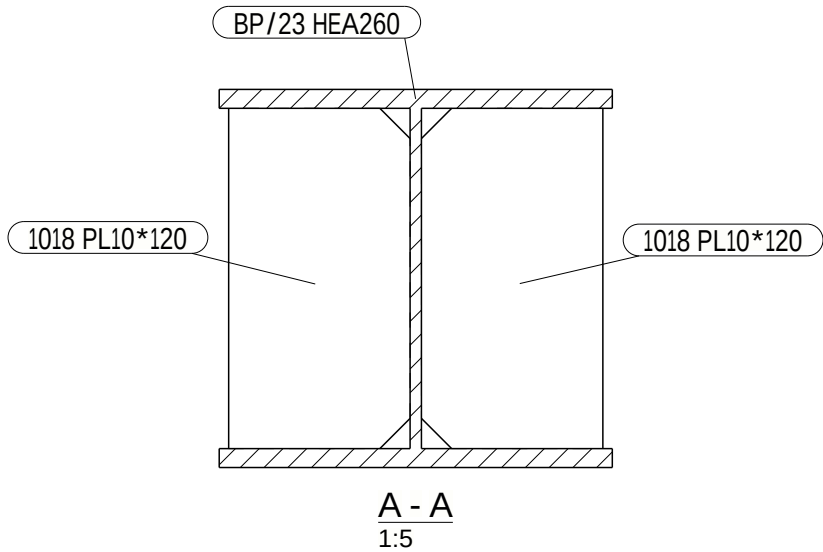


PLACERING I STOMNÄT	
NUMMER	SYSTEMLINJE
B/22	3/B-C

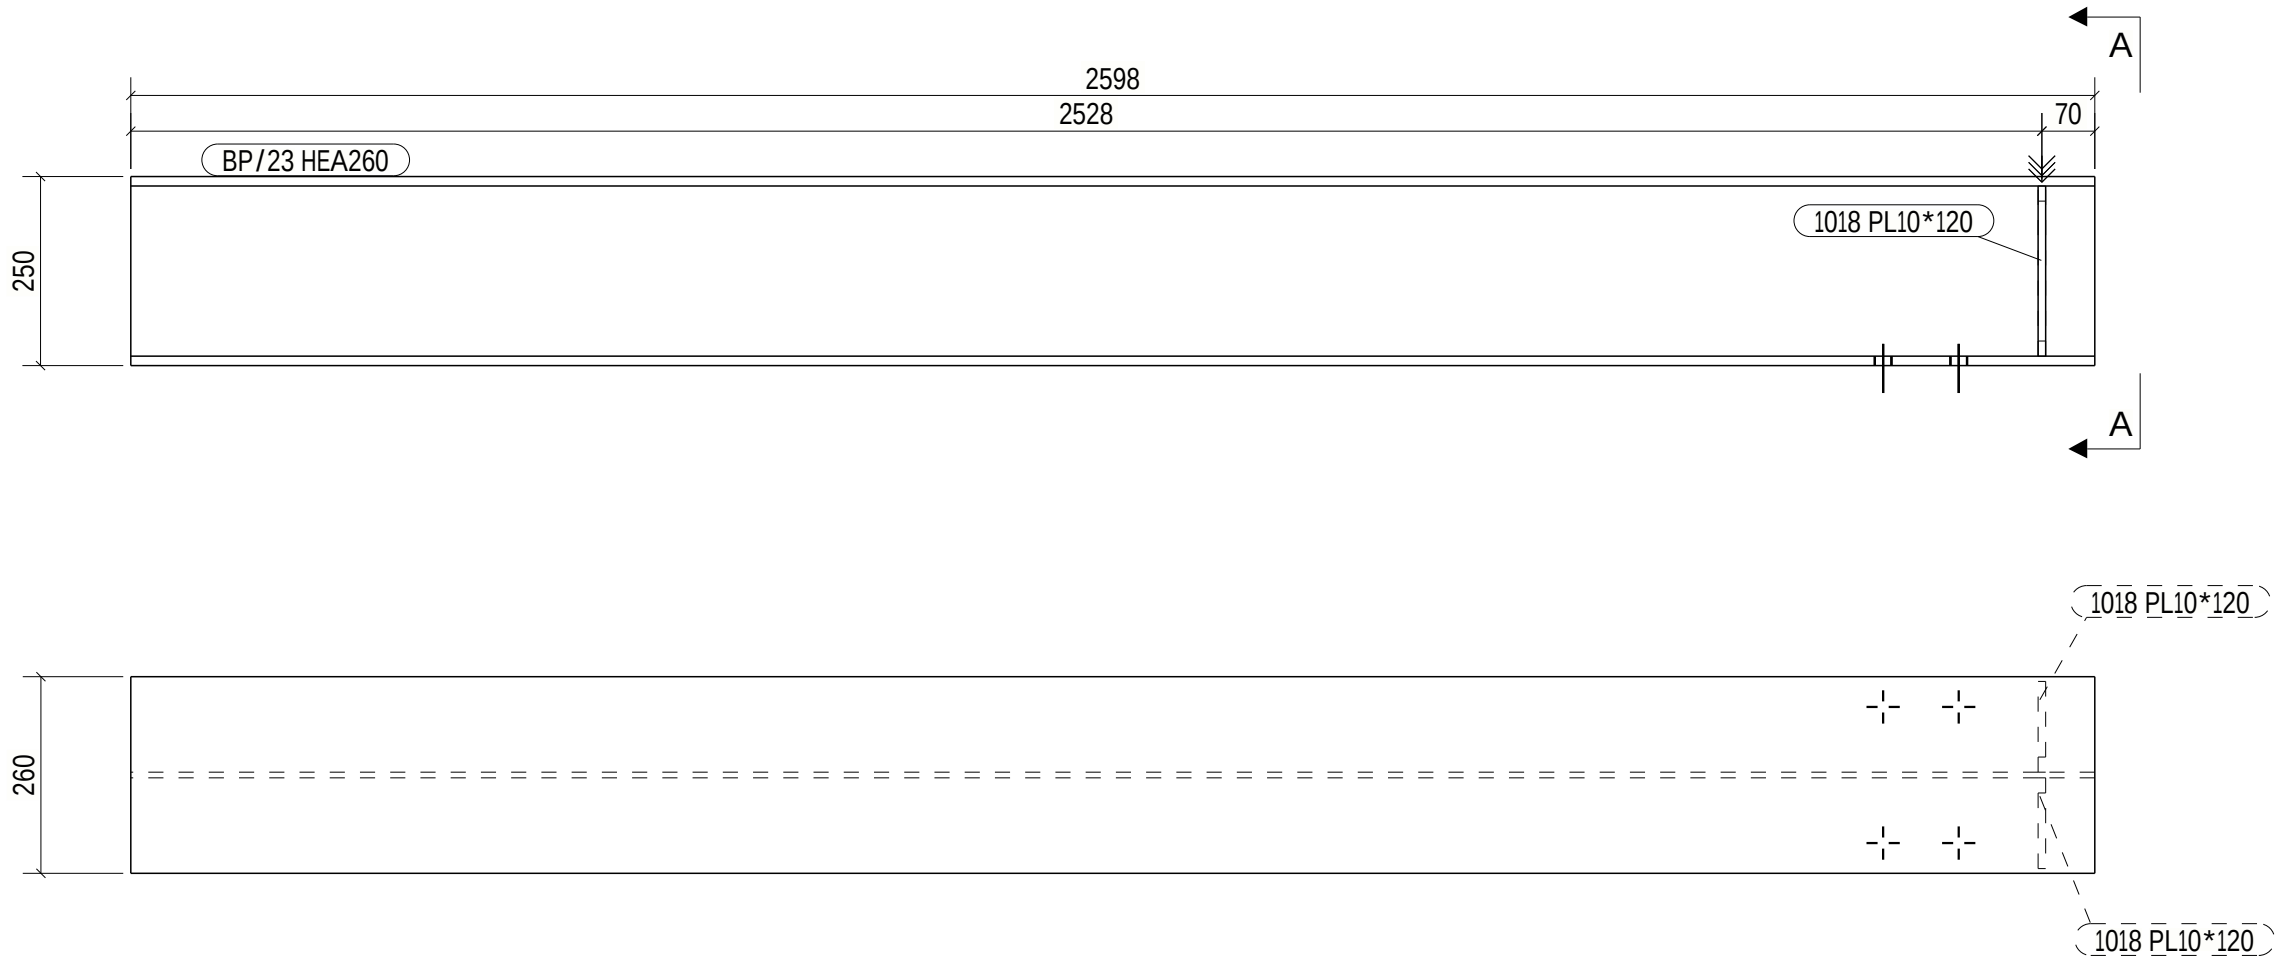

ALLMÄNNA NOTERINGAR: ALLA SVETSAR ÄR KÄLSVETS a5 OM EJ ANNAT ANGES						
MATERIALLISTA FÖR ETT GODS MÄRKT: B/22 1 st. TILLVERKAS						
STYCKLIT.	PROFIL	MATERIAL	ANT.	LÄNGD	AREA/st	VIKT/st
BP/23	HEA260	S355J2	1	2598	3.9	177.1
1018	PL10*120	S355J2	2	225	0.1	2.1
TOTALT					4.0	181.2

Norconsult 	ANSVARIG PART	PROJEKT	FÖRFRÅGNINGSUNDERLAG		STATUS
	KONTAKTPERSON	CENTRALKÖK ROBERTSFORS KOMMUN	BYGGHANDLING		HANDLING
	GODKÄND AV	TILLVERKNINGSRITNINGAR STÅL	ÄNDRING		FORMAT
	SKAPAD AV	INNEHÅLL	2024-12-20	DATUM	A3
PARTS			1:5	SKALA	BET
			B/22	NUMMER	