

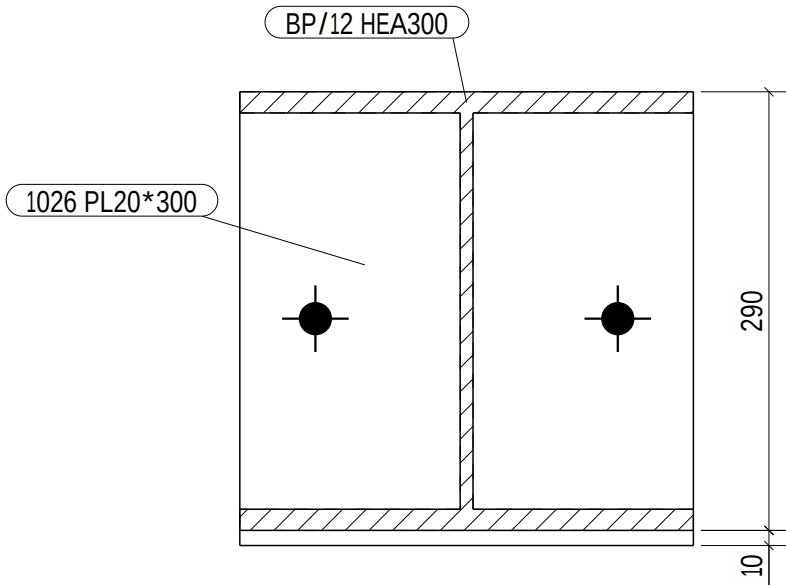
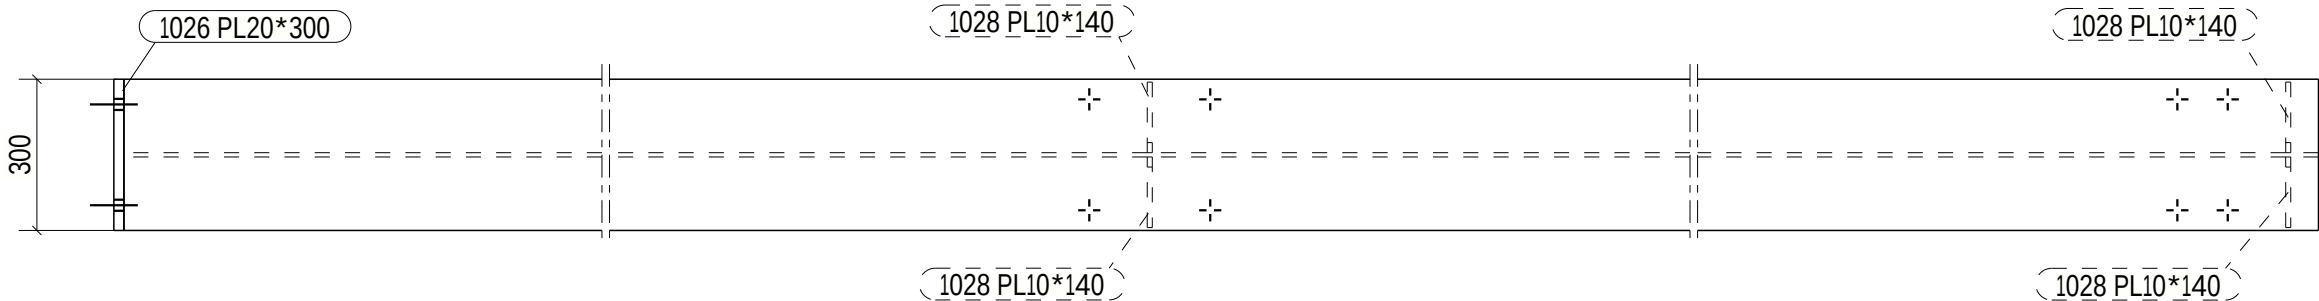


PLACERING I STOMNÄT	
NUMMER	SYSTEMLINJE
B/23	4/B-D

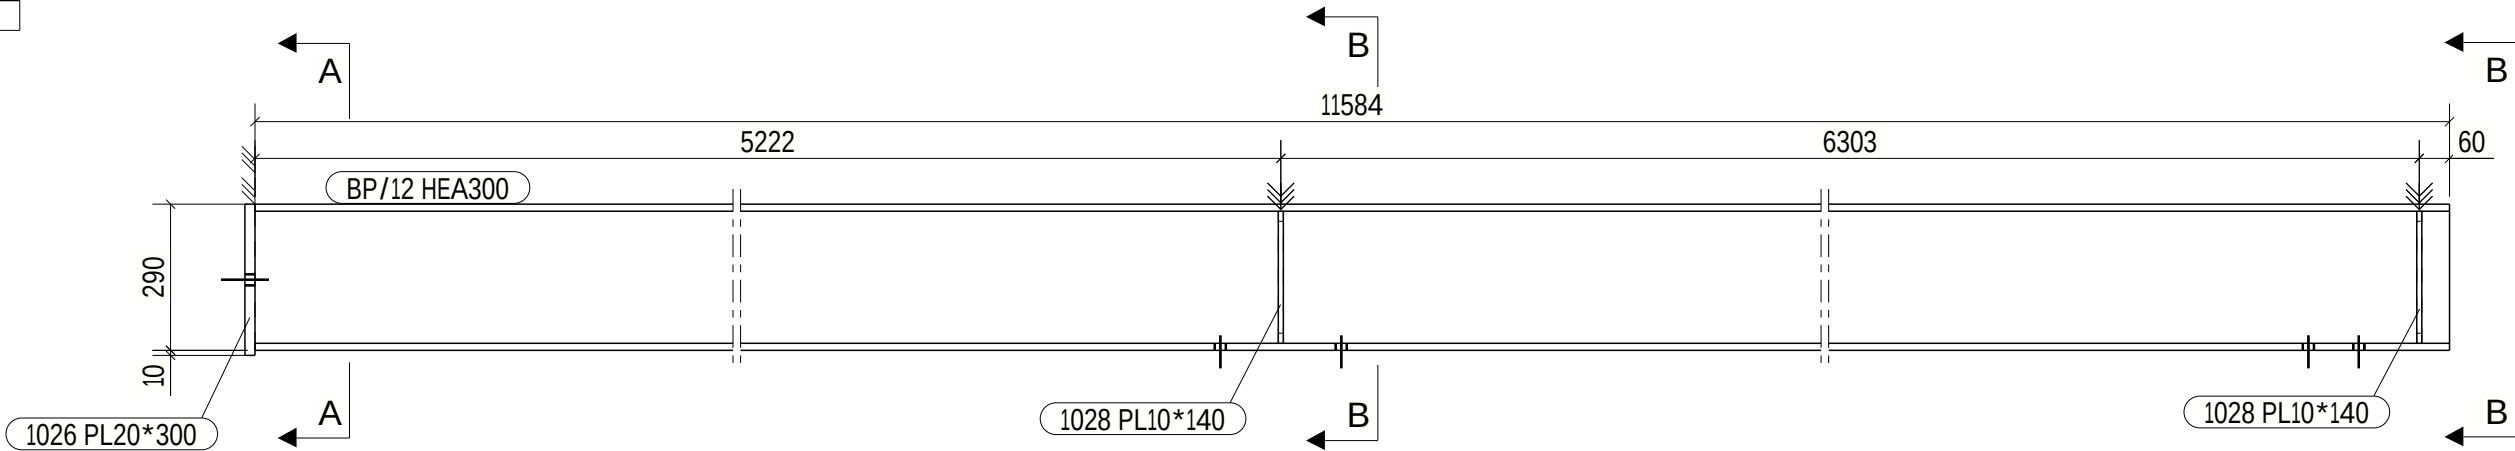

A - A
1:5

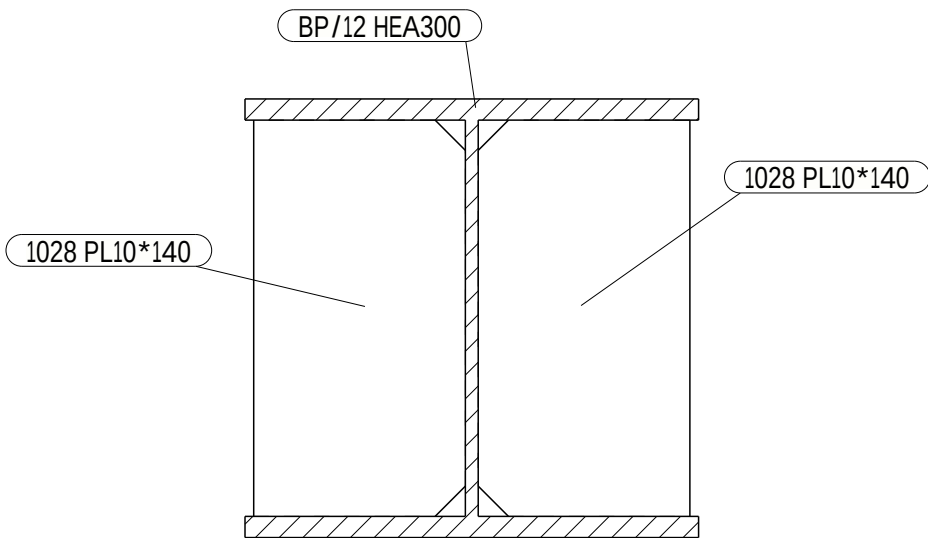

B - B
1:5

ALLMÄNNA NOTERINGAR: ALLA SVETSAR ÄR KÄLSVETS a5 OM EJ ANNAT ANGES

MATERIALLISTA FÖR ETT GODS MÄRKT: B/23						1 st. TILLVERKAS
STYCKLIT.	PROFIL	MATERIAL	ANT.	LÄNGD	AREA/st	VIKT/st
BP/12	HEA300	S355J2	1	11584	19.9	1023.1
1026	PL20*300	S355J2	1	300	0.2	14.1
1028	PL10*140	S355J2	4	262	0.1	2.8
TOTALT					20.4	1048.6

Norconsult	ANSVARIG PART	PROJEKT	FÖRFRÅGNINGSUNDERLAG		STATUS
	KONTAKTPERSON	CENTRALEKÖB ROBERTSFORS KOMMUN	BYGGHANDLING		HANDLING
	GODKÄND AV	TILLVERKNINGSRITNINGAR STÅL	2024-12-20		ANDRING
	SKAPAD AV	PARTS	B/23		FORMAT