PLACERING I STOMNÄT	
NUMMER	SYSTEMLINJE
B/24	4-5/D

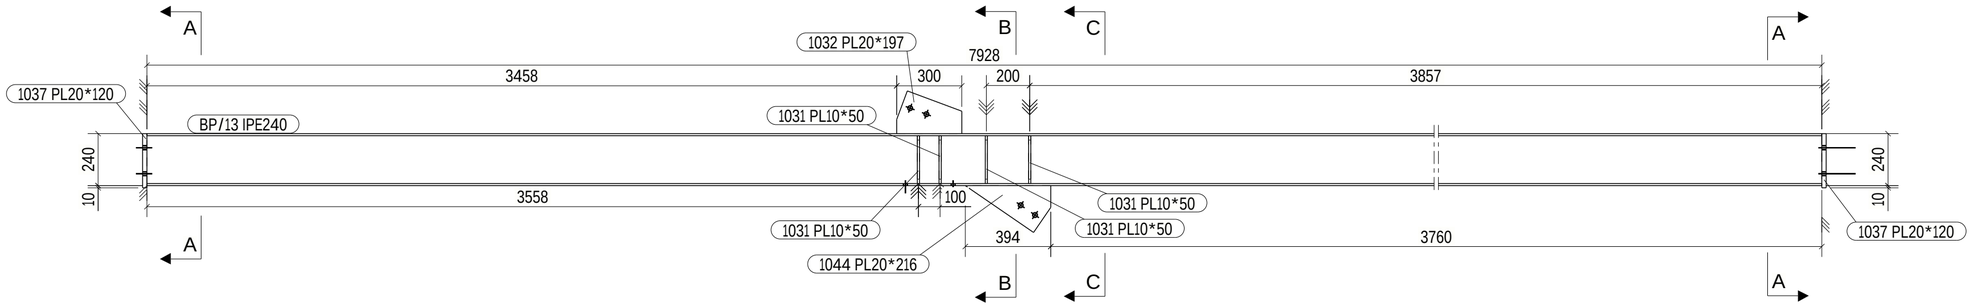

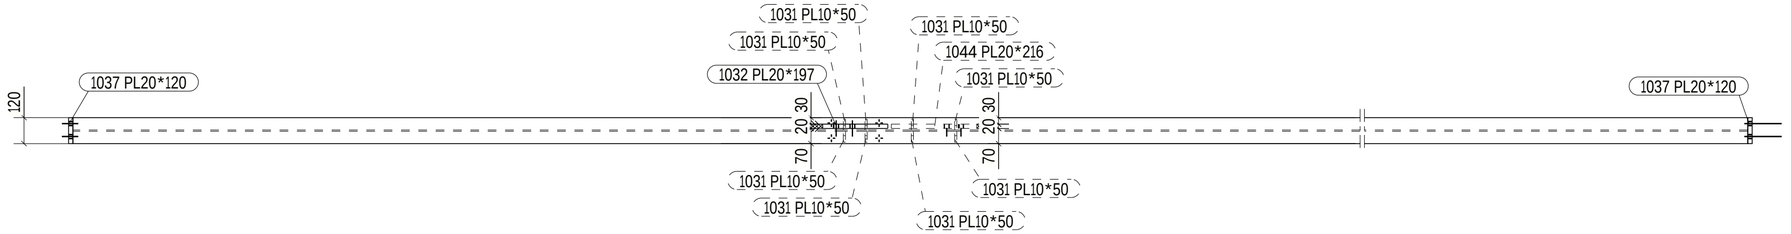

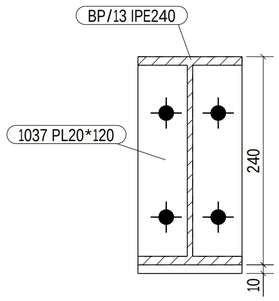

A - A
1:5

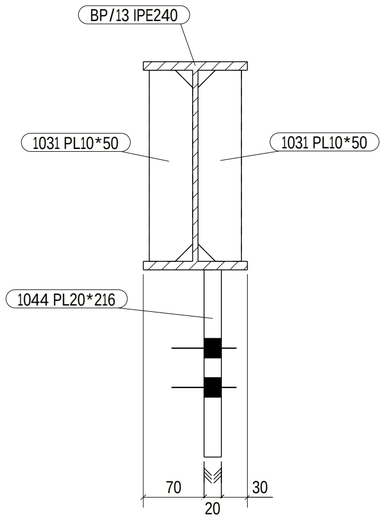

C - C
1:5

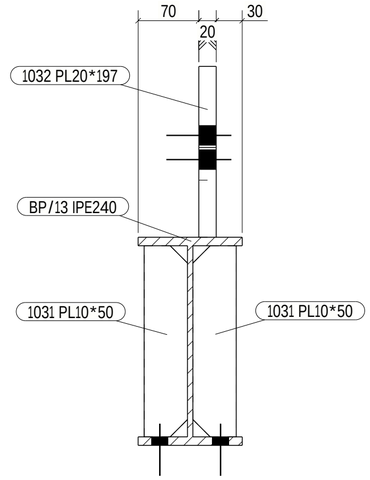

B - B
1:5

ALLMÄNNA NOTERINGAR:

ALLA HÅL ÄR 22 mm OM EJ ANNAT ANGES
ALLA SVETSAR ÄR 6.5 mm OM EJ ANNAT ANGES

MATERIALLISTA FÖR ETT GODS MÄRKT: B/24 — 1 st. TILLVERKAS

STYCKLIT.	PROFIL	MATERIAL	ANT.	LÄNGD	AREA/st	VIKT/st
BP/13	IPE240	S355J2	1	7928	7.3	243.3
1044	PL20*216	S355J2	1	394	0.1	7.3
1032	PL20*197	S355J2	1	300	0.1	6.9
1037	PL20*120	S355J2	2	250	0.1	4.7
1031	PL10*50	S355J2	8	220	0.0	0.8
				TOTALT	7.9	273.6

ANSVARIG PART: Norconsult	PROJEKT: CENTRALKÖK ROBERTSFORS KOMMUN	STATUS: FÖRFRÅGNINGSUNDERLAG
KONTAKTPERSON: BJÖRN LIDSTRÖM	RITNINGSKATEGOR: TILLVERKNINGSRITNINGAR STÅL	HANDLING: BYGGHANDLING
GODKÄND AV: BJÖRN LIDSTRÖM	INNEHÅLL: PARTS	ÄNDRING: — / FORMAT: A2
SKAPAD AV: ARVID WENNBERG		DATUM: 2024-12-20 / SKALA: 1:20
		NUMMER: B/24 / BET:

Tekla Structures