| PLACERING I STOMNÄT | |
|---|---|
| NUMMER | SYSTEMLINJE |
| B/26 | 3-4/B |

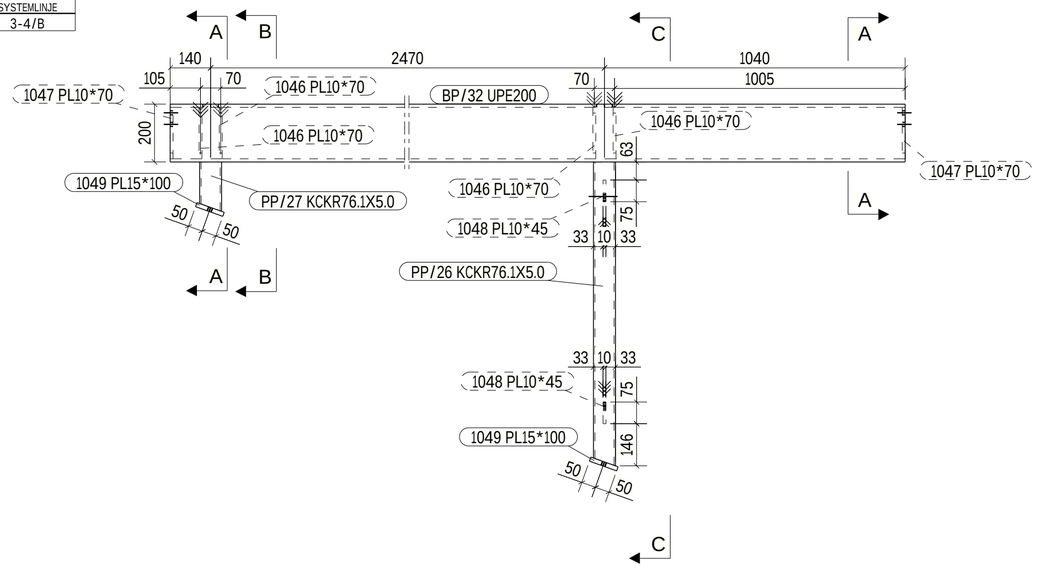


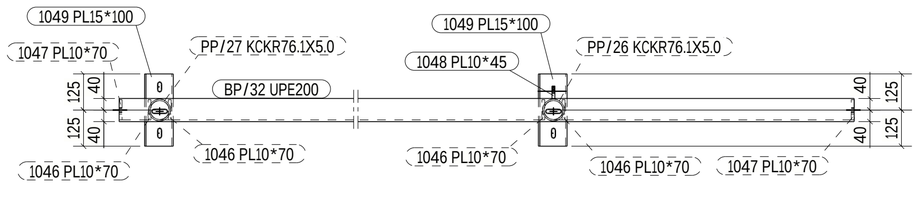


UTVÄNDIGT STÅL VARMFÖRZINKAS ENLIGT ALLMÄNNA FÖRESKRIFTER K-01-0-001 -- 003

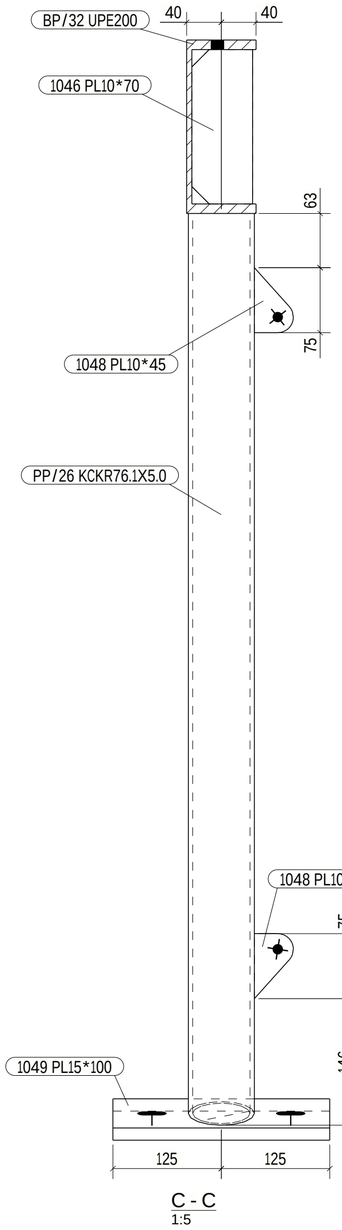


C - C
1:5

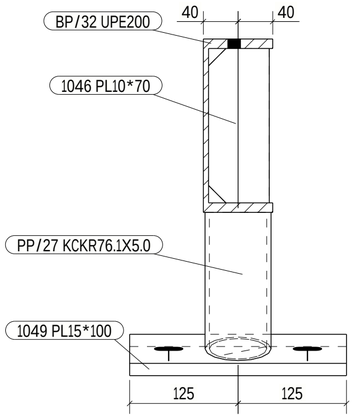


B - B
1:5

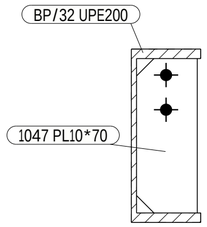


A - A
1:5

## ALLMÄNNA NOTERINGAR:

ALLA HÅL ÄR 22 mm OM EJ ANNAT ANGES
ALLA SVETSAR ÄR 6.5 mm OM EJ ANNAT ANGES

MATERIALLISTA FÖR ETT GODS MÄRKT: B/26 — 1 st. TILLVERKAS

| STYCKLIT. | PROFIL | MATERIAL | ANT. | LÄNGD | AREA/st | VIKT/st |
|---|---|---|---|---|---|---|
| BP/32 | UPE200 | S355J2 | 1 | 3650 | 2.5 | 83.1 |
| PP/26 | KCKR76.1X5.0 | S355J2 | 1 | 1051 | 0.3 | 9.2 |
| 1049 | PL15*100 | S355J2 | 2 | 250 | 0.1 | 2.9 |
| PP/27 | KCKR76.1X5.0 | S355J2 | 1 | 171 | 0.0 | 1.5 |
| 1046 | PL10*70 | S355J2 | 4 | 178 | 0.0 | 0.9 |
| 1047 | PL10*70 | S355J2 | 2 | 178 | 0.0 | 0.9 |
| 1048 | PL10*45 | S355J2 | 2 | 75 | 0.0 | 0.2 |
| | | | | TOTALT | 3.1 | 105.7 |

| | | |
|---|---|---|
| Norconsult | PROJEKT: CENTRALKÖK ROBERTSFORS KOMMUN | STATUS: FÖRFRÅGNINGSUNDERLAG |
| ANSVARIG PART: | | HANDLING: BYGGHANDLING |
| KONTAKTPERSON: BJÖRN LIDSTRÖM | RITNINGSKATEGORI: TILLVERKNINGSRITNINGAR STÅL | ÄNDRING: — FORMAT: A2 |
| GODKÄND AV: BJÖRN LIDSTRÖM | INNEHÅLL: PARTS | DATUM: 2024-12-20 SKALA: 1:15 |
| SKAPAD AV: ARVID WENNBERG | | NUMMER: B/26 BET: |

Tekla Structures