

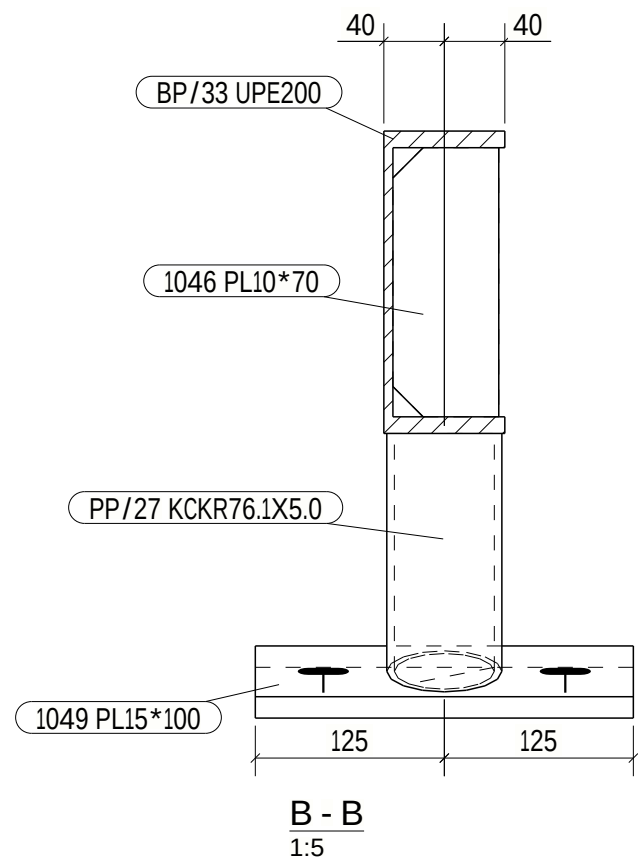
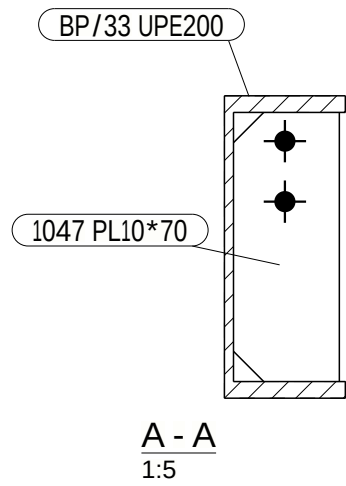


PLACERING I STOMNÄT	
NUMMER	SYSTEMLINJE
B/27	3-4/B-C

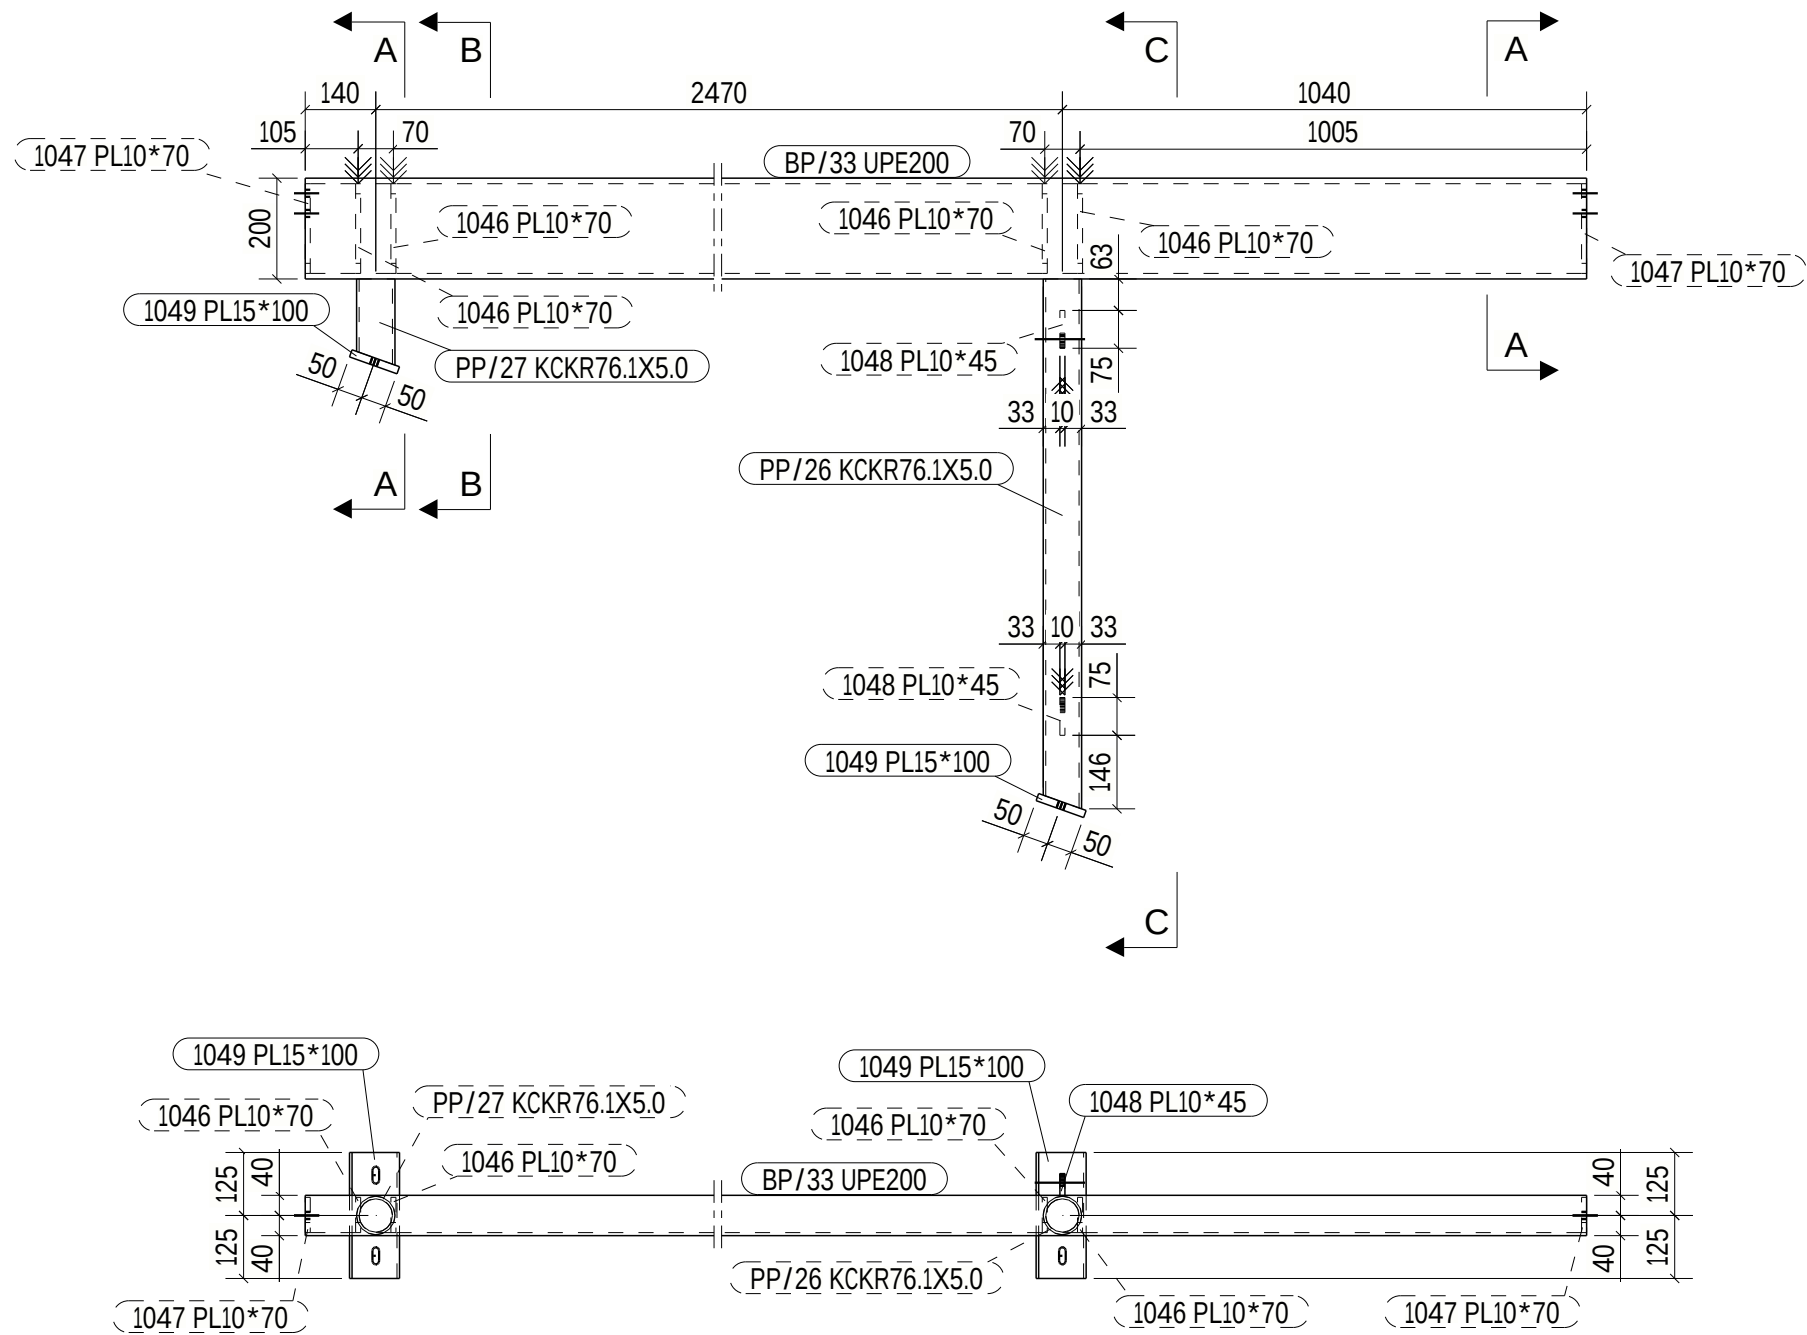

UTVÄNDIGT STÅL VARMFÖRZINKAS ENLIGT
ALLMÄNNA FÖRESKRIFTER K-01-0-001 -- 003

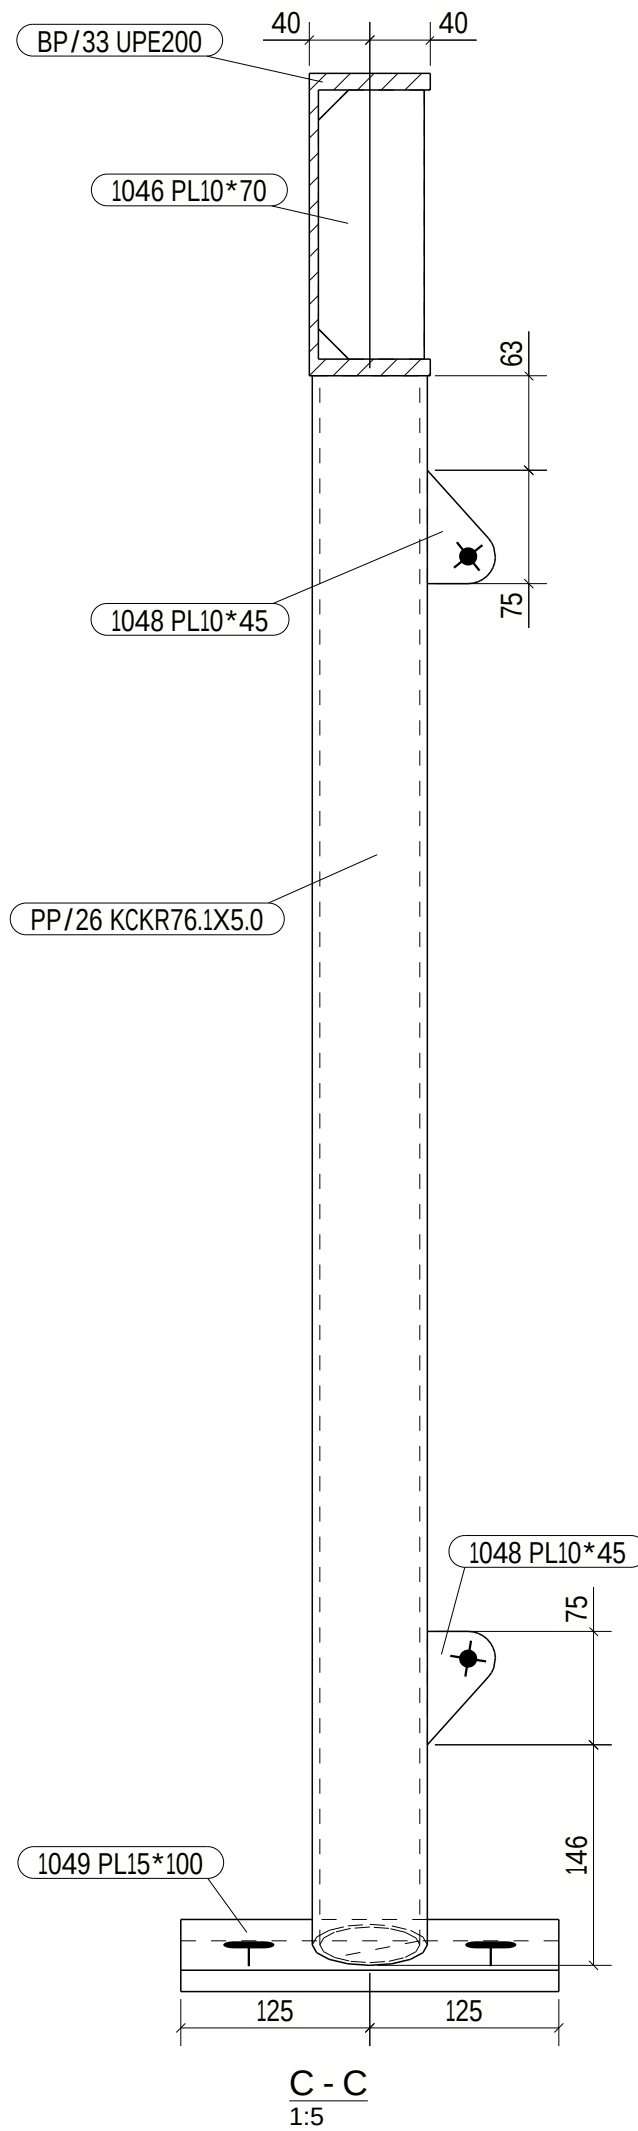

ALLMÄNNA NOTERINGAR:

ALLA HÅL ÄR 22mm OM EJ ANNAT ANGES
ALLA SVETSAR ÄR 6.5mm OM EJ ANNAT ANGES

MATERIALLISTA FÖR ETT GODS MÄRKT: B/27		1 st. TILLVERKAS				
STYCKLIT.	PROFIL	MATERIAL	ANT.	LÄNGD	AREA/st	VIKT/st
BP/33	UPE200	S355J2	1	3650	2.5	83.1
PP/26	KCKR76.1X5.0	S355J2	1	1051	0.3	9.2
1049	PL15*100	S355J2	2	250	0.1	2.9
PP/27	KCKR76.1X5.0	S355J2	1	171	0.0	1.5
1046	PL10*70	S355J2	4	178	0.0	0.9
1047	PL10*70	S355J2	2	178	0.0	0.9
1048	PL10*45	S355J2	2	75	0.0	0.2
TOTALT					3.1	105.7

Norconsult	ANSVARIG PART	PROJEKT	FÖRFRÅGNINGSUNDERLAG		STATUS
	KONTAKTPERSON	CENTRALEKÖB ROBERTSFORS KOMMUN	BYGGHANDLING		HANDLING
	GODKÄND AV	TILLVERKNINGSRITNINGAR STÅL	A2		FORMAT
	SKAPAD AV	2024-12-20	1:15		SKALA
PARTS		B/27			BET