PLACERING I STOMNÄT	
NUMMER	SYSTEMLINJE
B/29	3-4/A-B

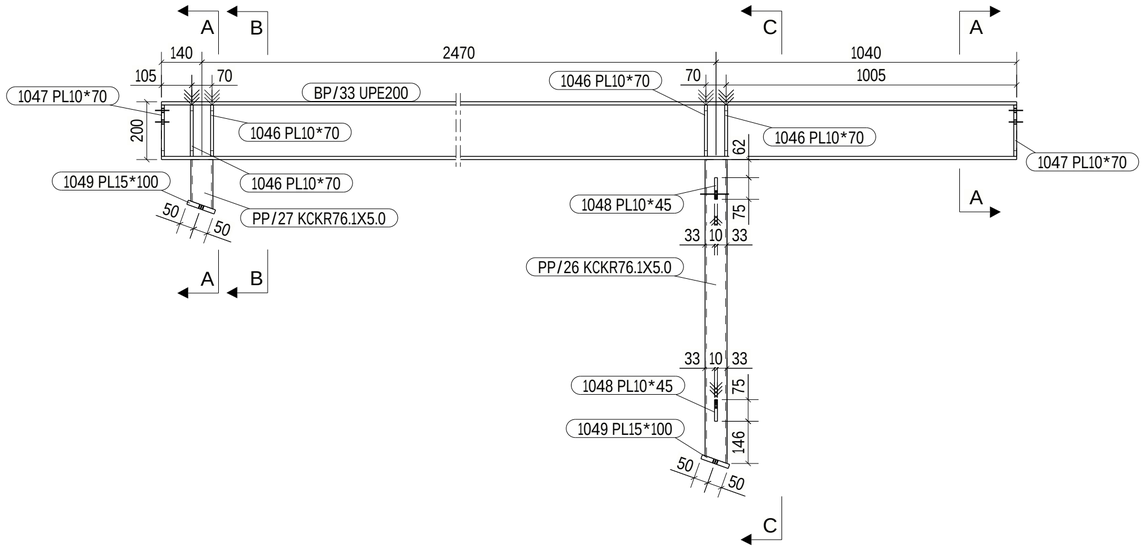

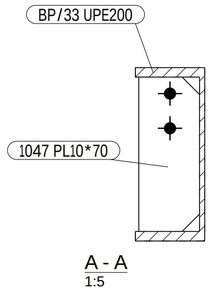

A - A
1:5

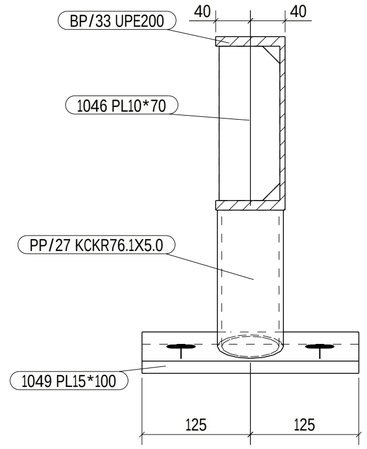

B - B
1:5

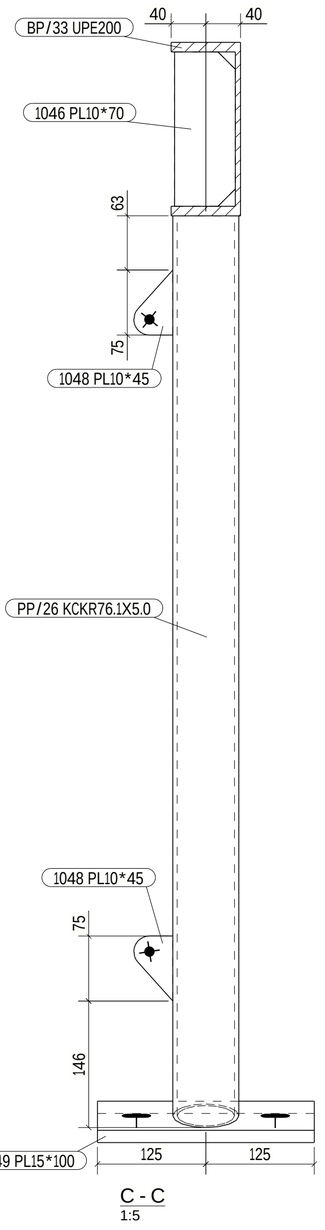

C - C
1:5

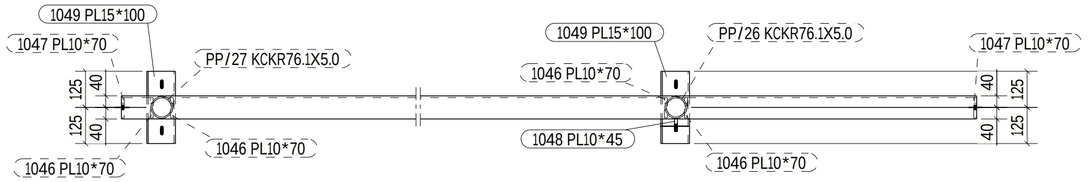

UTVÄNDIGT STÅL VARMFÖRZINKAS ENLIGT ALLMÄNNA FÖRESKRIFTER K-01-0-001 -- 003

ALLMÄNNA NOTERINGAR:
ALLA HÅL ÄR 22 mm OM EJ ANNAT ANGES
ALLA SVETSAR ÄR 6.5 mm OM EJ ANNAT ANGES

MATERIALLISTA FÖR ETT GODS MÄRKT: B/29 — 1 st. TILLVERKAS

STYCKLIT.	PROFIL	MATERIAL	ANT.	LÄNGD	AREA/st	VIKT/st
BP/33	UPE200	S355J2	1	3650	2.5	83.1
PP/26	KCKR76.1X5.0	S355J2	1	1051	0.3	9.2
1049	PL15*100	S355J2	2	250	0.1	2.9
PP/27	KCKR76.1X5.0	S355J2	1	171	0.0	1.5
1046	PL10*70	S355J2	4	178	0.0	0.9
1047	PL10*70	S355J2	2	178	0.0	0.9
1048	PL10*45	S355J2	2	75	0.0	0.2
				TOTALT	3.1	105.7

ANSVARIG PART: Norconsult	PROJEKT: CENTRALKÖK ROBERTSFORS KOMMUN	STATUS: FÖRFRÅGNINGSUNDERLAG	
KONTAKTPERSON: BJÖRN LIDSTRÖM	RITNINGSKATEGORI: TILLVERKNINGSRITNINGAR STÅL	HANDLING: BYGGHANDLING	
GODKÄND AV: BJÖRN LIDSTRÖM	INNEHÅLL: PARTS	ÄNDRING	FORMAT: A2
SKAPAD AV: ARVID WENNBERG		DATUM: 2024-12-20	SKALA: 1:15
		NUMMER: B/29	BET

Tekla Structures