
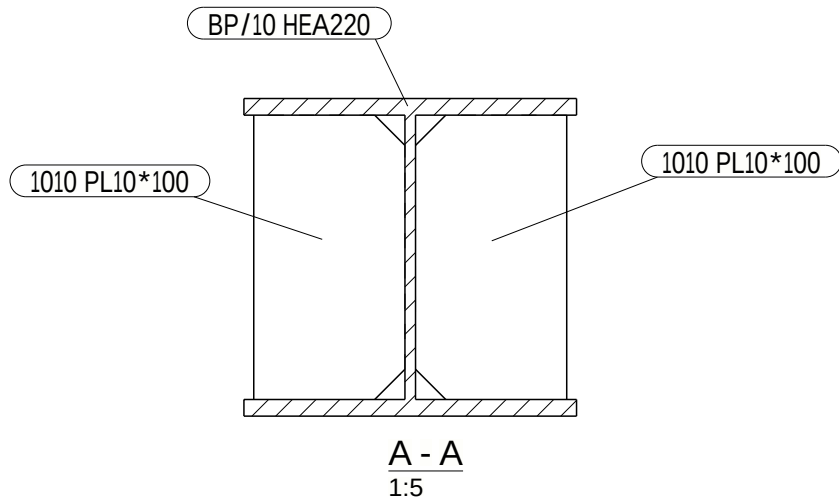


PLACERING I STOMNÄT	
NUMMER	SYSTEMLINJE
B/3	4/A-C

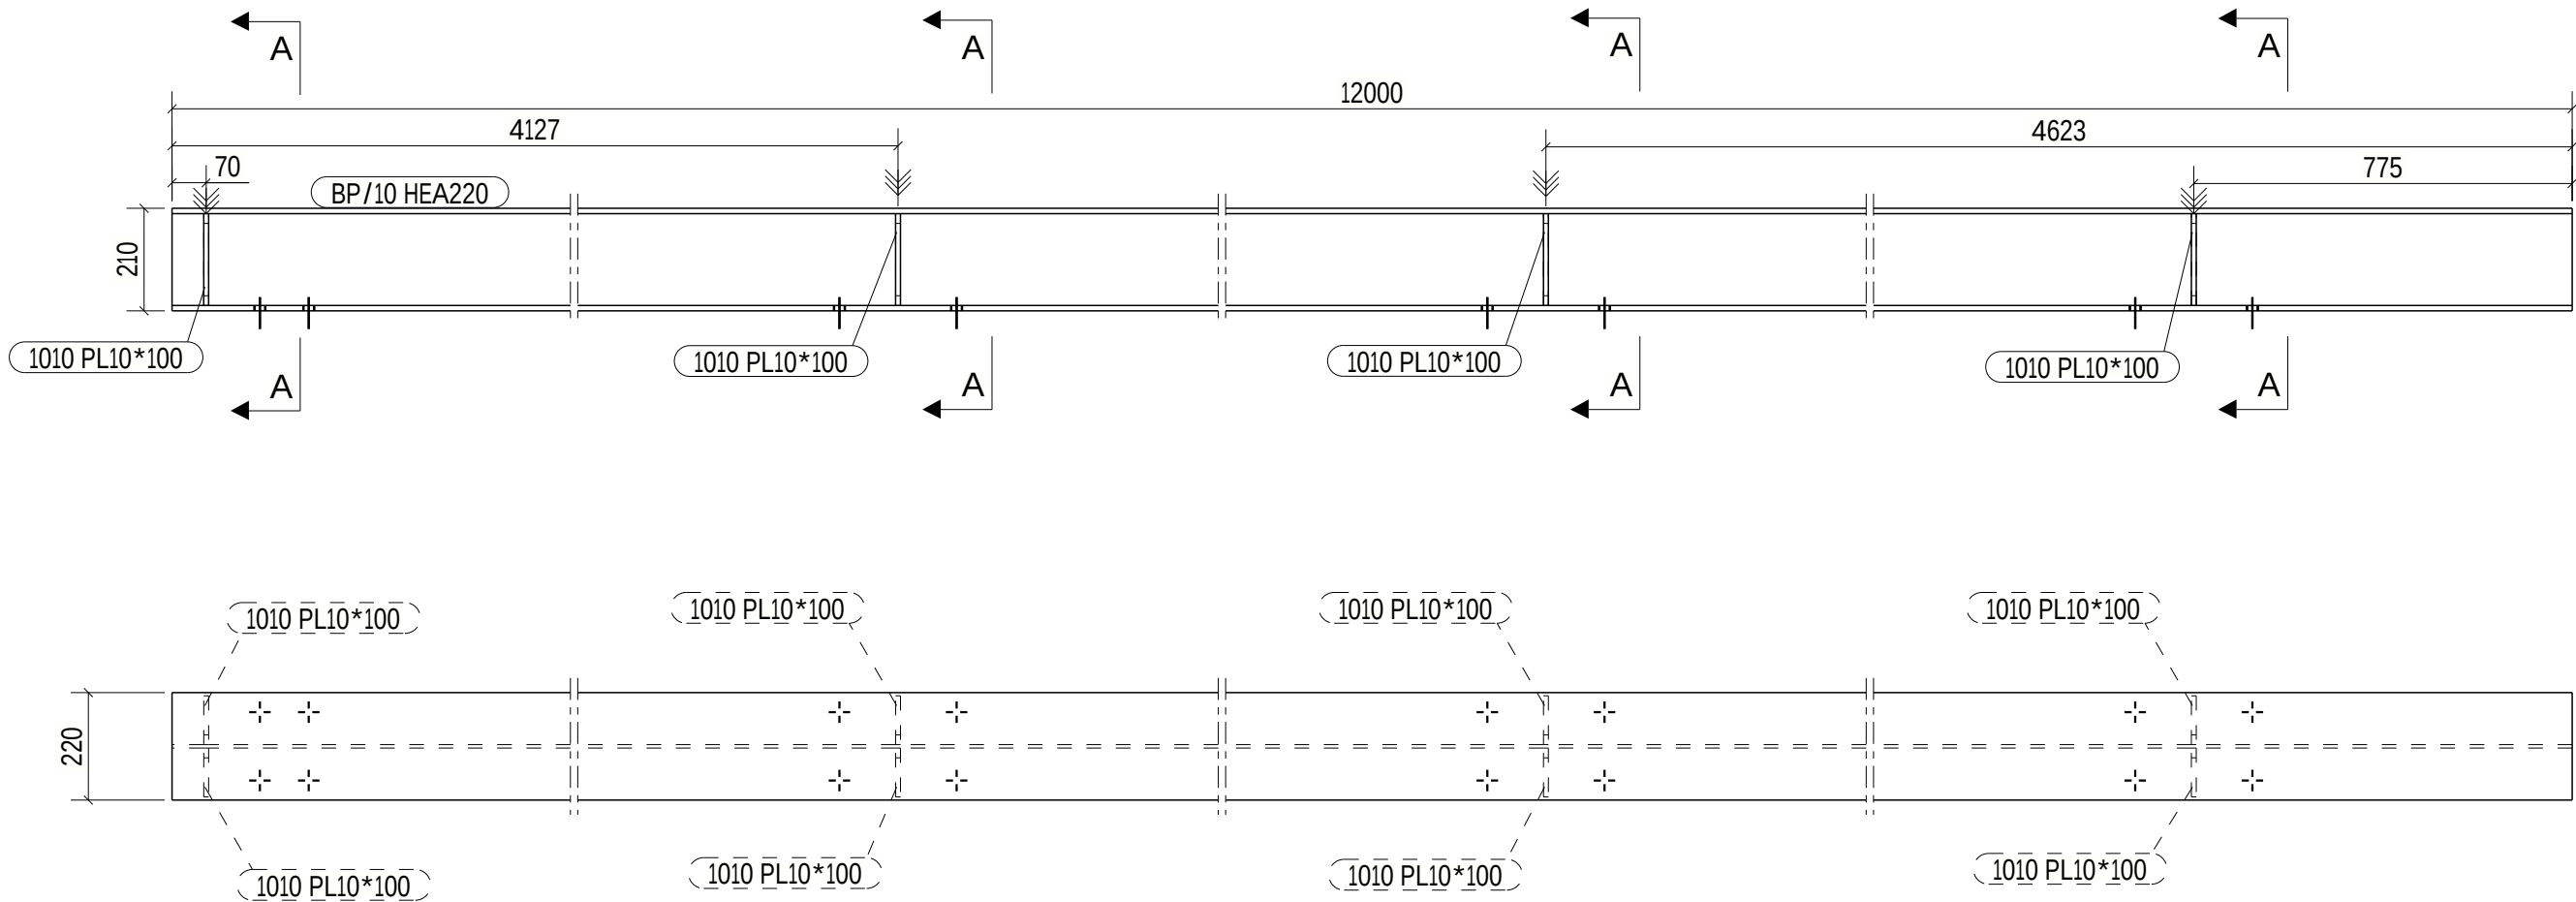

ALLMÄNNA NOTERINGAR: ALLA SVETSAR ÄR KÄLSVETS a5 OM EJ ANNAT ANGES

MATERIELLISTA FÖR ETT GODS MÄRKT: B/3						
1 st. TILLVERKAS						
STYCKLIT.	PROFIL	MATERIAL	ANT.	LÄNGD	AREA/st	VIKT/st
BP/10	HEA220	S355J2	1	12000	15.1	606.1
1010	PL10*100	S355J2	8	188	0.0	1.4
TOTALT					15.4	617.6

Norconsult	ANSVARIG PART	PROJEKT	FÖRFRÅGNINGSUNDERLAG		STATUS
	KONTAKTPERSON	CENTRALEKÖ ROBERTSFORS KOMMUN	BYGGHANDLING		HANDLING
	GODKÄND AV	TILLVERKNINGSRITNINGAR STÅL	ÄNDRING		FORMAT
	SKAPAD AV	2024-12-20	1:15		SKALA
PARTS		NUMMER	B/3	BET	