


| PLACERING I STOMNÄT |             |
|---------------------|-------------|
| NUMMER              | SYSTEMLINJE |
| B/33                | 3-4/A-C     |
| B/33                | 3/A-C       |

UTVÄNDIGT STÅL VARMFÖRZINKAS ENLIGT  
ALLMÄNNA FÖRESKRIFTER K-01-0-001 -- 003

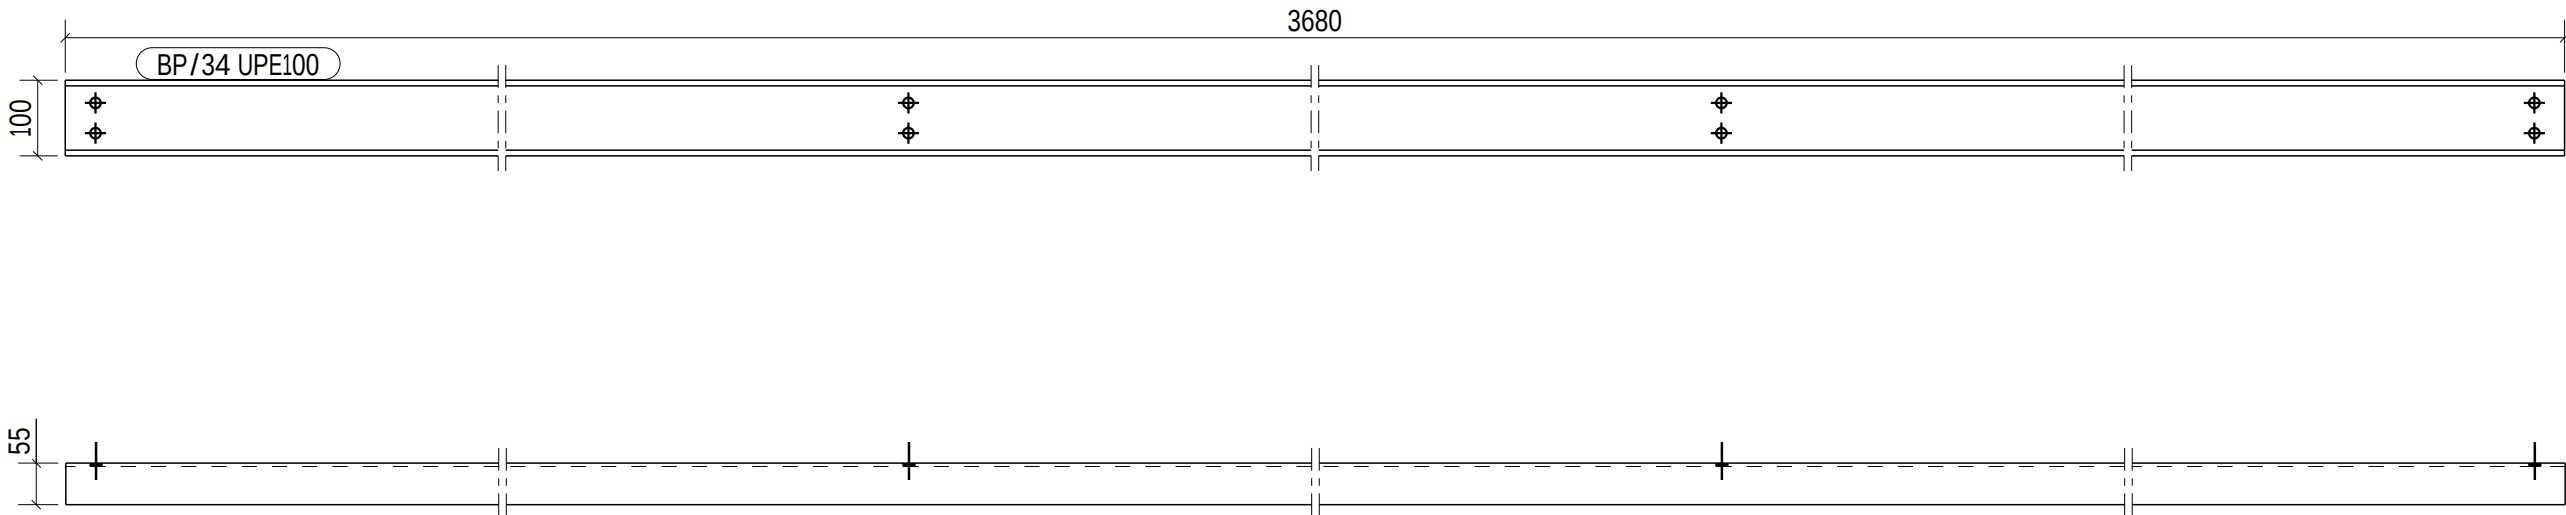

| ALLMÄNNA NOTERINGAR: ALLA SVETSAR ÄR KÄLSVETS a5 OM EJ ANNAT ANGES |        |          |                  |       |         |         |
|--------------------------------------------------------------------|--------|----------|------------------|-------|---------|---------|
| MATERIALLISTA FÖR ETT GODS MÄRKT: B/33                             |        |          | 2 st. TILLVERKAS |       |         |         |
| STYCKLIT.                                                          | PROFIL | MATERIAL | ANT.             | LÄNGD | AREA/st | VIKT/st |
| BP/34                                                              | UPE100 | S355J2   | 1                | 3680  | 1.5     | 36.1    |
| TOTALT                                                             |        |          |                  |       | 1.5     | 36.1    |

|                                                                                 |  |               |                               |  |                      |  |
|---------------------------------------------------------------------------------|--|---------------|-------------------------------|--|----------------------|--|
| Norconsult                                                                      |  | ANSVARIG PART | PROJEKT                       |  | STATUS               |  |
| <div>BJÖRN LIDSTRÖM</div> <div>BJÖRN LIDSTRÖM</div> <div>ARVID WENNERBERG</div> |  |               | CENTRALKÖK ROBERTSFORS KOMMUN |  | FÖRFRÅGNINGSUNDERLAG |  |
|                                                                                 |  |               | TILLVERKNINGSRITNINGAR STÅL   |  | BYGGHANDLING         |  |
|                                                                                 |  |               | PARTS                         |  | A3                   |  |
|                                                                                 |  |               | 2024-12-20                    |  | 1:10                 |  |
|                                                                                 |  |               | INNEHÅLL                      |  | SKALA                |  |
|                                                                                 |  |               | NUMMER                        |  | BET                  |  |
|                                                                                 |  |               | B/33                          |  |                      |  |