

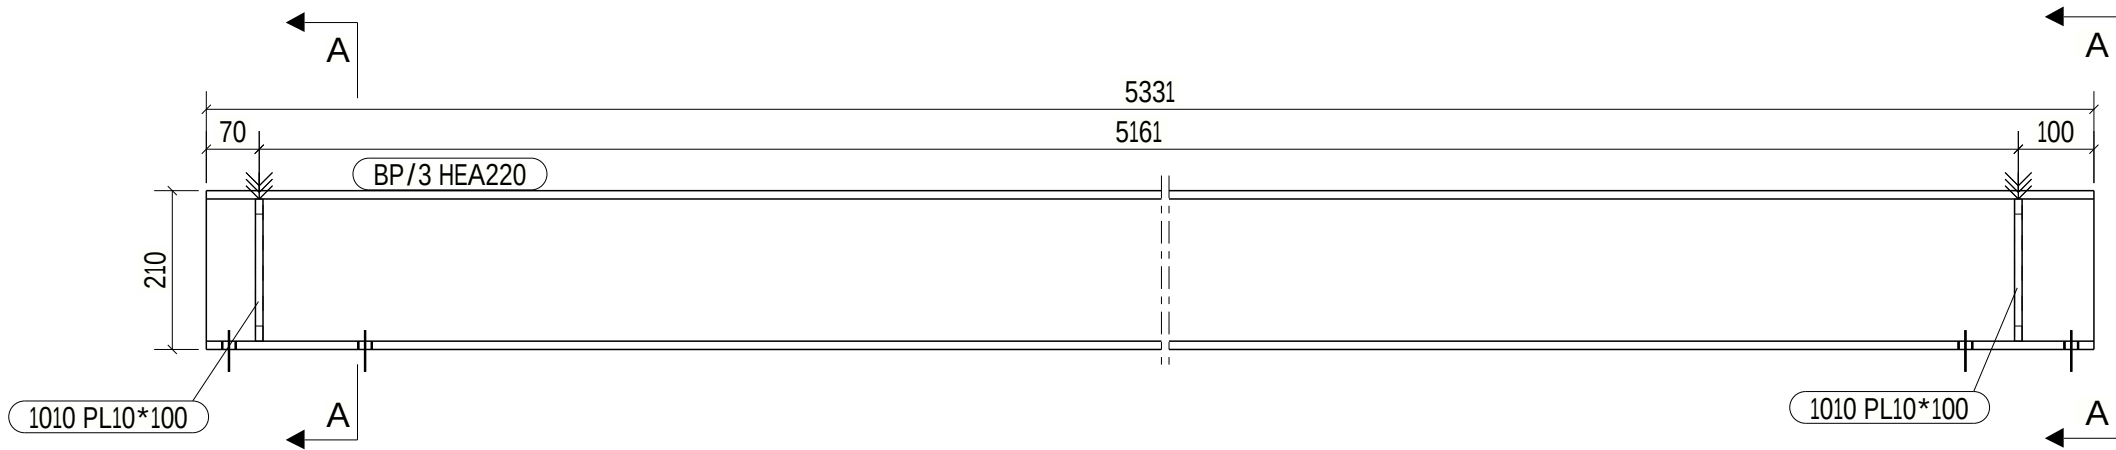


PLACERING I STOMNÄT	
NUMMER	SYSTEMLINJE
B/4	6-7/B-C

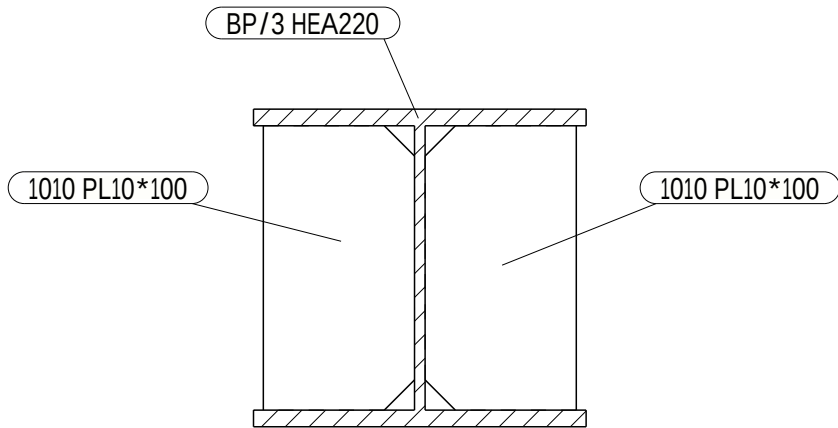

UTVÄNDIGT STÅL VARMFÖRZINKAS ENLIGT
ALLMÄNNA FÖRESKRIFTER K-01-0-001 -- 003

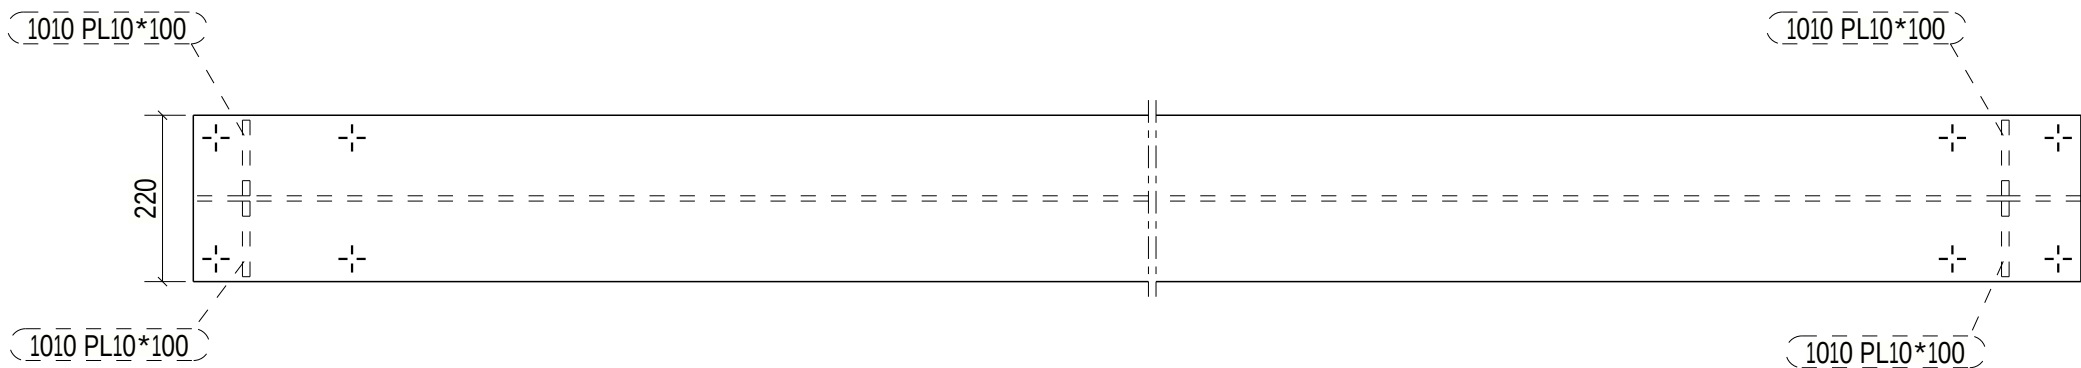

A - A
1:5

ALLMÄNNA NOTERINGAR: ALLA SVETSAR ÄR KÄLSVETS a5 OM EJ ANNAT ANGES

MATERIALLISTA FÖR ETT GODS MÄRKT: B/4 1 st. TILLVERKAS						
STYCKLIT.	PROFIL	MATERIAL	ANT.	LÄNGD	AREA/st	VIKT/st
BP/3	HEA220	S355J2	1	5331	6.7	269.3
1010	PL10*100	S355J2	4	188	0.0	1.4
TOTALT					6.9	275.0

Norconsult	ANSVARIG PART	PROJEKT	FÖRFRÅGNINGSUNDERLAG		STATUS
	KONTAKTPERSON	CENTRALKÖK ROBERTSFORS KOMMUN	BYGGHANDLING		HANDLING
	GODKÄND AV	TILLVERKNINGSRITNINGAR STÅL	ÄNDRING		FORMAT
	SKAPAD AV	INNEHÅLL	2024-12-20	DATUM	A3
PARTS			1:5	SKALA	BET
			B/4	NUMMER	