
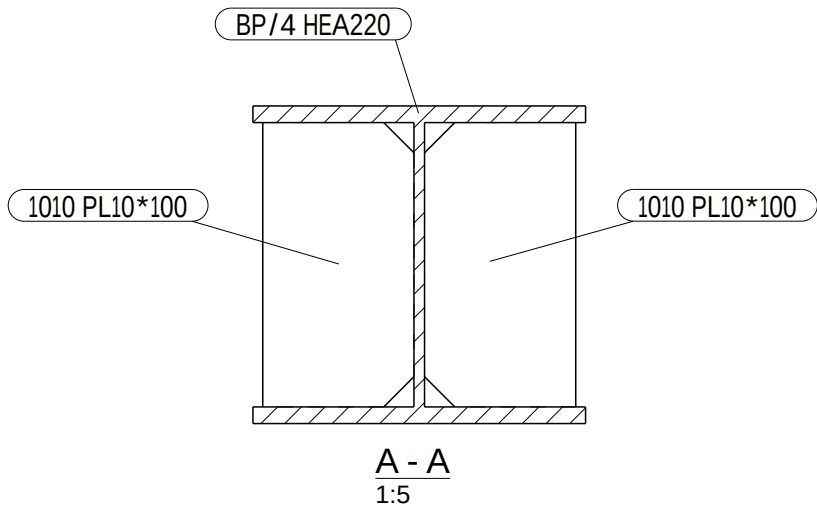


PLACERING I STOMNÄT	
NUMMER	SYSTEMLINJE
B/5	6-7/C-D

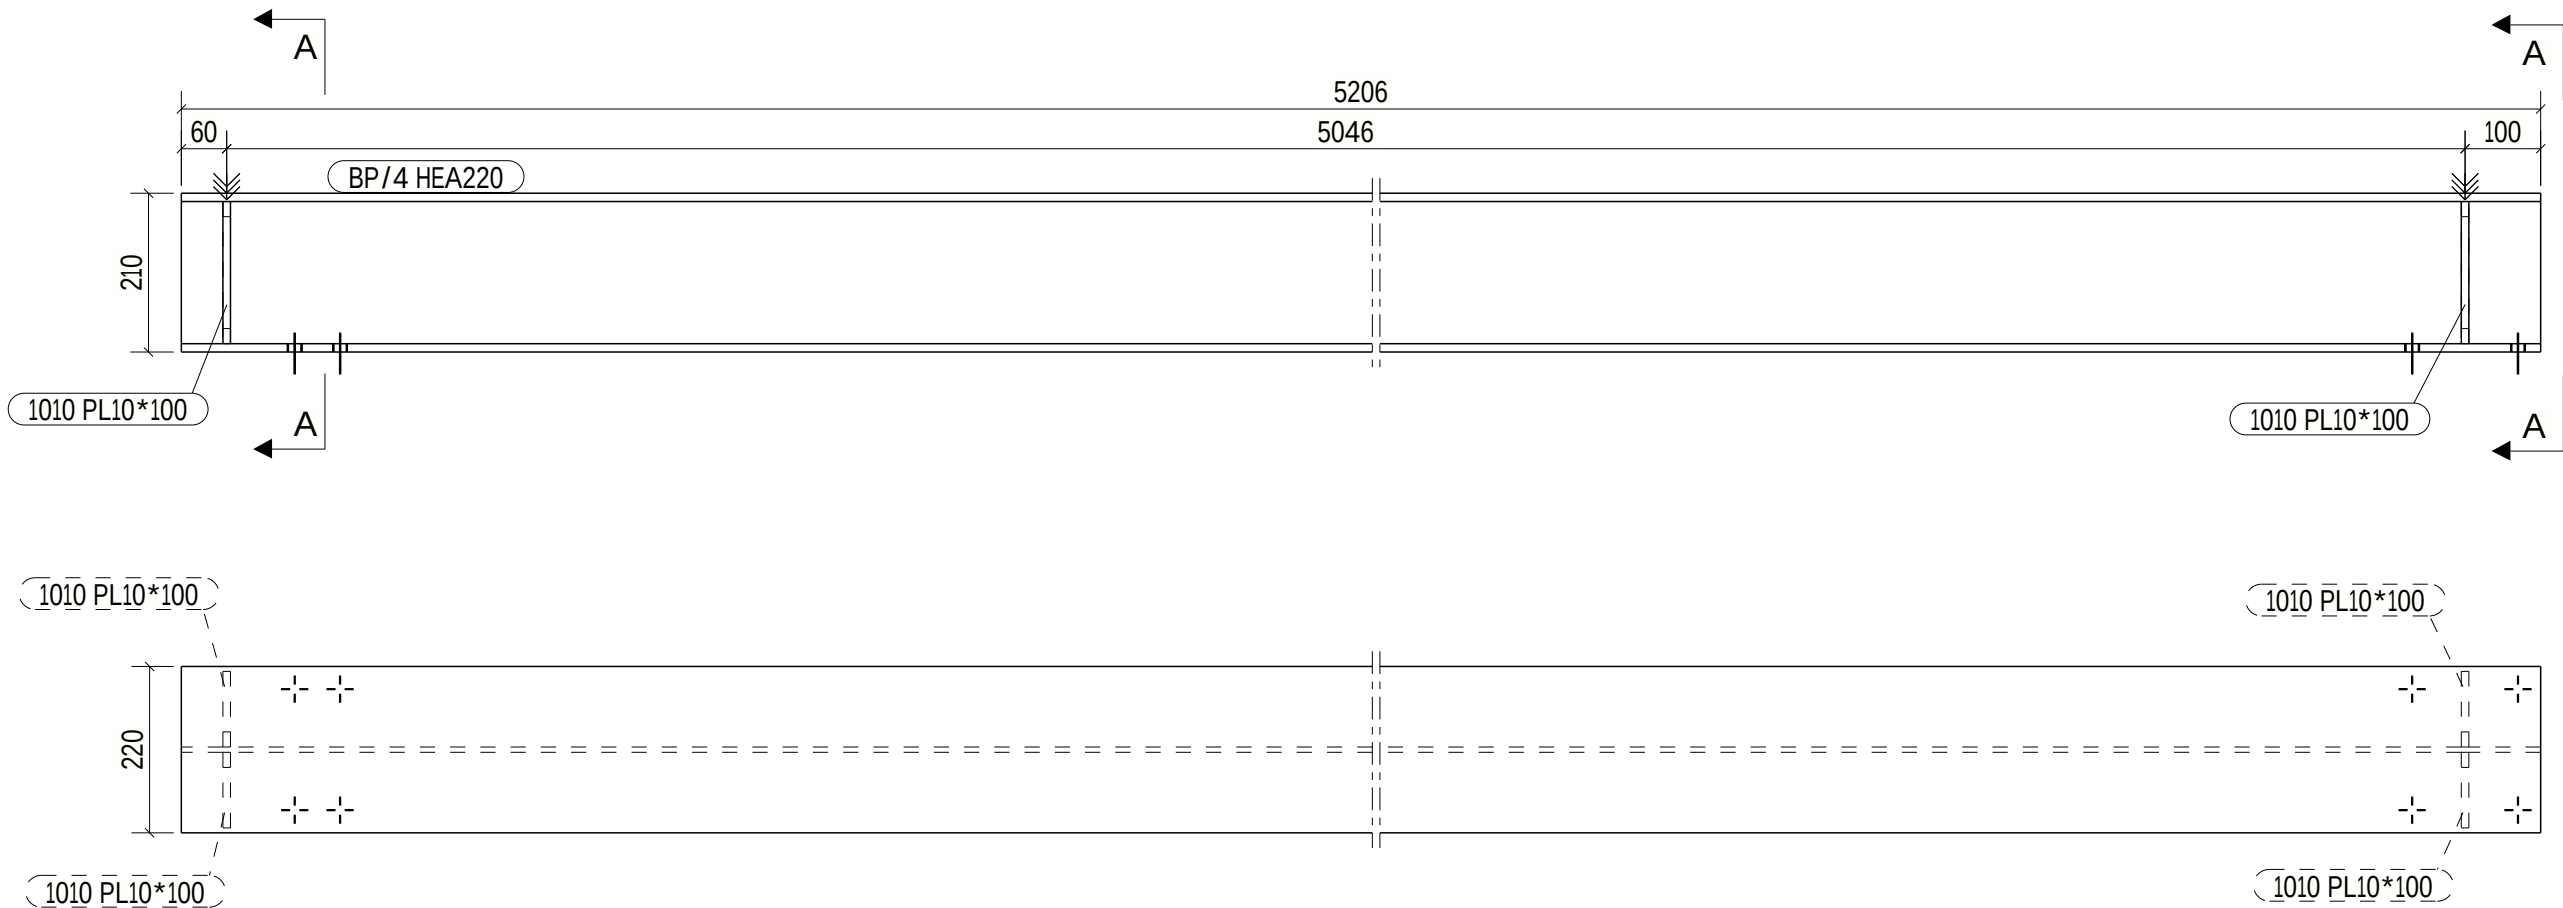

ALLMÄNNA NOTERINGAR: ALLA SVETSAR ÄR KÄLSVETS a5 OM EJ ANNAT ANGES

MATERIALLISTA FÖR ETT GODS MÄRKT: B/5 1 st. TILLVERKAS						
STYCKLIT.	PROFIL	MATERIAL	ANT.	LÄNGD	AREA/st	VIKT/st
BP/4	HEA220	S355J2	1	5206	6.5	262.9
1010	PL10*100	S355J2	4	188	0.0	1.4
TOTALT					6.7	268.7

Norconsult	ANSVARIG PART	PROJEKT	FÖRFRÅGNINGSUNDERLAG		STATUS
	KONTAKTPERSON	CENTRALKÖK ROBERTSFORS KOMMUN	BYGGHANDLING		HANDLING
	GODKÄND AV	TILLVERKNINGSRITNINGAR STÅL	ÄNDRING	FORMAT	A3
	SKAPAD AV	INNEHÅLL	2024-12-20	DATUM	1:5
PARTS			NUMMER	BET	B/5