
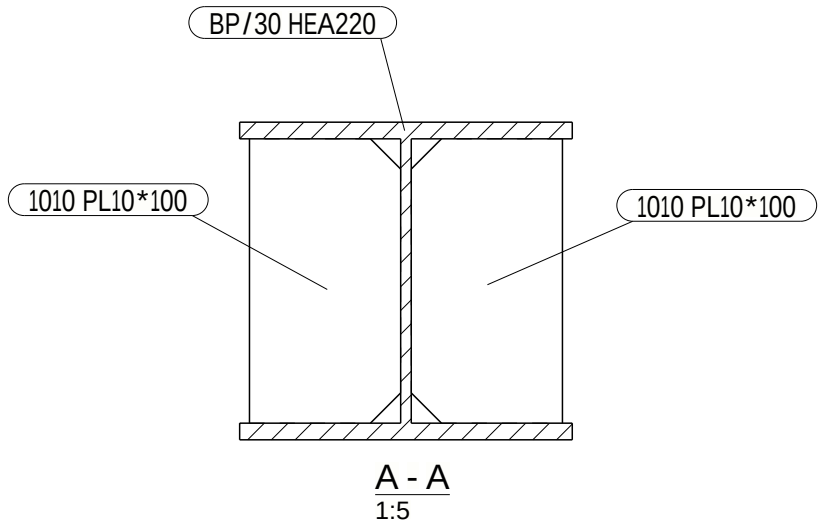
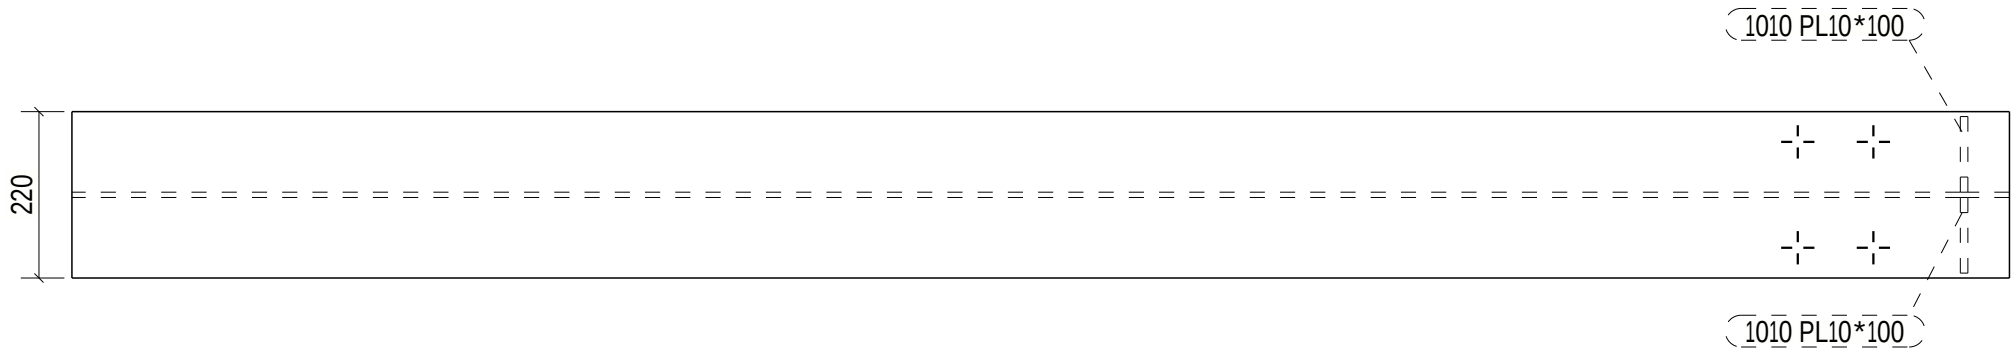


PLACERING I STOMNÄT	
NUMMER	SYSTEMLINJE
B/6	4/B-C

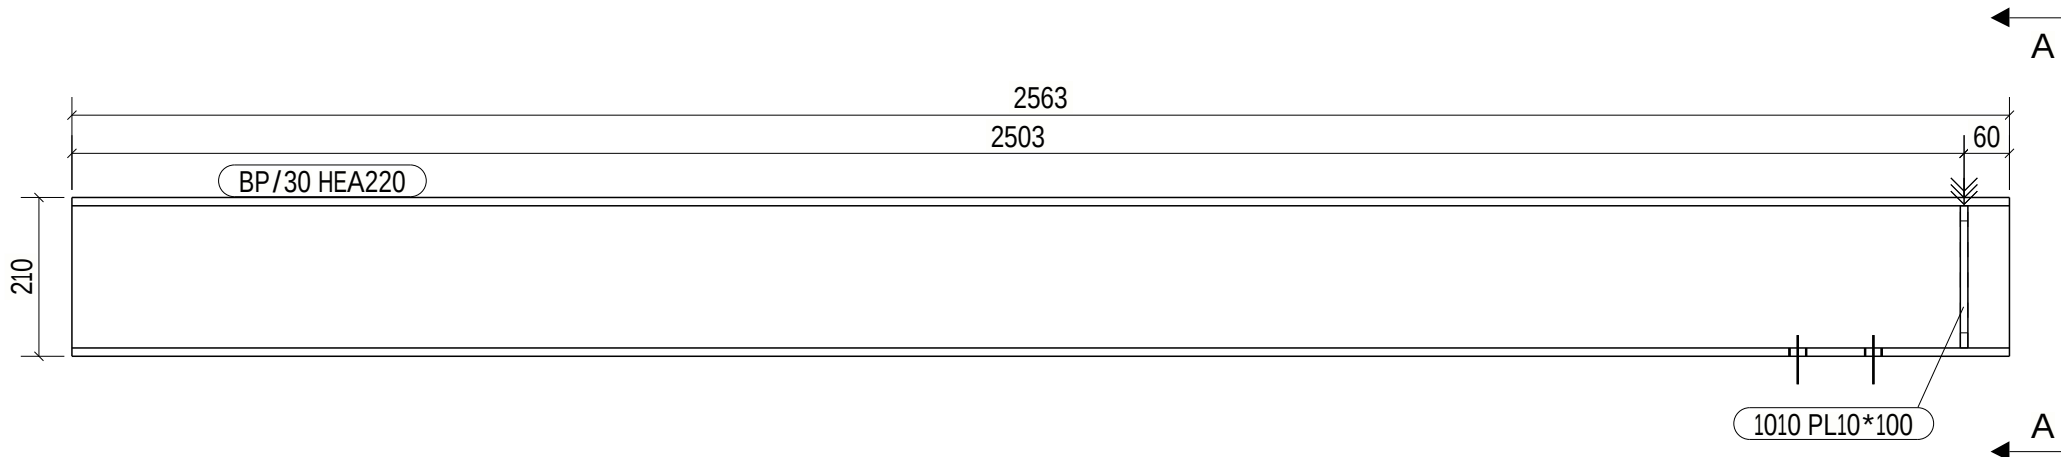

ALLMÄNNA NOTERINGAR: ALLA SVETSAR ÄR KÄLSVETS a5 OM EJ ANNAT ANGES

MATERIALLISTA FÖR ETT GODS MÄRKT:		B/6					1 st. TILLVERKAS
STYCKLIT.	PROFIL	MATERIAL	ANT.	LÄNGD	AREA/st	VIKT/st	
BP/30	HEA220	S355J2	1	2563	3.2	129.5	
1010	PL10*100	S355J2	2	188	0.0	1.4	
TOTALT					3.3	132.3	

Norconsult 	ANSVARIG PART	PROJEKT	FÖRFRÅGNINGSUNDERLAG		STATUS
	KONTAKTPERSON	CENTRALKÖK ROBERTSFORS KOMMUN	BYGGHANDLING		HANDLING
	GODKÄND AV	TILLVERKNINGSRITNINGAR STÅL	ÄNDRING		FORMAT
	SKAPAD AV	INNEHÅLL	2024-12-20	DATUM	A3
PARTS			1:5	SKALA	BET
			B/6	NUMMER	