

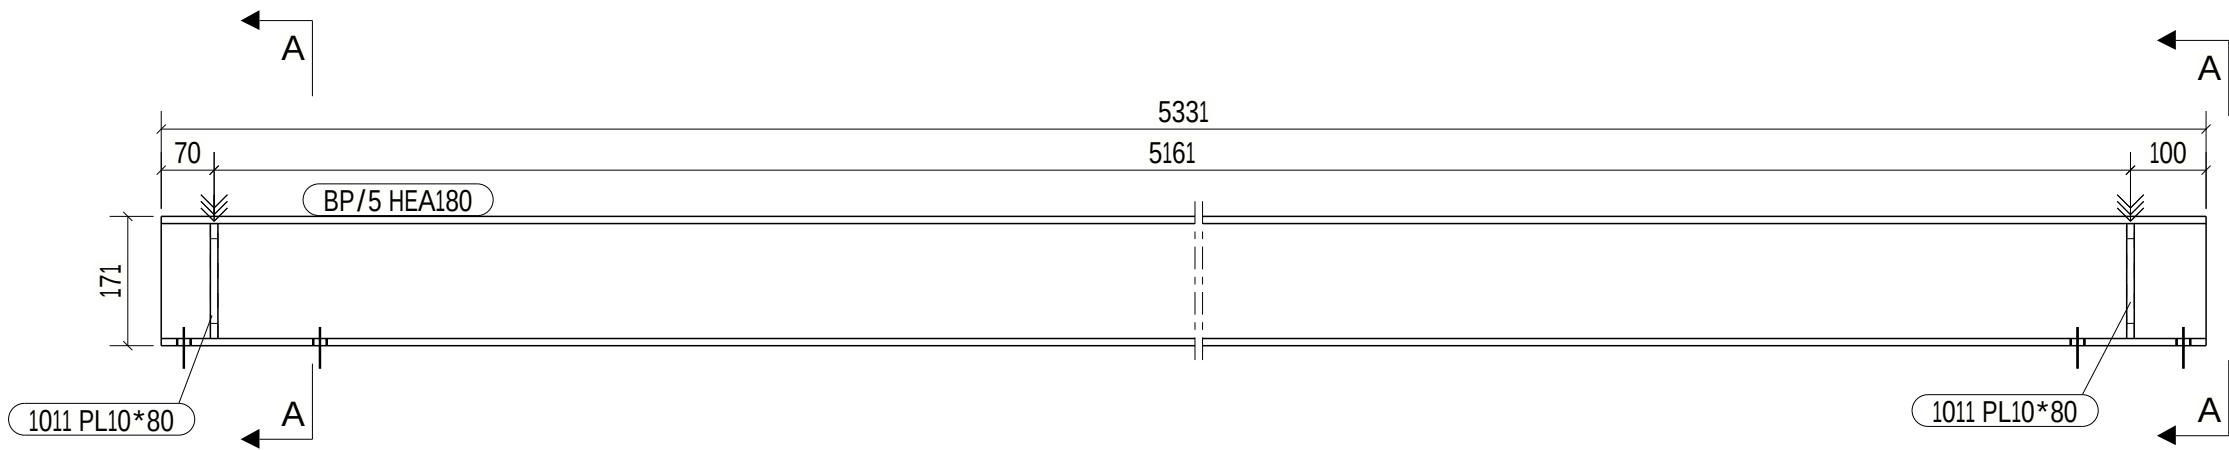


PLACERING I STOMNÄT	
NUMMER	SYSTEMLINJE
B/7	6-7/D-E

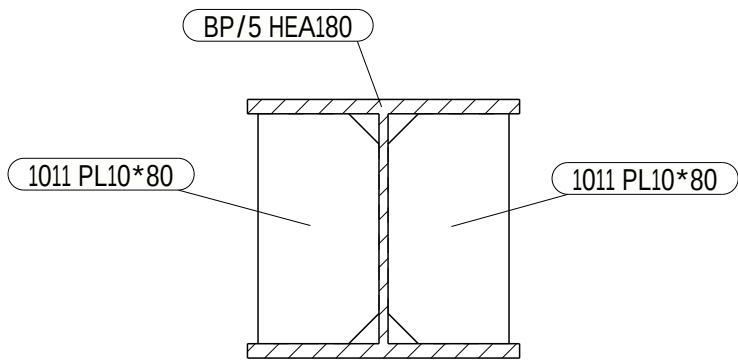

UTVÄNDIGT STÅL VARMFÖRZINKAS ENLIGT
ALLMÄNNA FÖRESKRIFTER K-01-0-001 -- 003

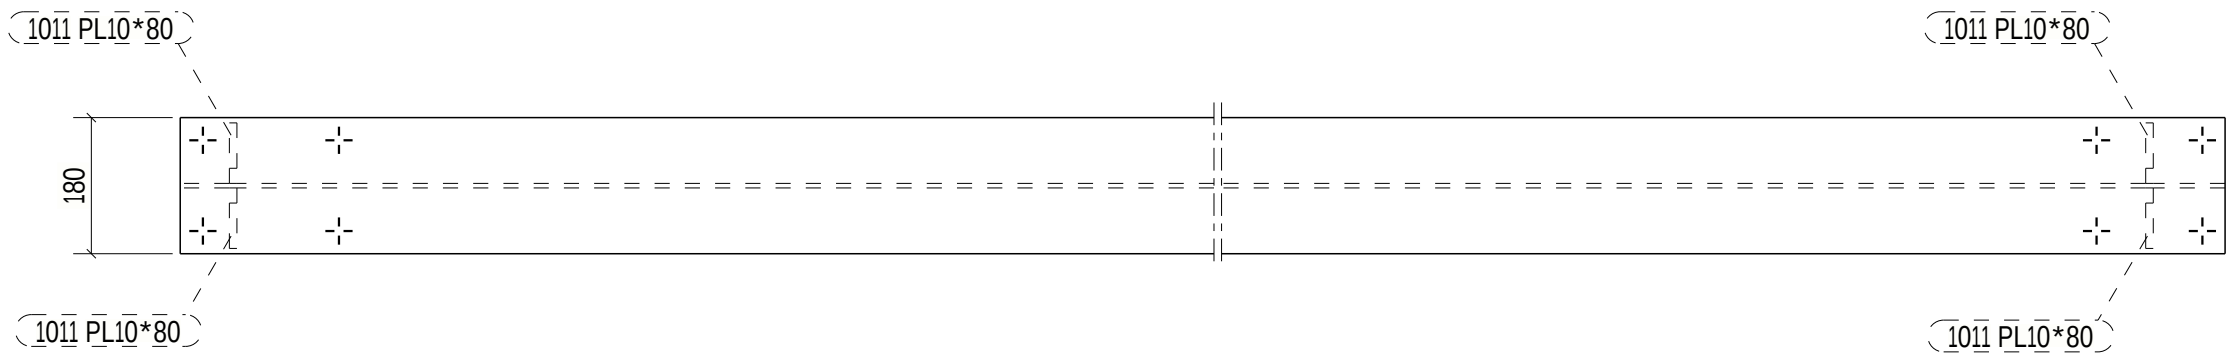

A - A
1:5

ALLMÄNNA NOTERINGAR: ALLA SVETSAR ÄR KÄLSVETS a5 OM EJ ANNAT ANGES

MATERIALLISTA FÖR ETT GODS MÄRKT: B/7							1 st. TILLVERKAS
STYCKLIT.	PROFIL	MATERIAL	ANT.	LÄNGD	AREA/st	VIKT/st	
BP/5	HEA180	S355J2	1	5331	5.5	189.4	
1011	PL10*80	S355J2	4	152	0.0	0.9	
TOTALT					5.6	193.1	

Norconsult 	ANSVARIG PART	PROJEKT	FÖRFRÅGNINGSUNDERLAG		STATUS
	KONTAKTPERSON	CENTRALEKÖ ROBERTSFORS KOMMUN	BYGGHANDLING		HANDLING
	GODKÄND AV	TILLVERKNINGSRITNINGAR STÅL	ÄNDRING		FORMAT
	SKAPAD AV	INNEHÅLL	2024-12-20	DATUM	A3
PARTS			NUMMER	BET	SKALA
			B/7		1:5