


ANTAL	MONTAGEDEL
2	B/30

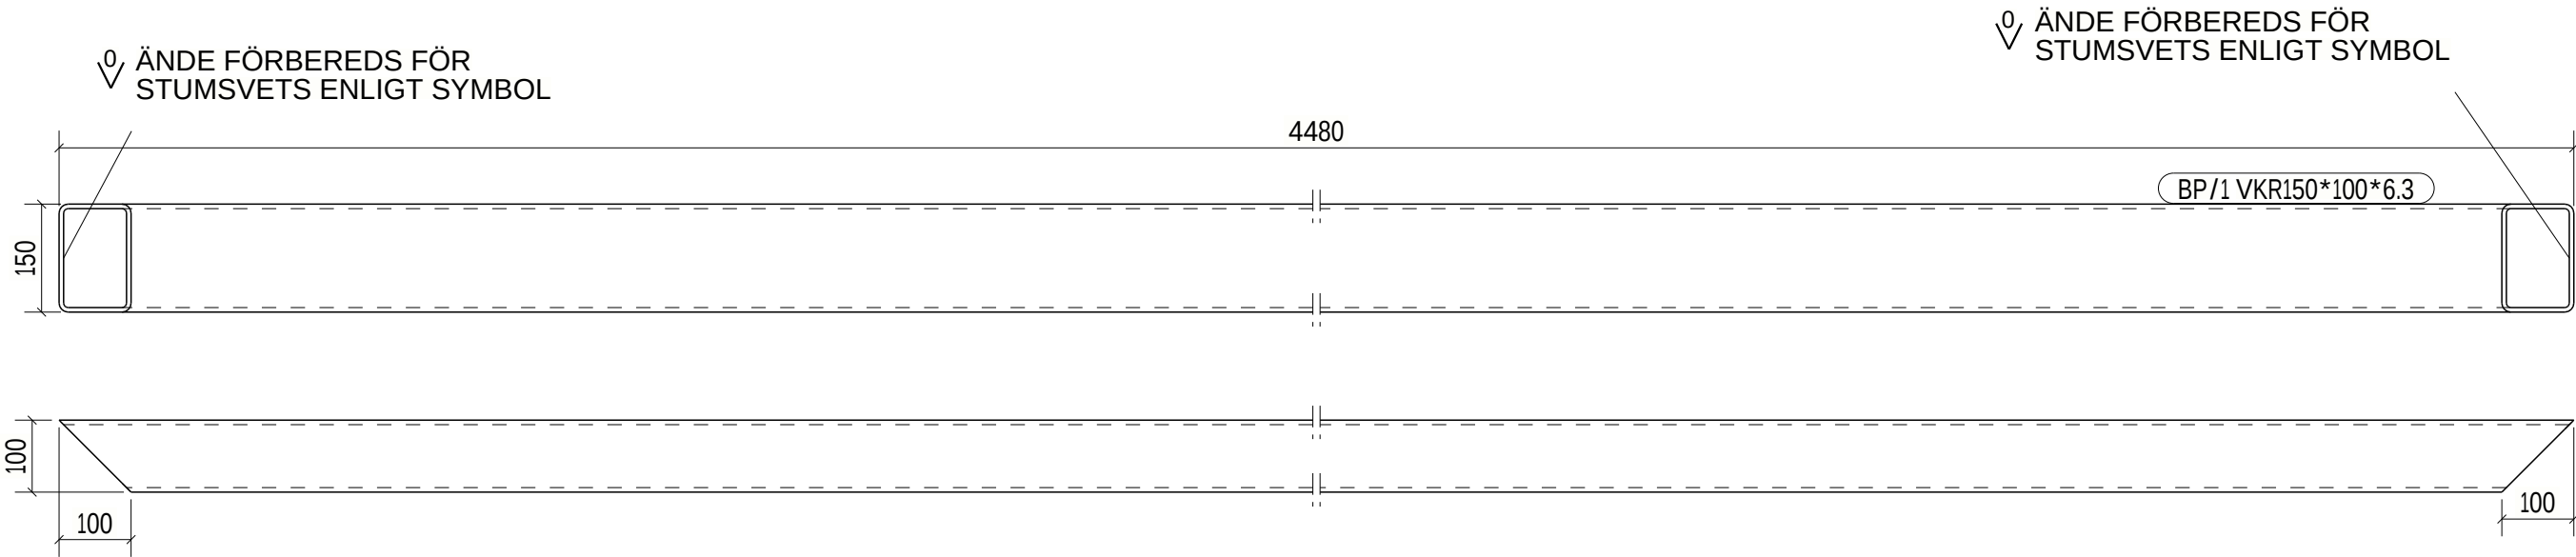

BP/1	VKR150*100*6.3	S355J2H	2	4480.0	2.15	103.7
MÄRKE	PROFIL	MATERIAL	ANTAL	LÄNGD	AREA	VIKT
MATERIALLISTA				TOTALT	4.30	207.5

Norconsult		ANSVARIG PART	CENTRALKÖK ROBERTSFORS KOMMUN		PROJEKT	FÖRFRÅGNINGSUNDERLAG		STATUS	
BJÖRN LIDSTRÖM		KONTAKTPERSON	TILLVERKNINGSRITNINGAR STÅL		RITNINGSKATEGORI	BYGGHANDLING		HANDLING	
BJÖRN LIDSTRÖM		GODKÄND AV	PARTS		INNEHÅLL	ÄNDRING	A3	FORMAT	
ARVID WENNERBERG		SKAPAD AV				2024-12-20	DATUM	1:10	SKALA
						BP/1	NUMMER		BET