


ANTAL	MONTAGEDEL
1	B/20

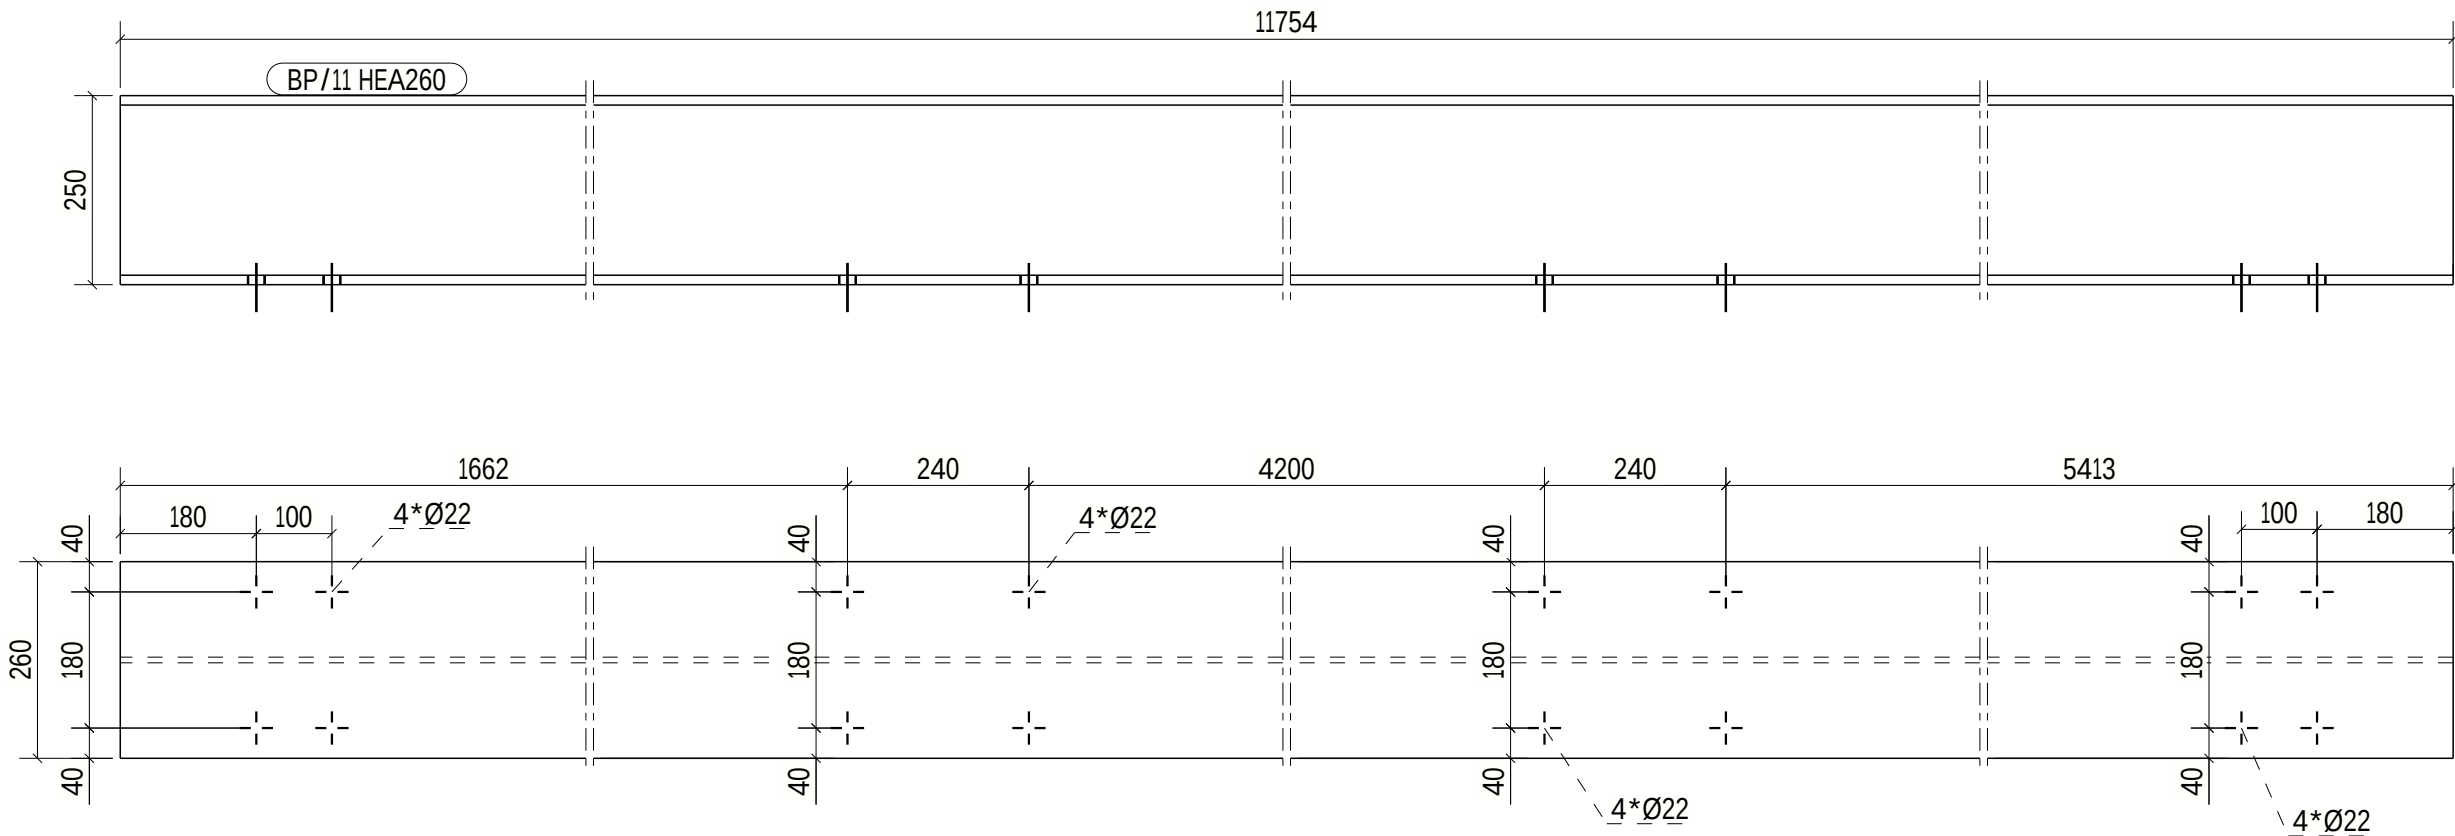

BP/11	HEA260	S355J2	1	11754.5	17.44	801.1
MÄRKE	PROFIL	MATERIAL	ANTAL	LÄNGD	AREA	VIKT
MATERIALLISTA				TOTALT	17.44	801.1

Norconsult ANSVARIG PART BJÖRN LIDSTRÖM GODKÄND AV ARVID WENNERBERG SKAPAD AV	CENTRALKÖK ROBERTSFORS KOMMUN		FÖRFRÅGNINGSUNDERLAG	
	TILLVERKNINGSRITNINGAR STÅL		BYGGHANDLING	
	PARTS		2024-12-20	A3
			BP/11	1:10