


ANTAL	MONTAGEDEL
1	B/23

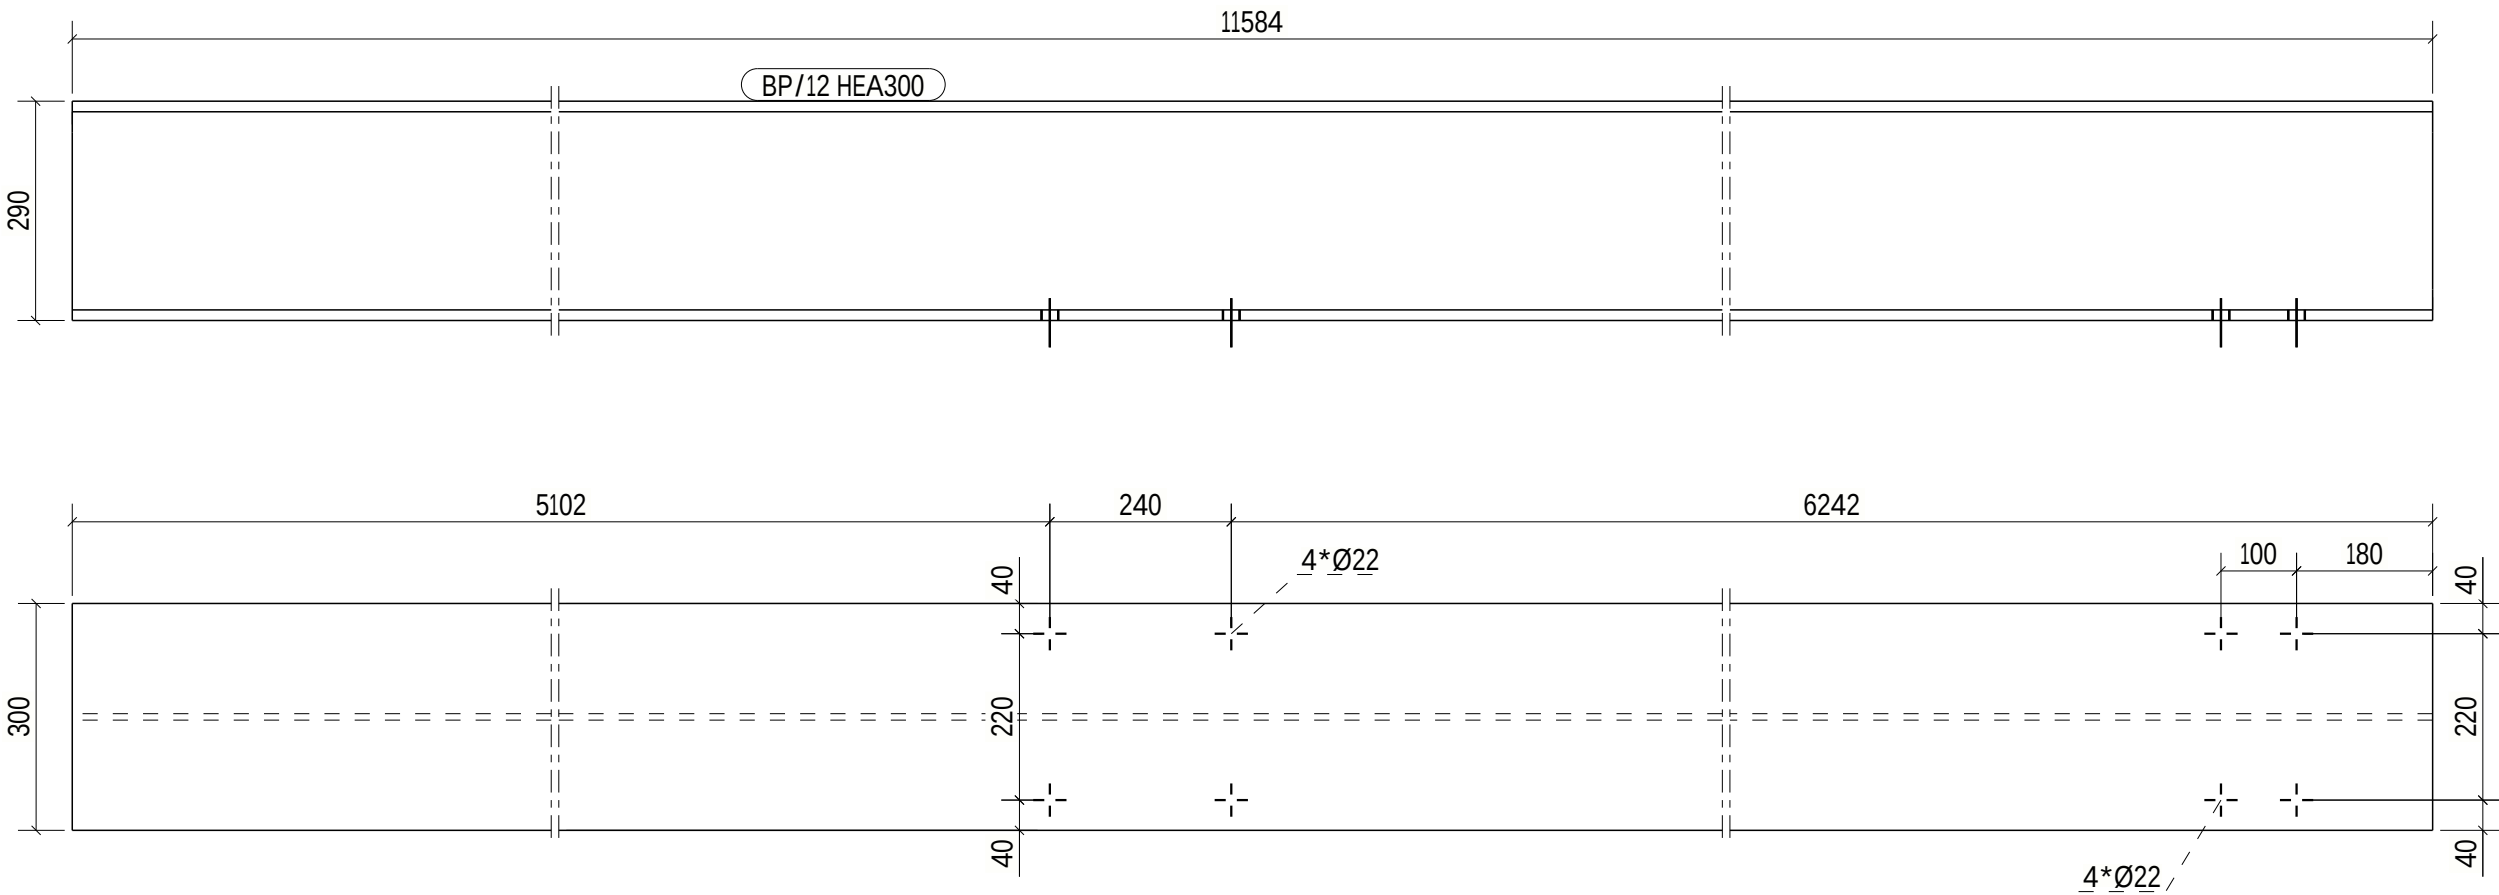

BP/12	HEA300	S355J2	1	11584.5	19.89	1023.1
MÄRKE	PROFIL	MATERIAL	ANTAL	LÄNGD	AREA	VIKT
MATERIALLISTA				TOTALT	19.89	1023.1

Norconsult 		ANSVARIG PART	PROJEKT		FÖRFRÅGNINGSUNDERLAG		STATUS
CENTRALEKÖK ROBERTSFORS KOMMUN			BYGGHANDLING				HANDLING
BJÖRN LIDSTRÖM		KONTAKTPERSON	RITNINGSKATEGORI		ÄNDRING		FORMAT
BJÖRN LIDSTRÖM		GODKÄND AV	TILLVERKNINGSRITNINGAR STÅL		A3		
ARVID WENNERBERG		SKAPAD AV	INNEHÅLL		2024-12-20		DATUM
PARTS					1:10		SKALA
					BP/12		NUMMER
							BET