


ANTAL	MONTAGEDEL
1	B/24

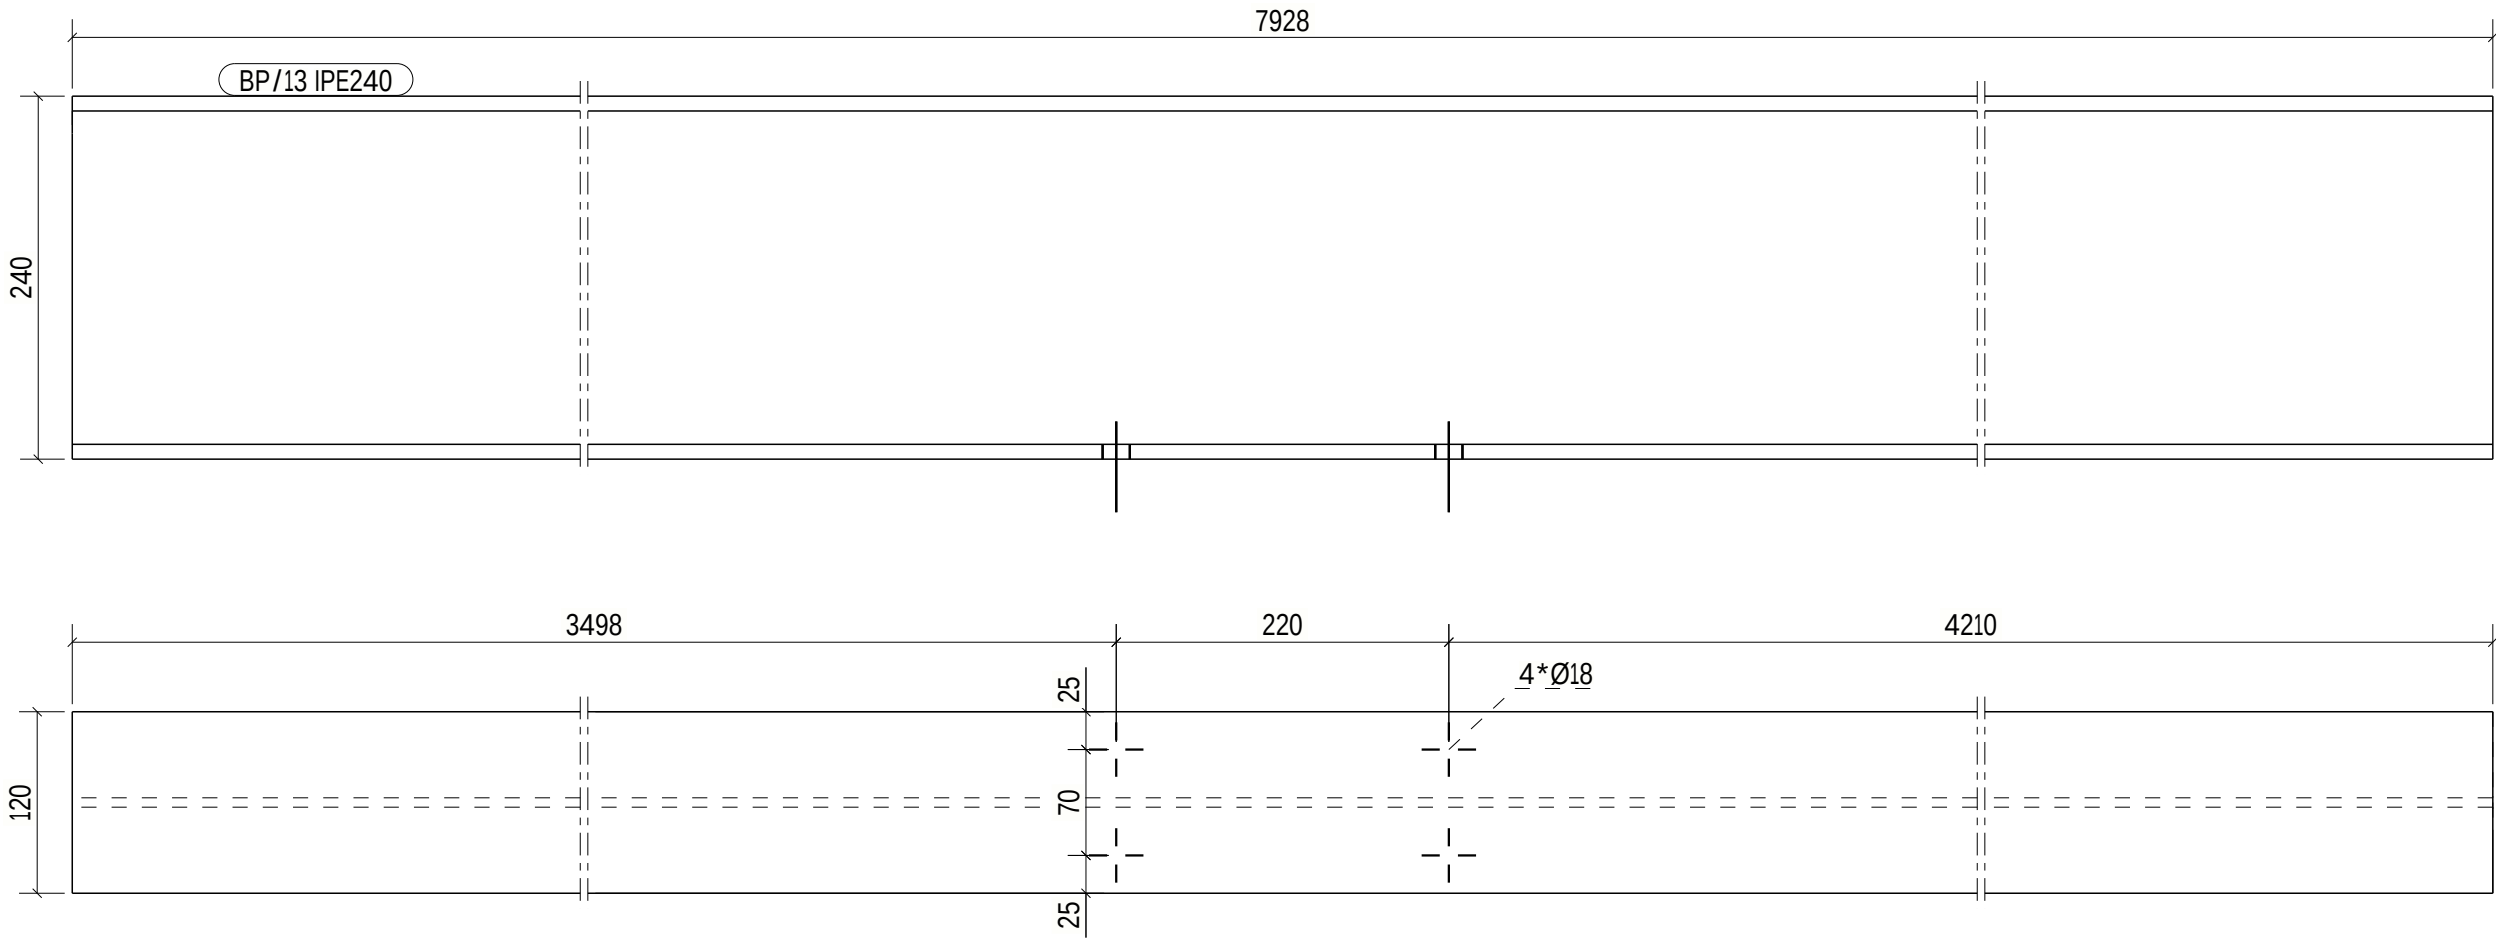

BP/13	IPE240	S355J2	1	7928.0	7.31	243.3
MÄRKE	PROFIL	MATERIAL	ANTAL	LÄNGD	AREA	VIKT
MATERIALLISTA				TOTALT	7.31	243.3

Norconsult	ANSVARIG PART	PROJEKT	FÖRFRÅGNINGSUNDERLAG		STATUS
	KONTAKTPERSON	CENTRALEKÖK ROBERTSFORS KOMMUN	BYGGHANDLING		HANDLING
	GODKÄND AV	TILLVERKNINGSRITNINGAR STÅL	ÄNDRING		FORMAT
ARVID WENNERBERG		SKAPAD AV	INNEHÅLL		SKALA
		PARTS	2024-12-20	DATUM	1:5
			NUMMER	BET	
			BP/13		