


ANTAL	MONTAGEDEL
1	B/8

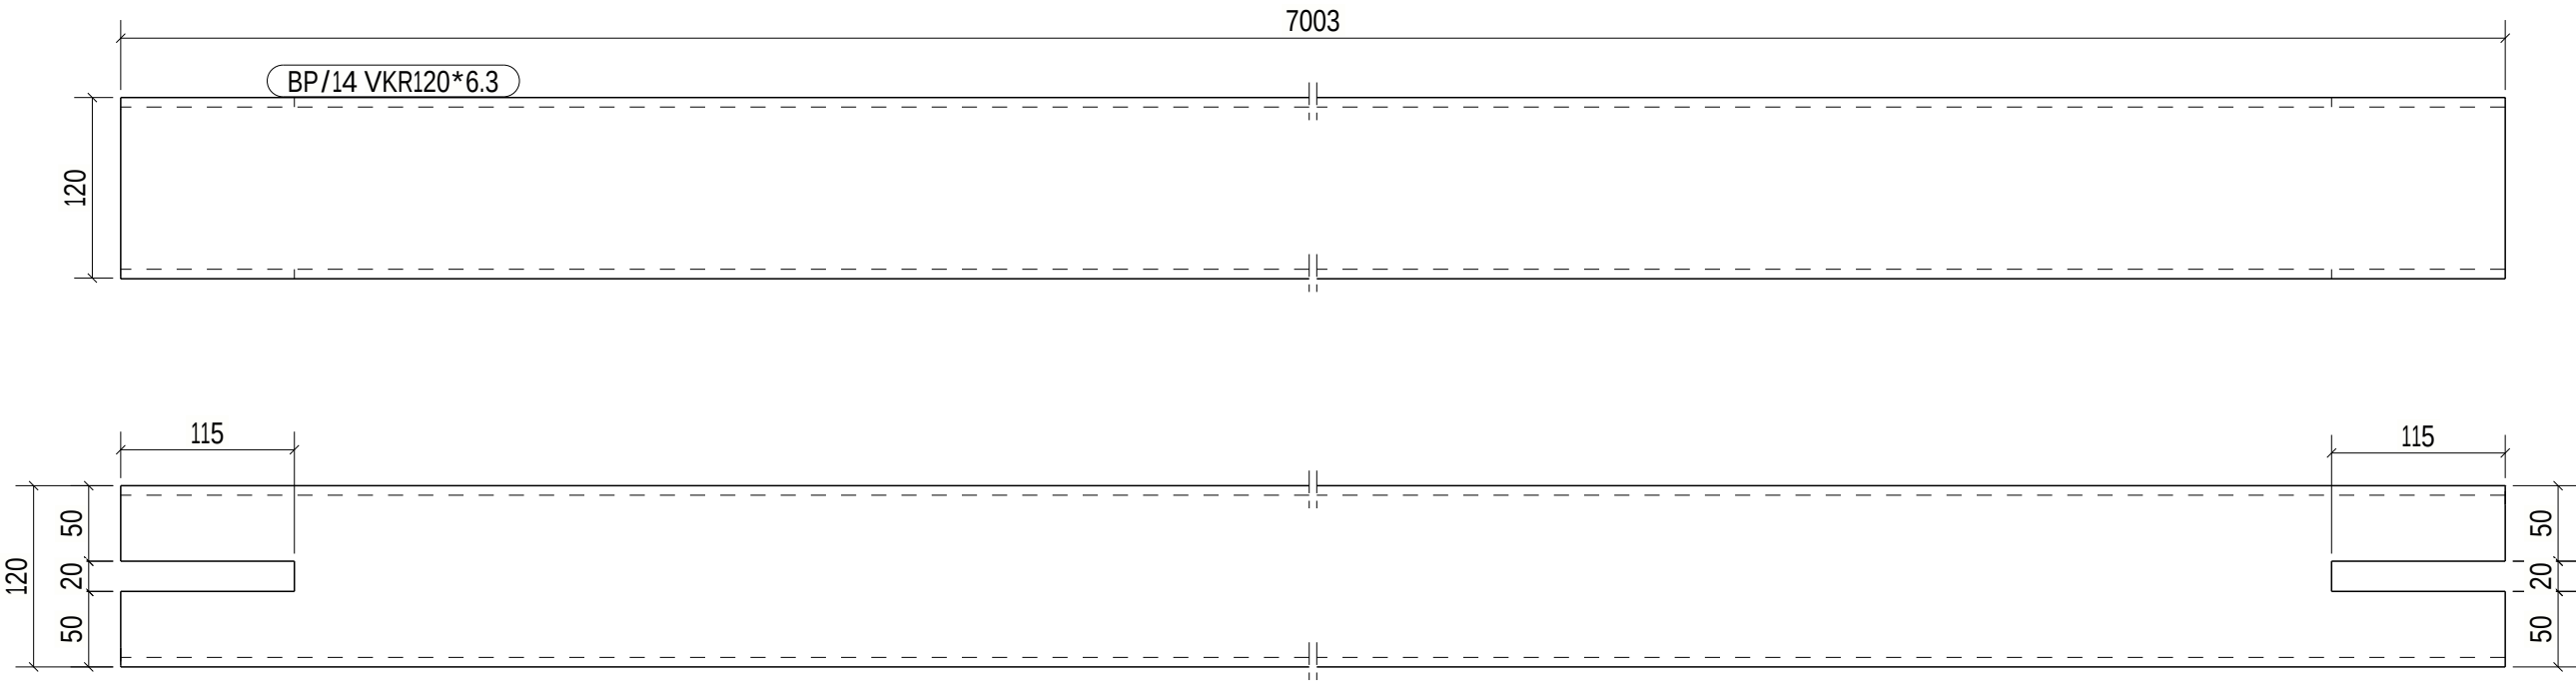

BP/14	VKR120*6.3	S355J2H	1	7003.0	3.22	155.0
MÄRKE	PROFIL	MATERIAL	ANTAL	LÄNGD	AREA	VIKT
MATERIALLISTA				TOTALT	3.22	155.0

Norconsult		ANSVARIG PART	PROJEKT	FÖRFRÅGNINGSUNDERLAG		STATUS
BJÖRN LIDSTRÖM		KONTAKTPERSON	CENTRALEKÖK ROBERTSFORS KOMMUN	BYGGHANDLING		HANDLING
BJÖRN LIDSTRÖM		GODKÄND AV	TILLVERKNINGSRITNINGAR STÅL	ÄNDRING	FORMAT	A3
ARVID WENNERBERG		SKAPAD AV	PARTS	2024-12-20	DATUM	1:5
				NUMMER	BET	