


ANTAL	MONTAGEDEL
1	B/10

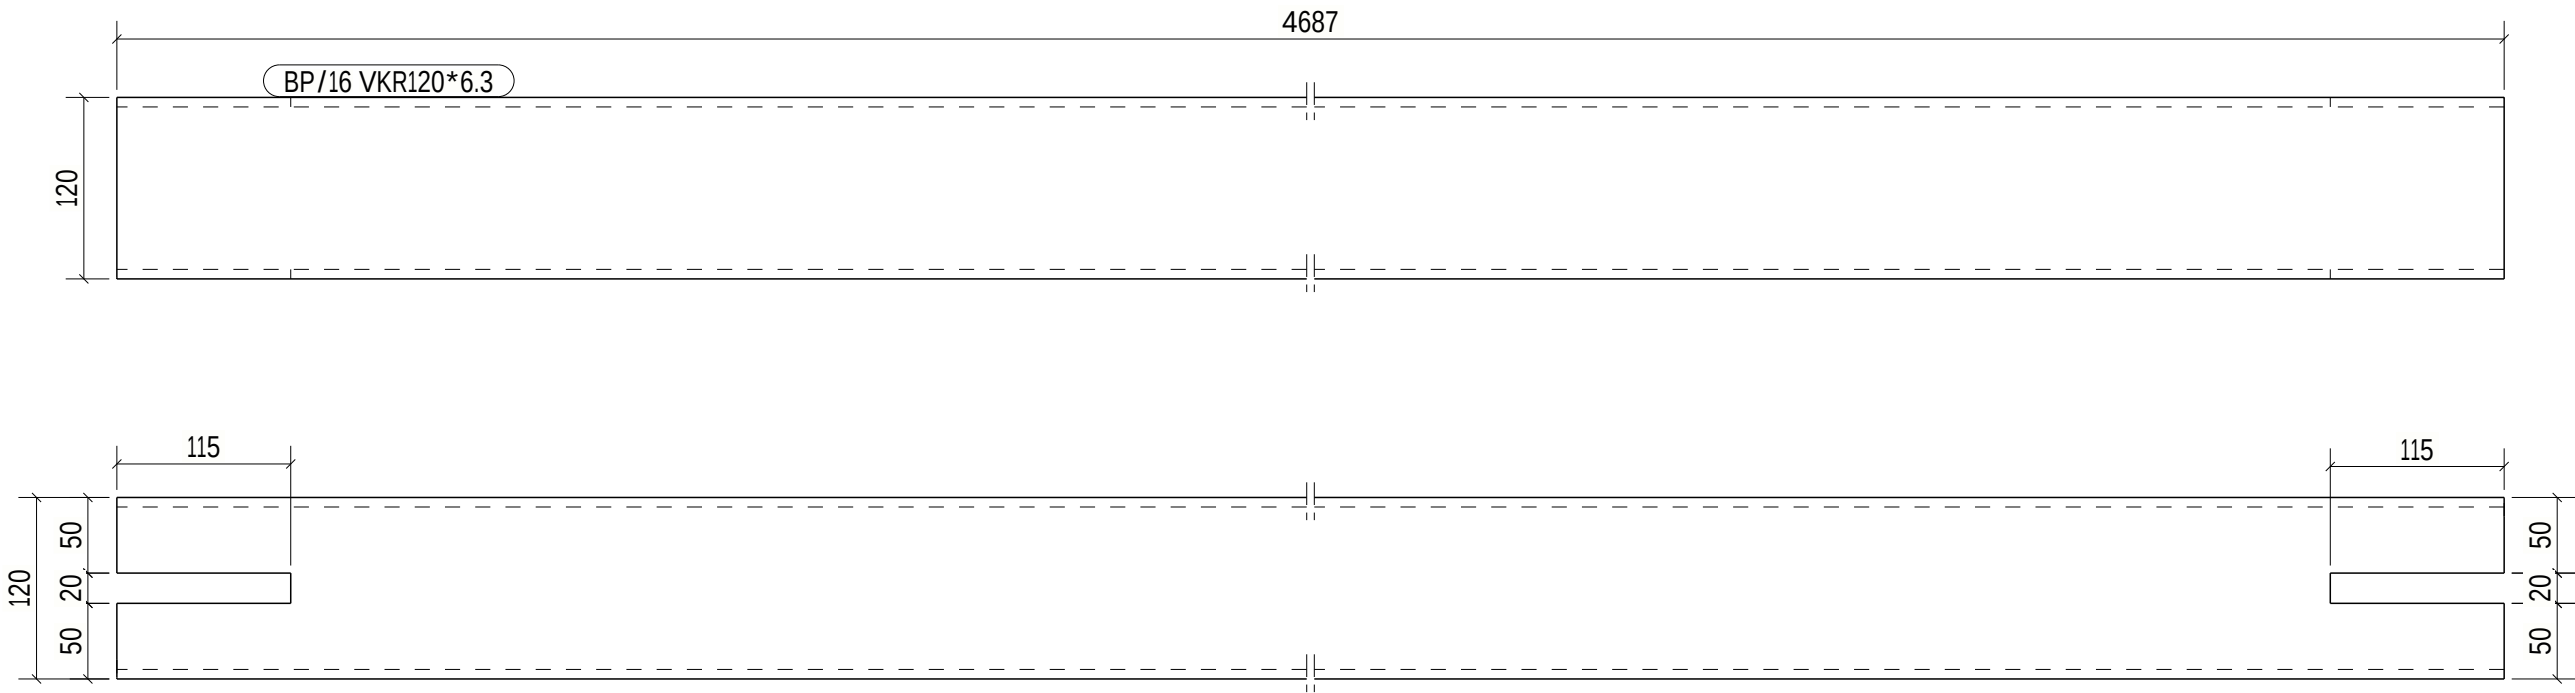

BP/16	VKR120*6.3	S355J2H	1	4687.0	2.16	103.8
MÄRKE	PROFIL	MATERIAL	ANTAL	LÄNGD	AREA	VIKT
MATERIALLISTA				TOTALT	2.16	103.8

Norconsult 		ANSVARIG PART	PROJEKT		FÖRFRÅGNINGSUNDERLAG		STATUS
CENTRALEKÖK ROBERTSFORS KOMMUN			BYGGHANDLING				HANDLING
					ÄNDRING	FORMAT	
BJÖRN LIDSTRÖM		KONTAKTPERSON	TILLVERKNINGSRITNINGAR STÅL		RITNINGSKATEGORI		A3
BJÖRN LIDSTRÖM		GODKÄND AV	PARTS		INNEHÅLL	DATUM	SKALA
ARVID WENNERBERG		SKAPAD AV				2024-12-20	1:5
					NUMMER	BET	
					BP/16		