


ANTAL	MONTAGEDEL
1	B/12

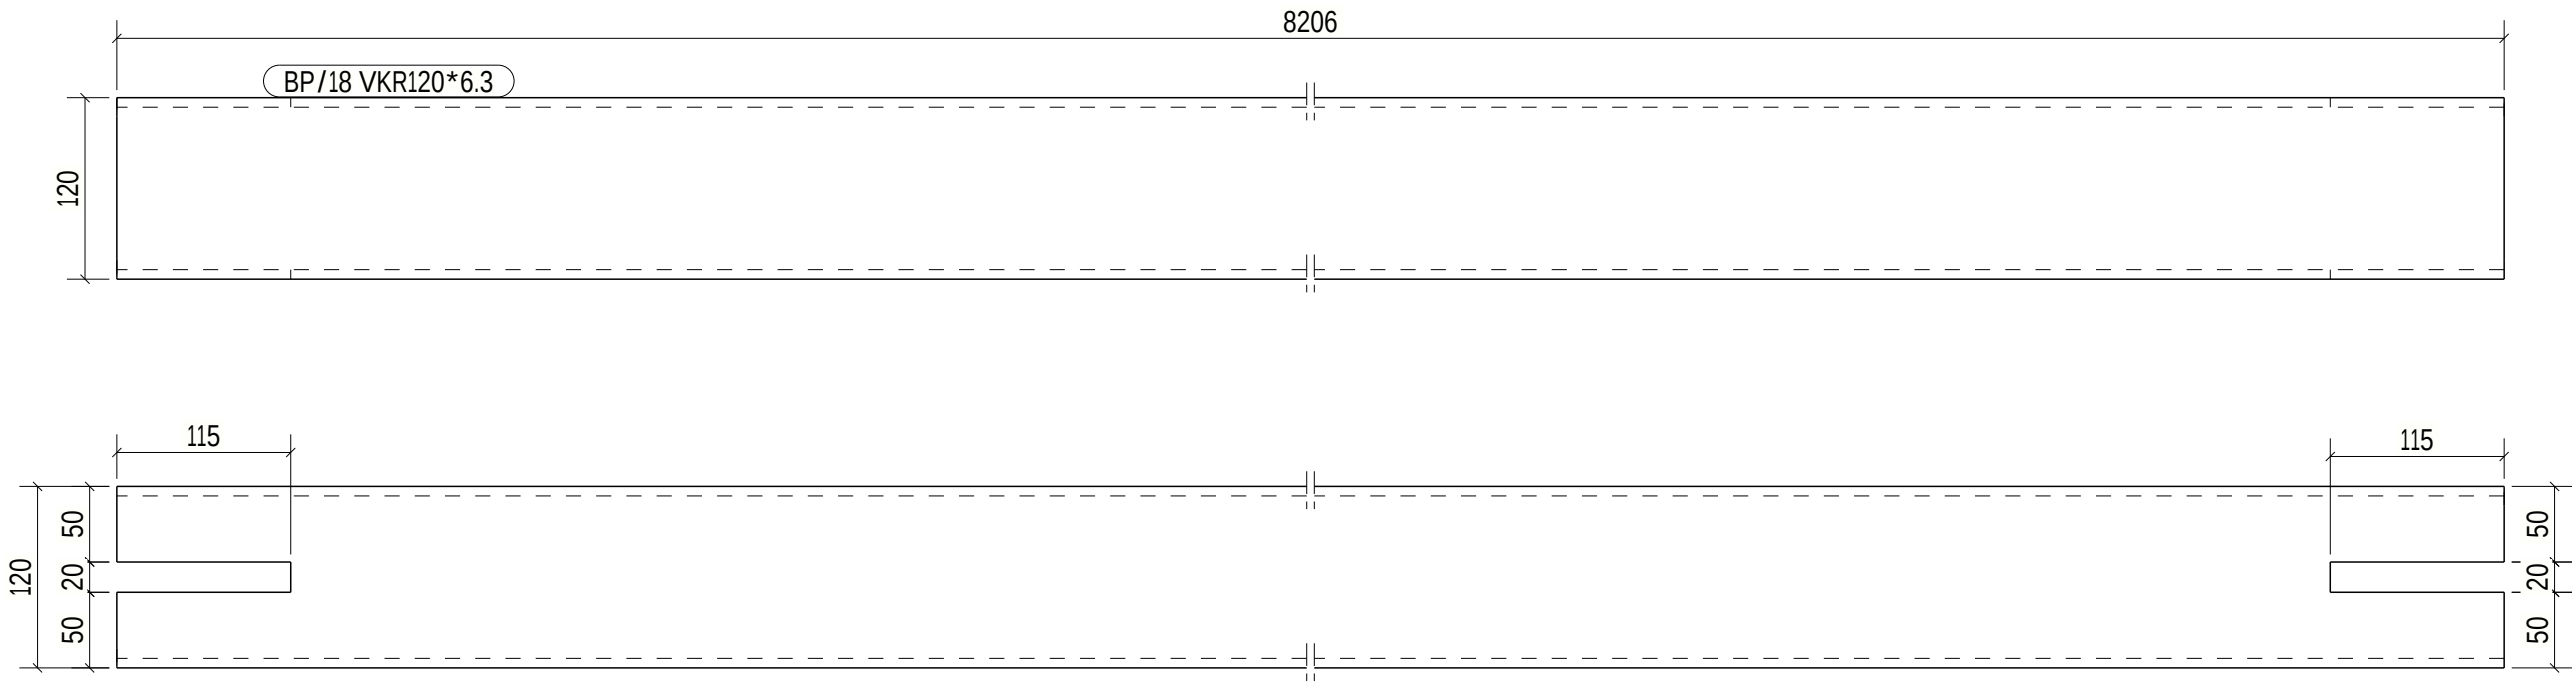

BP/18	VKR120*6.3	S355J2H	1	8205.9	3.77	181.7
MÄRKE	PROFIL	MATERIAL	ANTAL	LÄNGD	AREA	VIKT
MATERIALLISTA				TOTALT	3.77	181.7

Norconsult	ANSVARIG PART	PROJEKT		STATUS	
	KONTAKTPERSON	CENTRALKÖK ROBERTSFORS KOMMUN		FÖRFRÅGNINGSUNDERLAG	
	GODKÄND AV	TILLVERKNINGSRITNINGAR STÅL		BYGGHANDLING	
	SKAPAD AV	PARTS		A3	
		INNEHÅLL		ANDRING	FORMAT
		2024-12-20		DATUM	SKALA
		BP/18		NUMMER	BET