


ANTAL	MONTAGEDEL
1	B/13

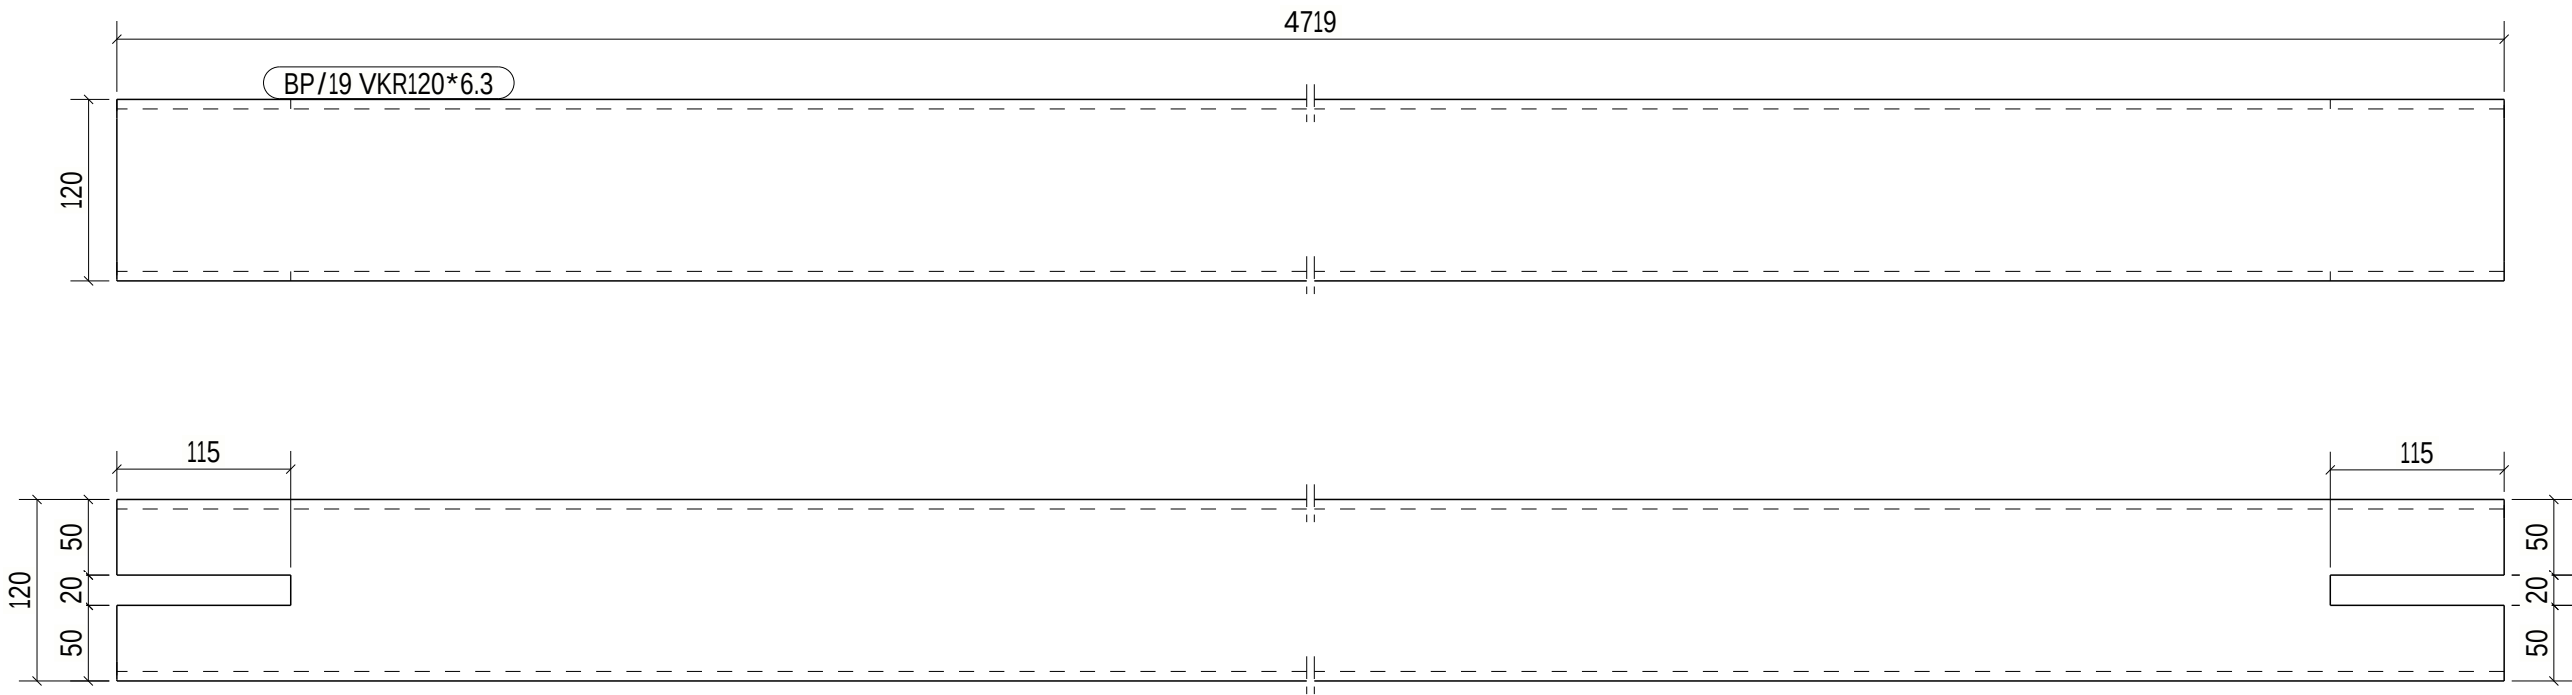

BP/19	VKR120*6.3	S355J2H	1	4718.8	2.17	104.5
MÄRKE	PROFIL	MATERIAL	ANTAL	LÄNGD	AREA	VIKT
MATERIALLISTA				TOTALT	2.17	104.5

Norconsult		ANSVARIG PART	CENTRALKÖK ROBERTSFORS KOMMUN		PROJEKT	FÖRFRÅGNINGSUNDERLAG		STATUS
BJÖRN LIDSTRÖM		KONTAKTPERSON	TILLVERKNINGSRITNINGAR STÅL		RITNINGSKATEGORI	BYGGHANDLING		HANDLING
BJÖRN LIDSTRÖM		GODKÄND AV	PARTS		INNEHÅLL	ÄNDRING		FORMAT
ARVID WENNERBERG		SKAPAD AV				2024-12-20		DATUM
						NUMMER		BET
						BP/19		