


ANTAL	MONTAGEDEL
2	B/1

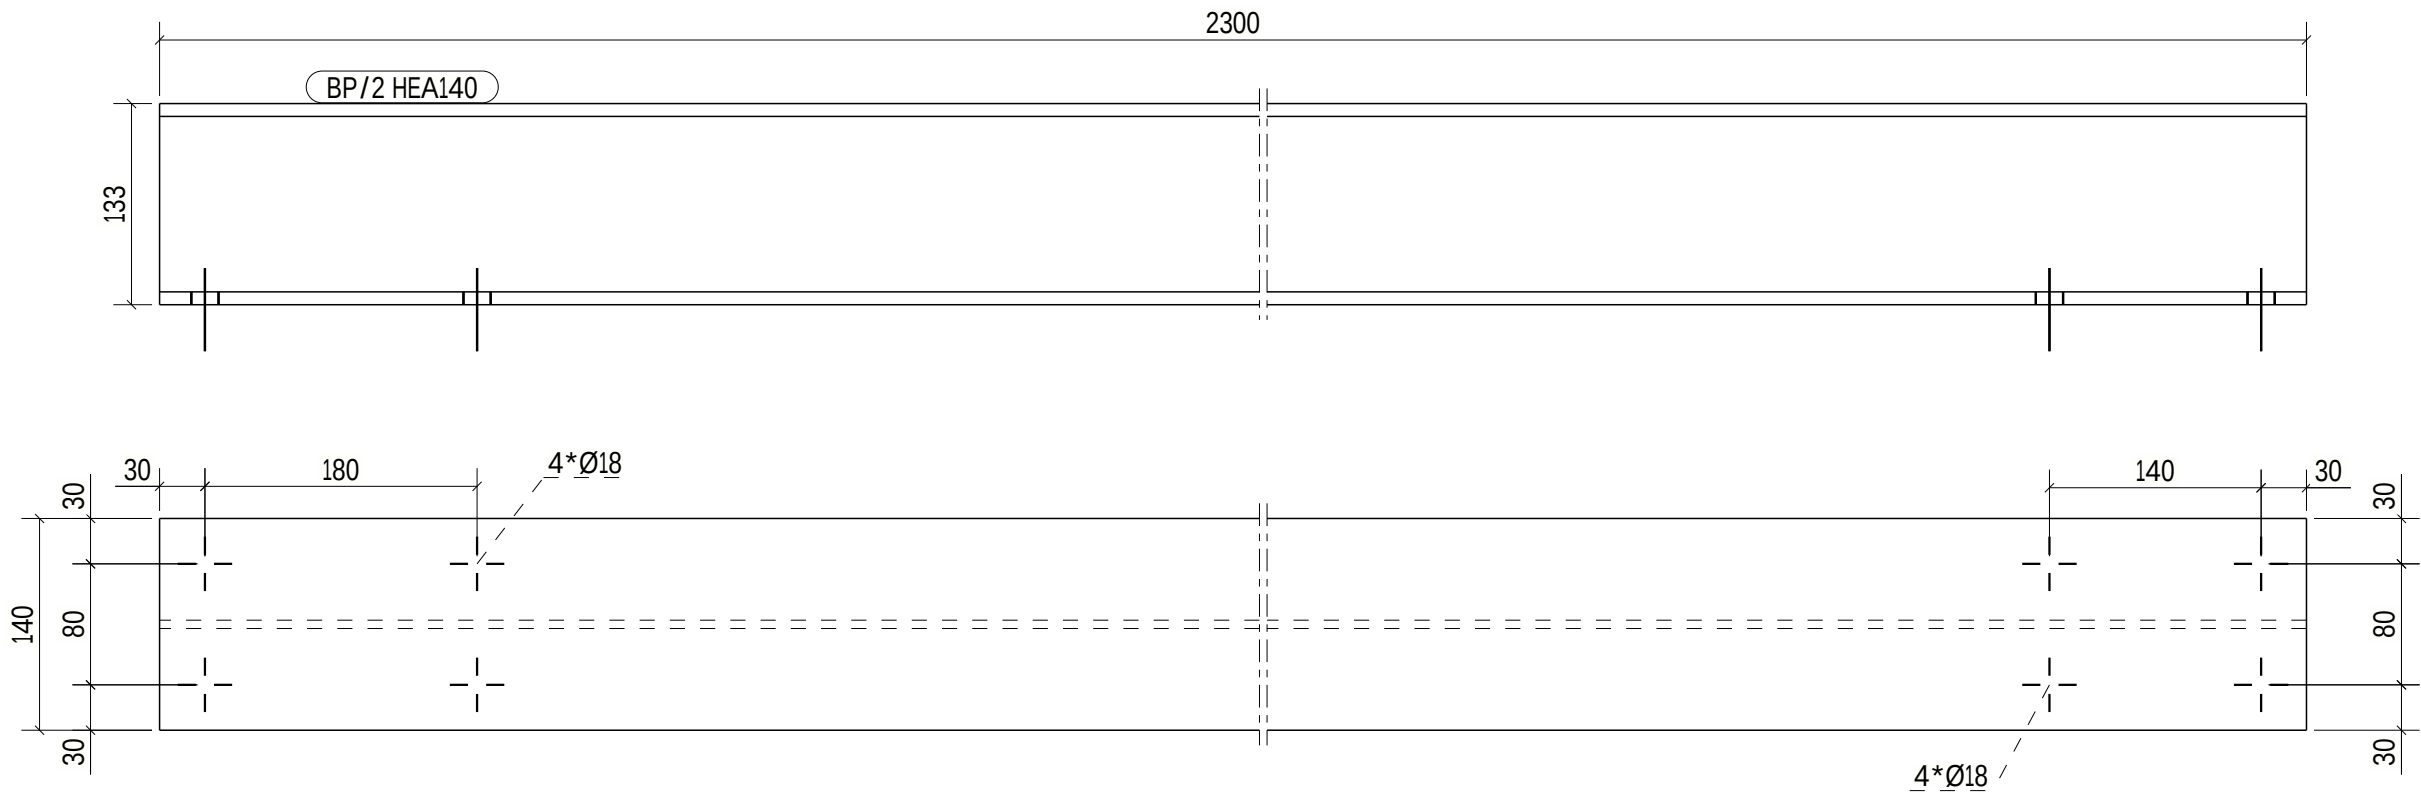

BP/2	HEA140	S355J2	2	2300.0	1.83	56.7
MÄRKE	PROFIL	MATERIAL	ANTAL	LÄNGD	AREA	VIKT
MATERIALLISTA				TOTALT	3.65	113.5

Norconsult 		ANSVARIG PART	PROJEKT		FÖRFRÅGNINGSUNDERLAG		STATUS	
CENTRALEKÖ ROBERTSFORS KOMMUN			BYGGHANDLING				HANDLING	
			TILLVERKNINGSRITNINGAR STÅL		RITNINGSKATEGORI	ÄNDRING	FORMAT	
BJÖRN LIDSTRÖM		KONTAKTPERSON	INNEHÅLL		2024-12-20		DATUM	SKALA
BJÖRN LIDSTRÖM		GODKÄND AV			1:5		NUMMER	BET
ARVID WENNERBERG		SKAPAD AV	PARTS		BP/2			