


ANTAL	MONTAGEDEL
1	B/14

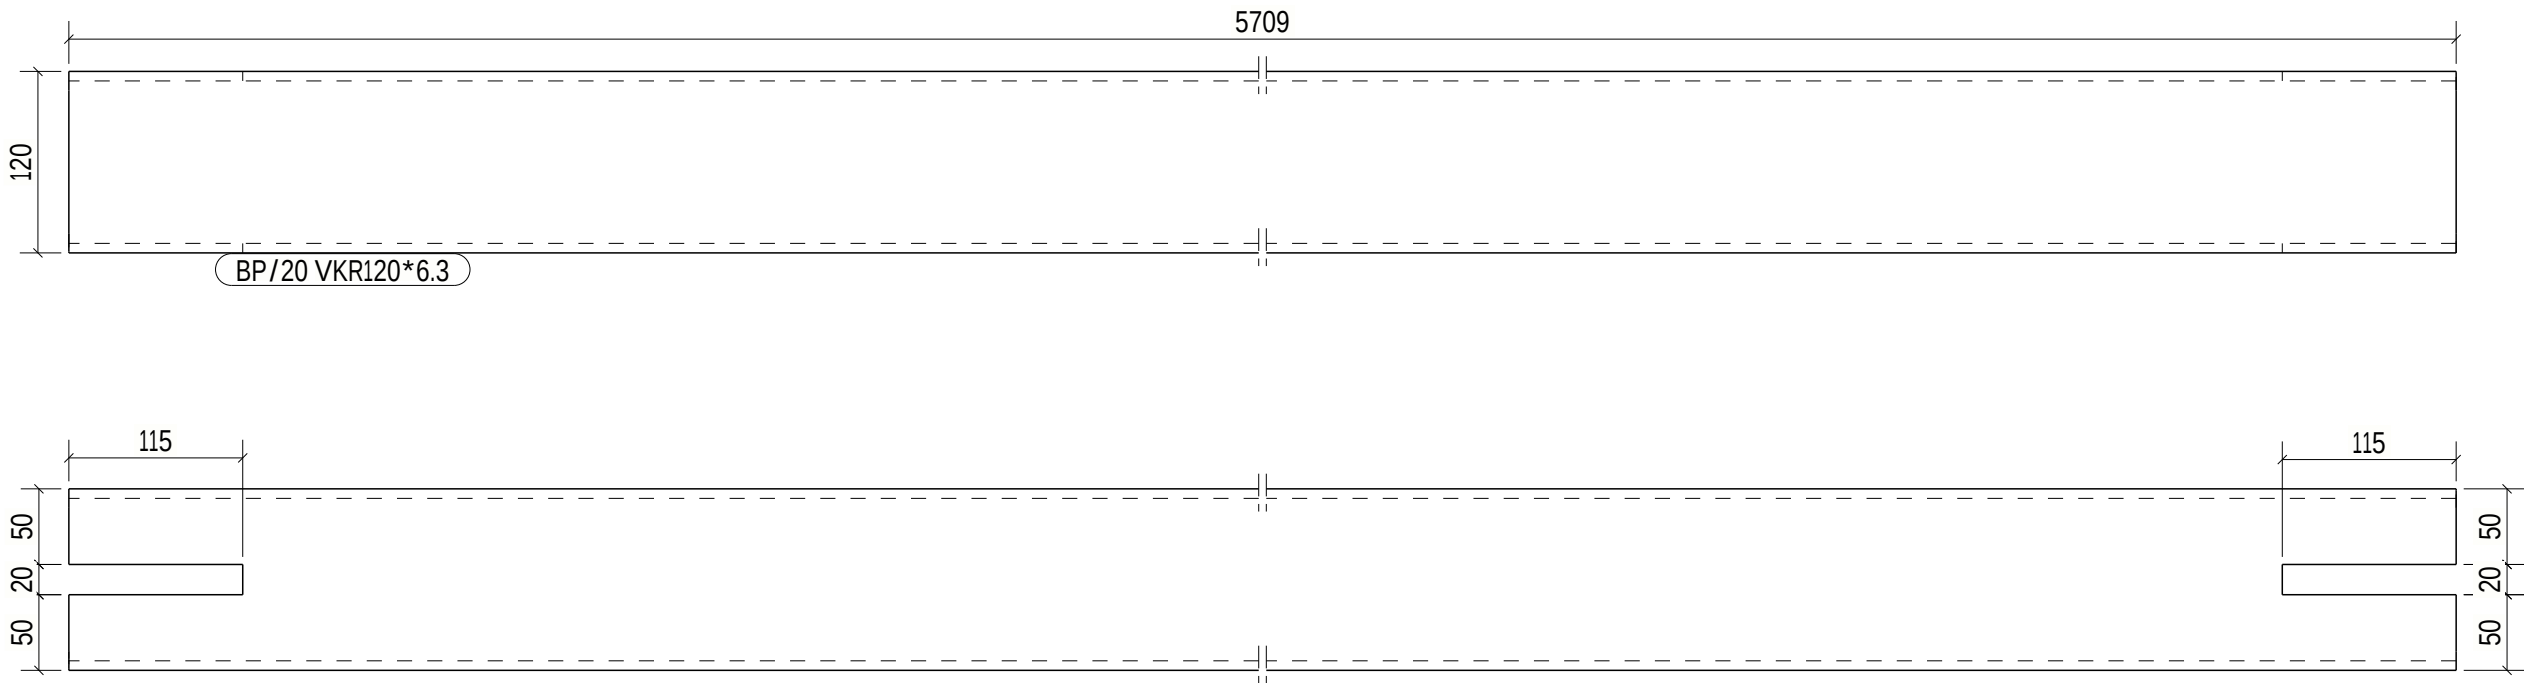

BP /20	VKR120*6.3	S355J2H	1	5708.6	2.63	126.4
MÄRKE	PROFIL	MATERIAL	ANTAL	LÄNGD	AREA	VIKT
MATERIALLISTA				TOTALT	2.63	126.4

Norconsult	ANSVARIG PART	PROJEKT	FÖRFRÅGNINGSUNDERLAG		STATUS
	BJÖRN LIDSTRÖM	CENTRALKÖK ROBERTSFORS KOMMUN	BYGGHANDLING		HANDLING
	BJÖRN LIDSTRÖM	TILLVERKNINGSRITNINGAR STÅL	ÄNDRING	A3	FORMAT
	ARVID WENNERBERG	PARTS	2024-12-20	1:5	SKALA
			NUMMER	BET	
			BP /20		