


ANTAL	MONTAGEDEL
1	B/16

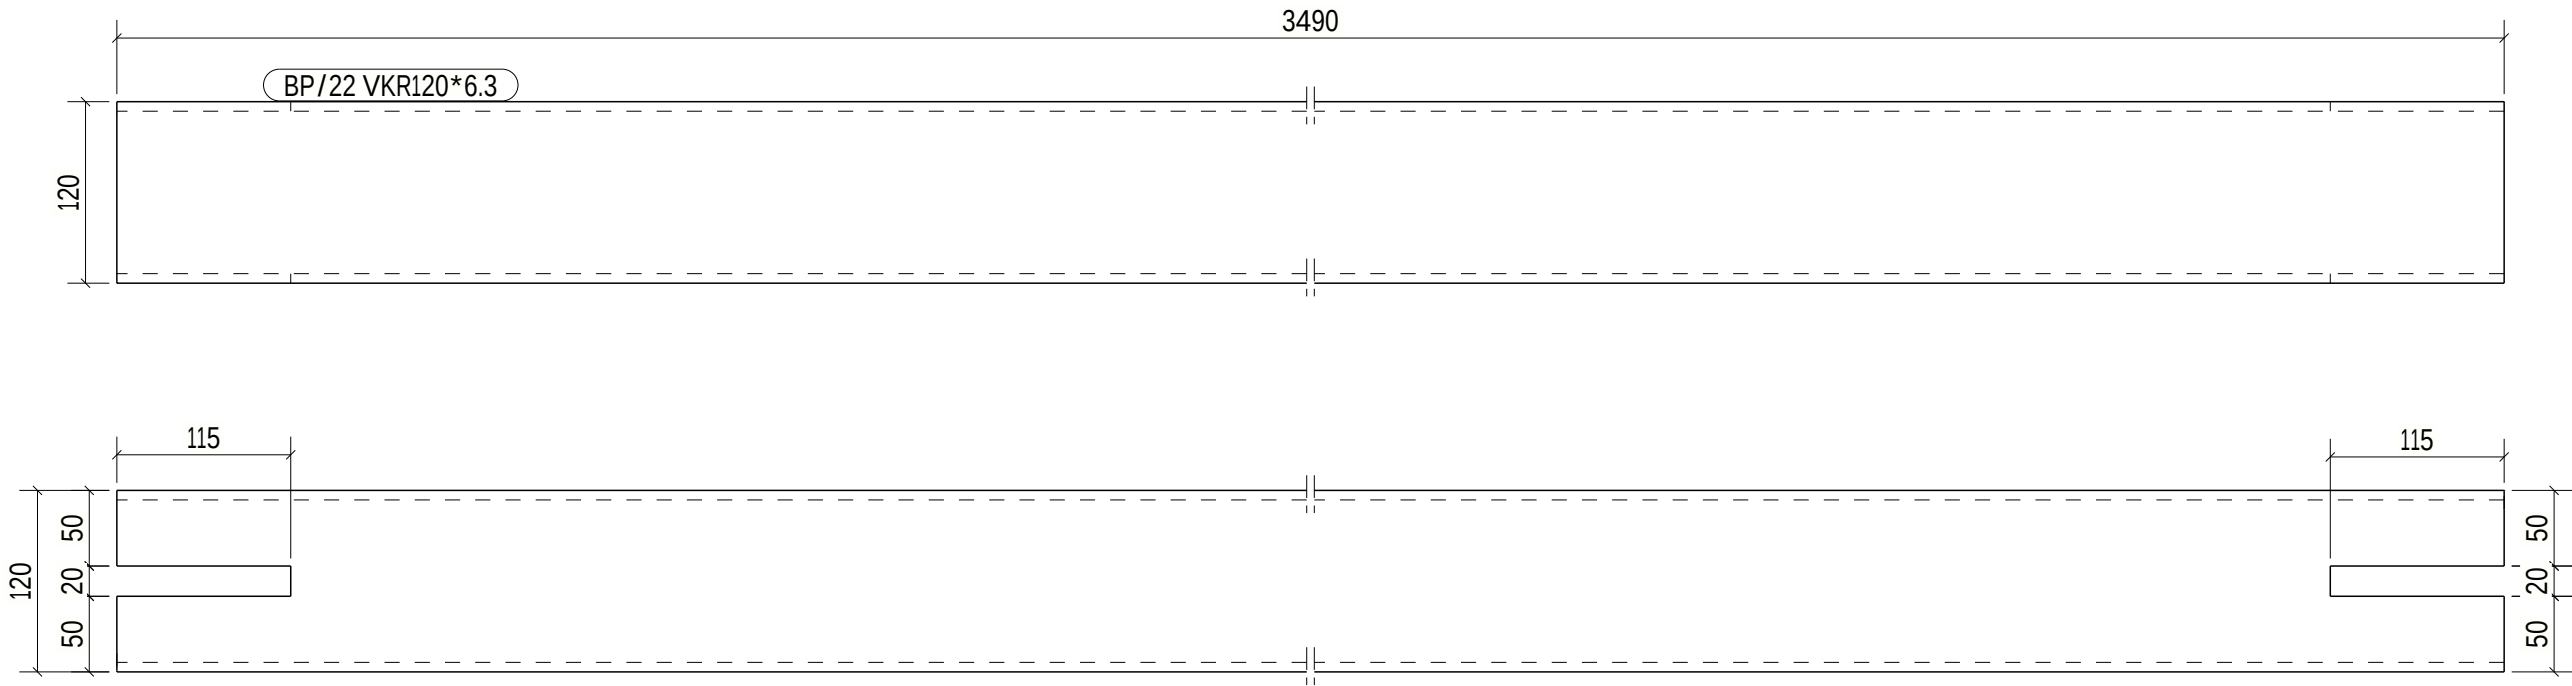

BP/22	VKR120*6.3	S355J2H	1	3490.5	1.61	77.3
MÄRKE	PROFIL	MATERIAL	ANTAL	LÄNGD	AREA	VIKT
MATERIALLISTA				TOTALT	1.61	77.3

Norconsult ANSVARIG PART	PROJEKT		STATUS	
	CENTRALEKÖK ROBERTSFORS KOMMUN		FÖRFRÅGNINGSUNDERLAG	
	TILLVERKNINGSRITNINGAR STÅL		BYGGHANDLING	
	PARTS		A3	
BJÖRN LIDSTRÖM		RITNINGSKATEGORI		ÄNDRING
BJÖRN LIDSTRÖM		INNEHÅLL		FORMAT
ARVID WENNERBERG		2024-12-20		SKALA
		1:5		BET
		BP/22		