ANTAL	MONTAGEDEL
1	B/22

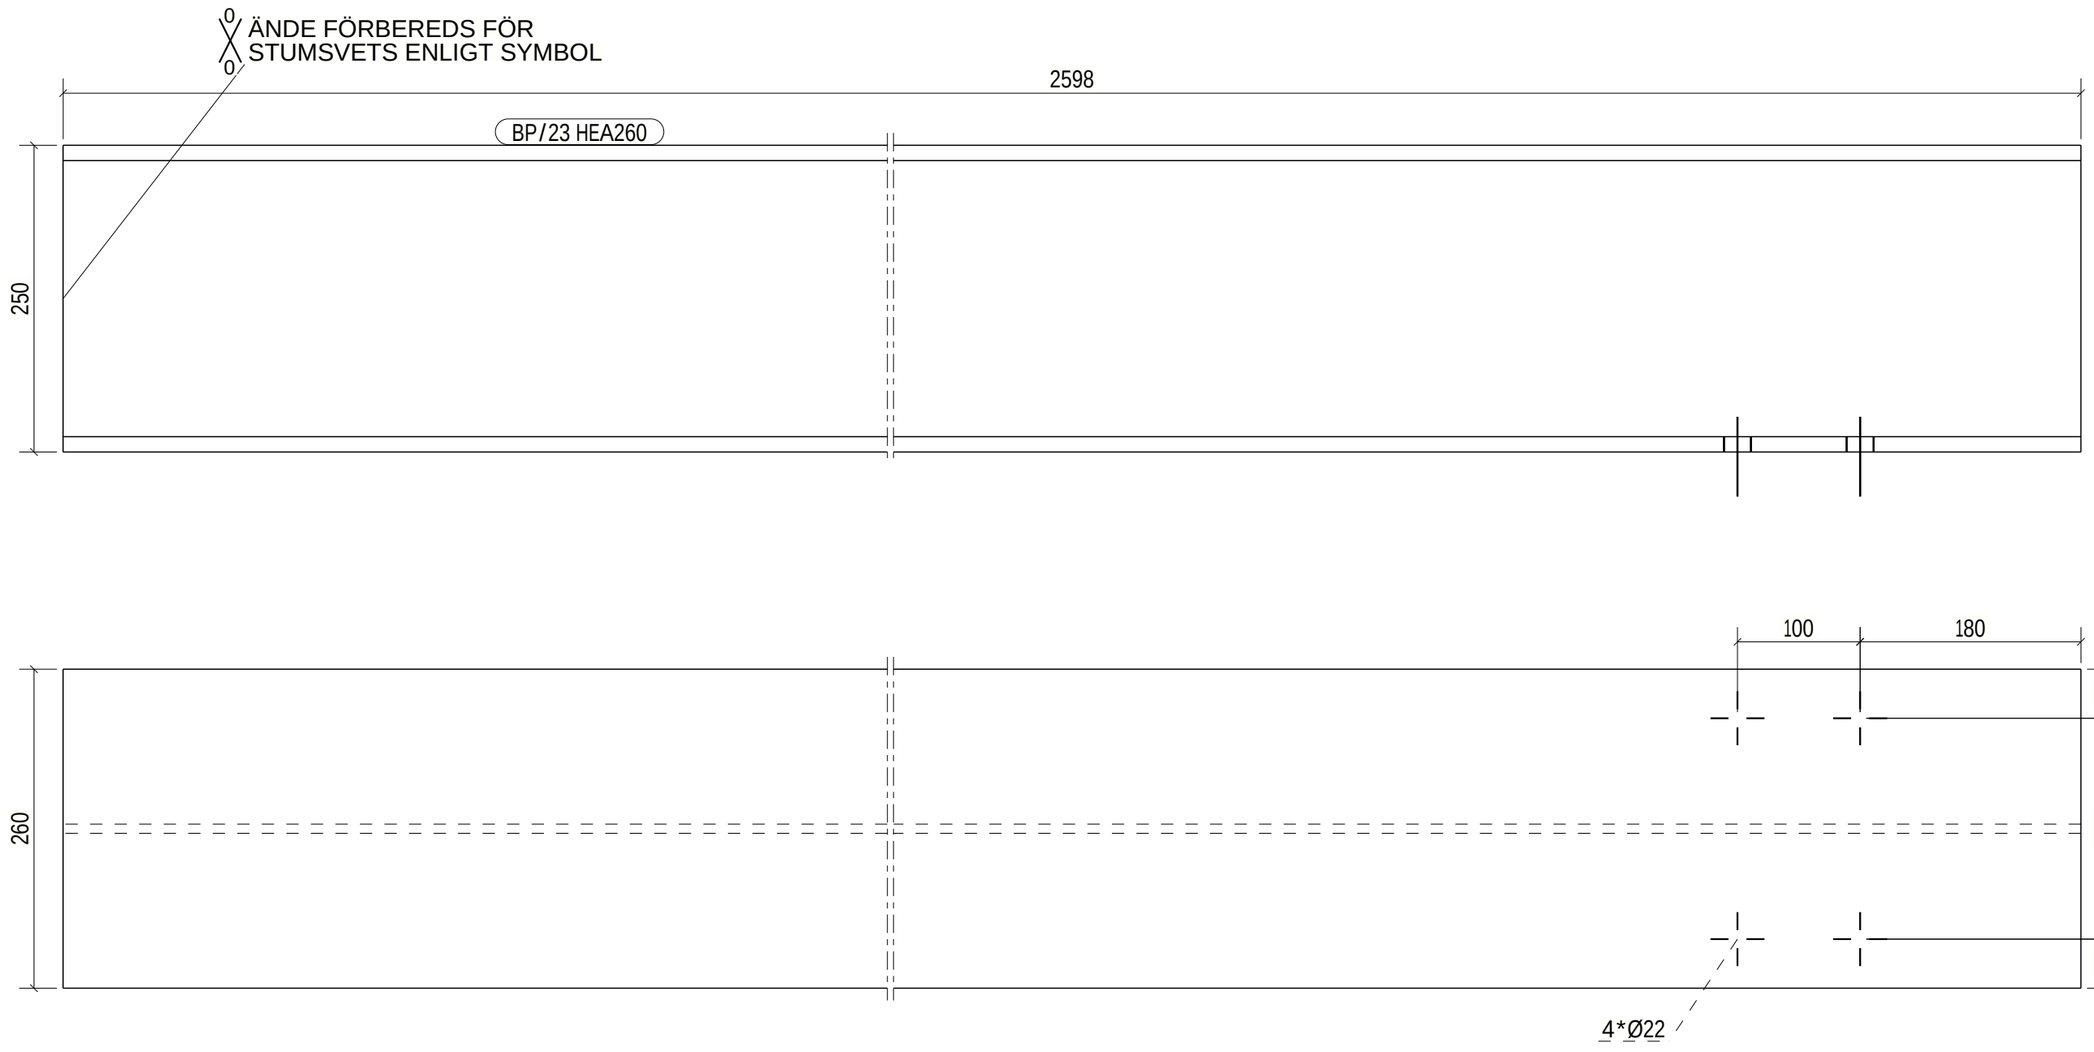

BP/23	HEA260	S355J2	1	2598.0	3.86	177.1
MÄRKE	PROFIL	MATERIAL	ANTAL	LÄNGD	AREA	VIKT
MATERIALLISTA				TOTALT	3.86	177.1

ANSVARIG PART: Norconsult	PROJEKT: CENTRALKÖK ROBERTSFORS KOMMUN	STATUS: FÖRFRÅGNINGSUNDERLAG
KONTAKTPERSON: BJÖRN LIDSTRÖM		HANDLING: BYGGHANDLING
GODKÄND AV: BJÖRN LIDSTRÖM	RITNINGSKATEGORI: TILLVERKNINGSRITNINGAR STÅL	ÄNDRING: — / FORMAT: A3
SKAPAD AV: ARVID WENNBERG	INNEHÅLL: PARTS	DATUM: 2024-12-20 / SKALA: 1:5
		NUMMER: BP/23 / BET:

Tekla Structures