ANTAL	MONTAGEDEL
1	B/21

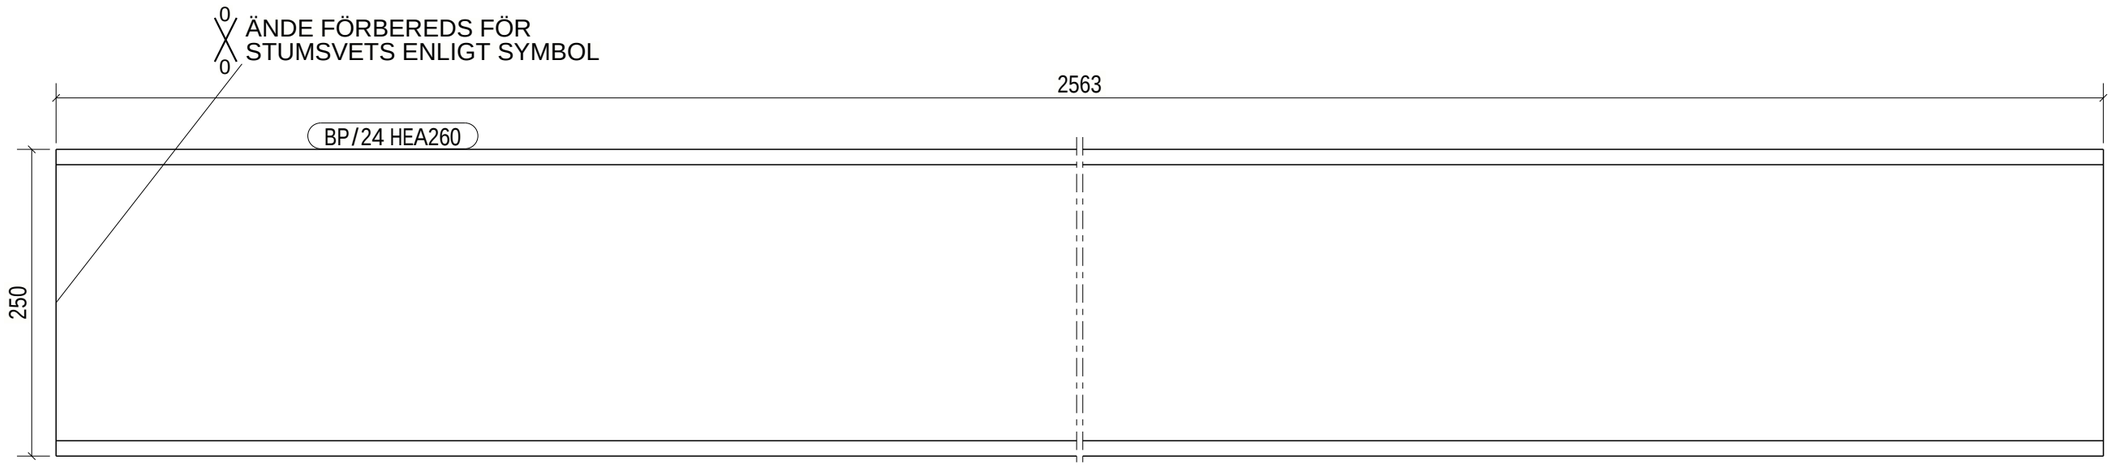

BP/24	HEA260	S355J2	1	2563.0	3.80	174.7
MÄRKE	PROFIL	MATERIAL	ANTAL	LÄNGD	AREA	VIKT
MATERIALLISTA				TOTALT	3.80	174.7

Norconsult ANSVARIG PART	PROJEKT CENTRALKÖK ROBERTSFORS KOMMUN	STATUS FÖRFRÅGNINGSUNDERLAG
KONTAKTPERSON BJÖRN LIDSTRÖM		HANDLING BYGGHANDLING
GODKÄND AV BJÖRN LIDSTRÖM	RITNINGSKATEGORI TILLVERKNINGSRITNINGAR STÅL	ÄNDRING FORMAT A3
SKAPAD AV ARVID WENNBERG	INNEHÅLL PARTS	DATUM 2024-12-20 SKALA 1:5
		NUMMER BP/24 BET

Tekla Structures