


ANTAL	MONTAGEDEL
1	B/25

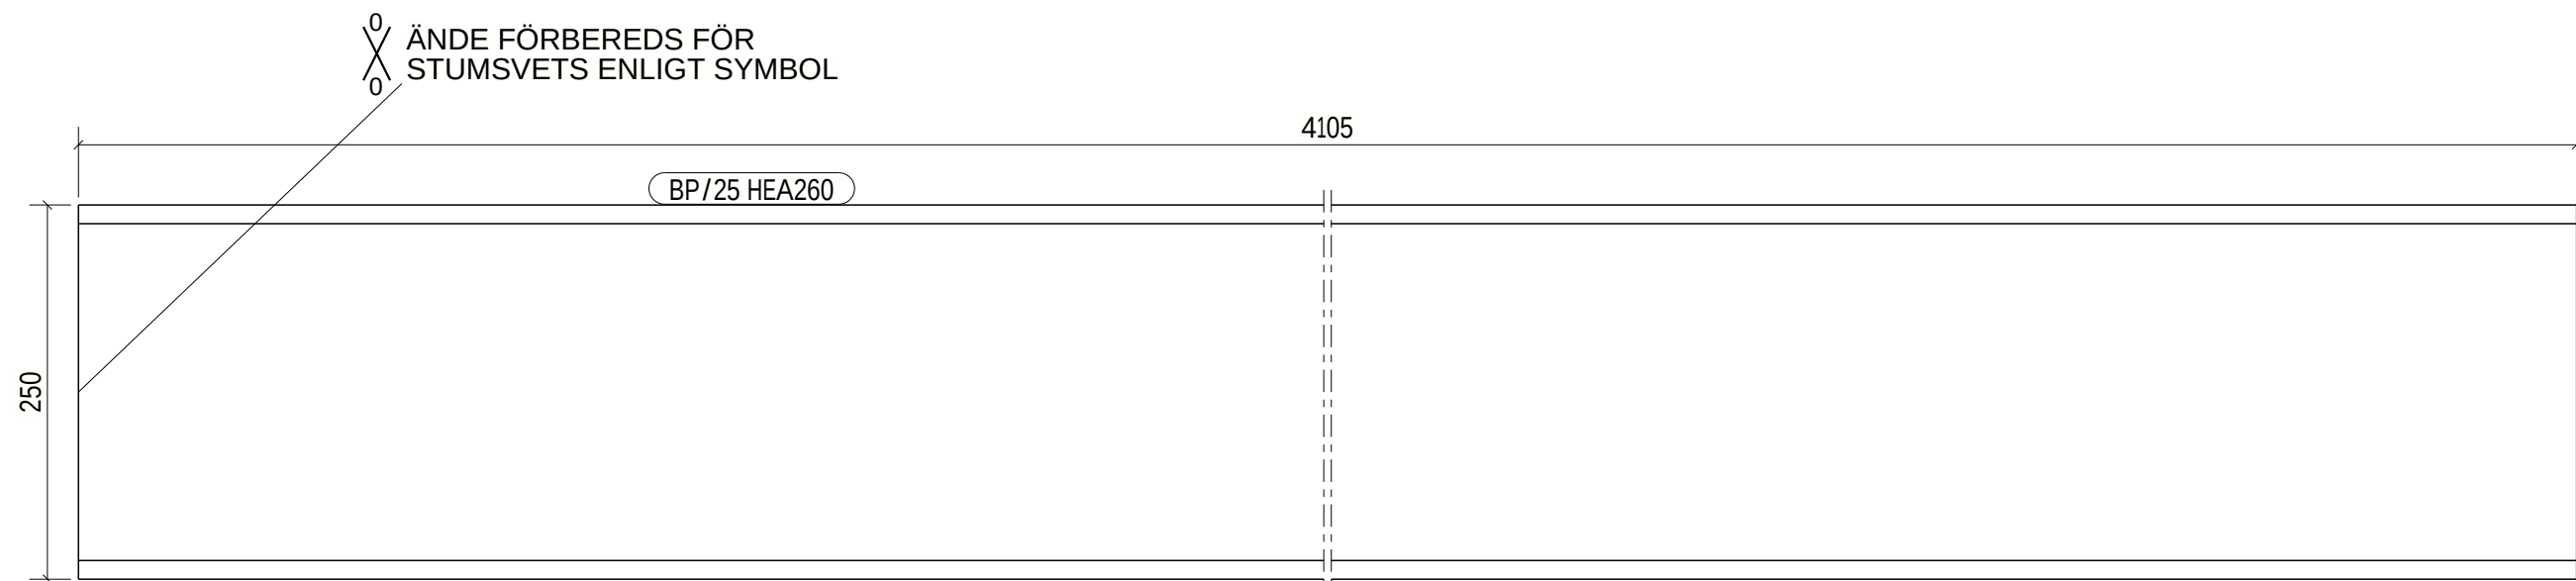

BP/25	HEA260	S355J2	1	4105.0	6.09	279.8
MÄRKE	PROFIL	MATERIAL	ANTAL	LÄNGD	AREA	VIKT
MATERIALLISTA				TOTALT	6.09	279.8

Norconsult		ANSVARIG PART	PROJECT	FÖRFRÅGNINGSUNDERLAG		STATUS
BJÖRN LIDSTRÖM		KONTAKTPERSON	CENTRALEKÖB ROBERTSFORS KOMMUN	BYGGHANDLING		HANDLING
BJÖRN LIDSTRÖM		GÖDKÄND AV	TILLVERKNINGSRITNINGAR STÅL	ÄNDRING		FORMAT
ARVID WENNBERG		SKAPAD AV	PARTS	2024-12-20		A3
				NUMMER		SKALA
				BP/25		BET