


ANTAL	MONTAGEDEL
2	B/30

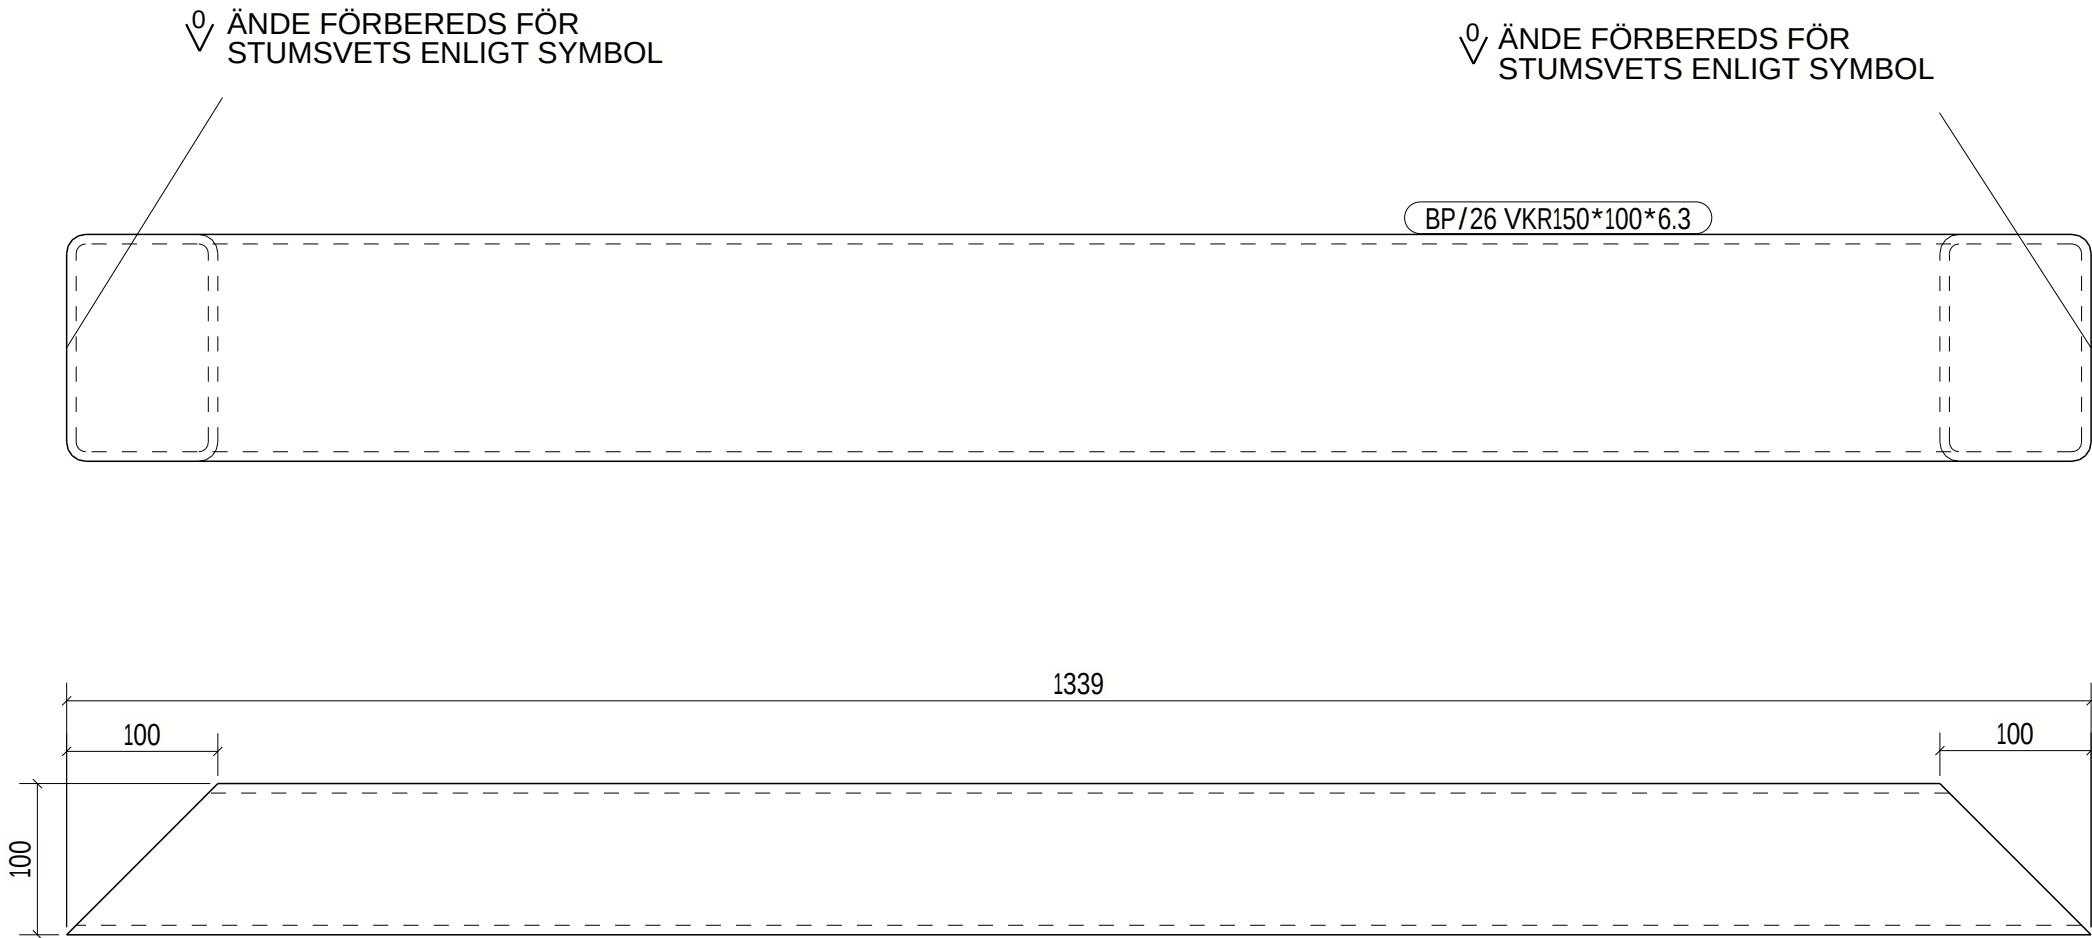

BP/26	VKR150*100*6.3	S355J2H	2	1339.0	0.64	31.0
MÄRKE	PROFIL	MATERIAL	ANTAL	LÄNGD	AREA	VIKT
MATERIALLISTA				TOTALT	1.29	62.0

Norconsult ANSVARIG PART	CENTRALKÖK ROBERTSFORS KOMMUN		FÖRFRÅGNINGSUNDERLAG	
	TILLVERKNINGSRITNINGAR STÅL		BYGGHANDLING	
	PARTS		2024-12-20	A3
			BP/26	