


ANTAL	MONTAGEDEL
1	B/4

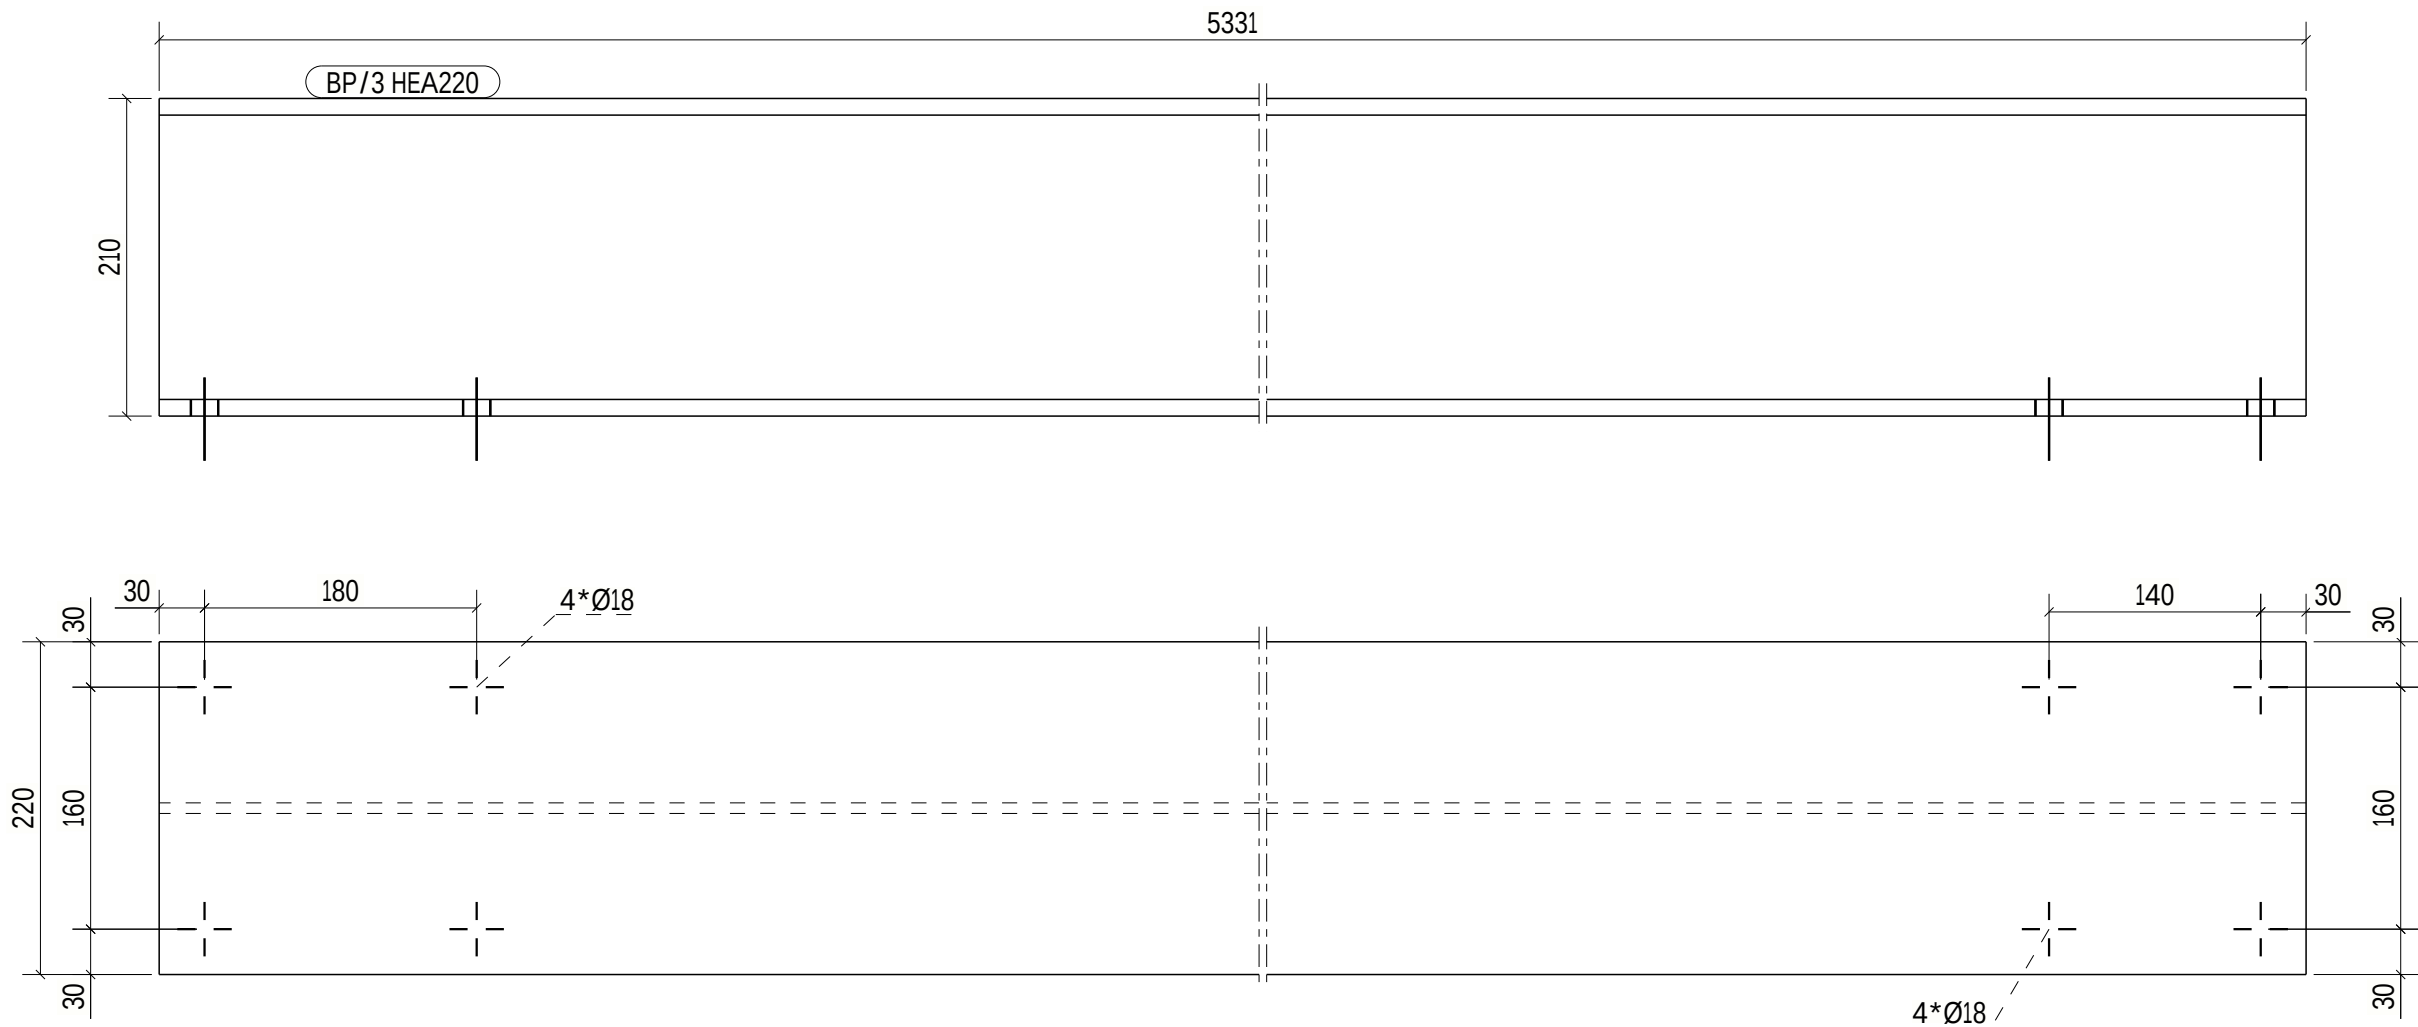

BP/3	HEA220	S355J2	1	5331.0	6.69	269.3
MÄRKE	PROFIL	MATERIAL	ANTAL	LÄNGD	AREA	VIKT
MATERIALLISTA				TOTALT	6.69	269.3

Norconsult		ANSVARIG PART	PROJEKT		STATUS	
			CENTRALEKÖ ROBERTSFORS KOMMUN		FÖRFRÅGNINGSUNDERLAG	
BJÖRN LIDSTRÖM		KONTAKTPERSON			HANDLING	
BJÖRN LIDSTRÖM		GODKÄND AV	TILLVERKNINGSRITNINGAR STÅL		BYGGHANDLING	
ARVID WENNERBERG		SKAPAD AV			ÄNDRING	FORMAT
			INNEHÅLL		2024-12-20	A3
					DATUM	SKALA
			PARTS		NUMMER	BET
					BP/3	