


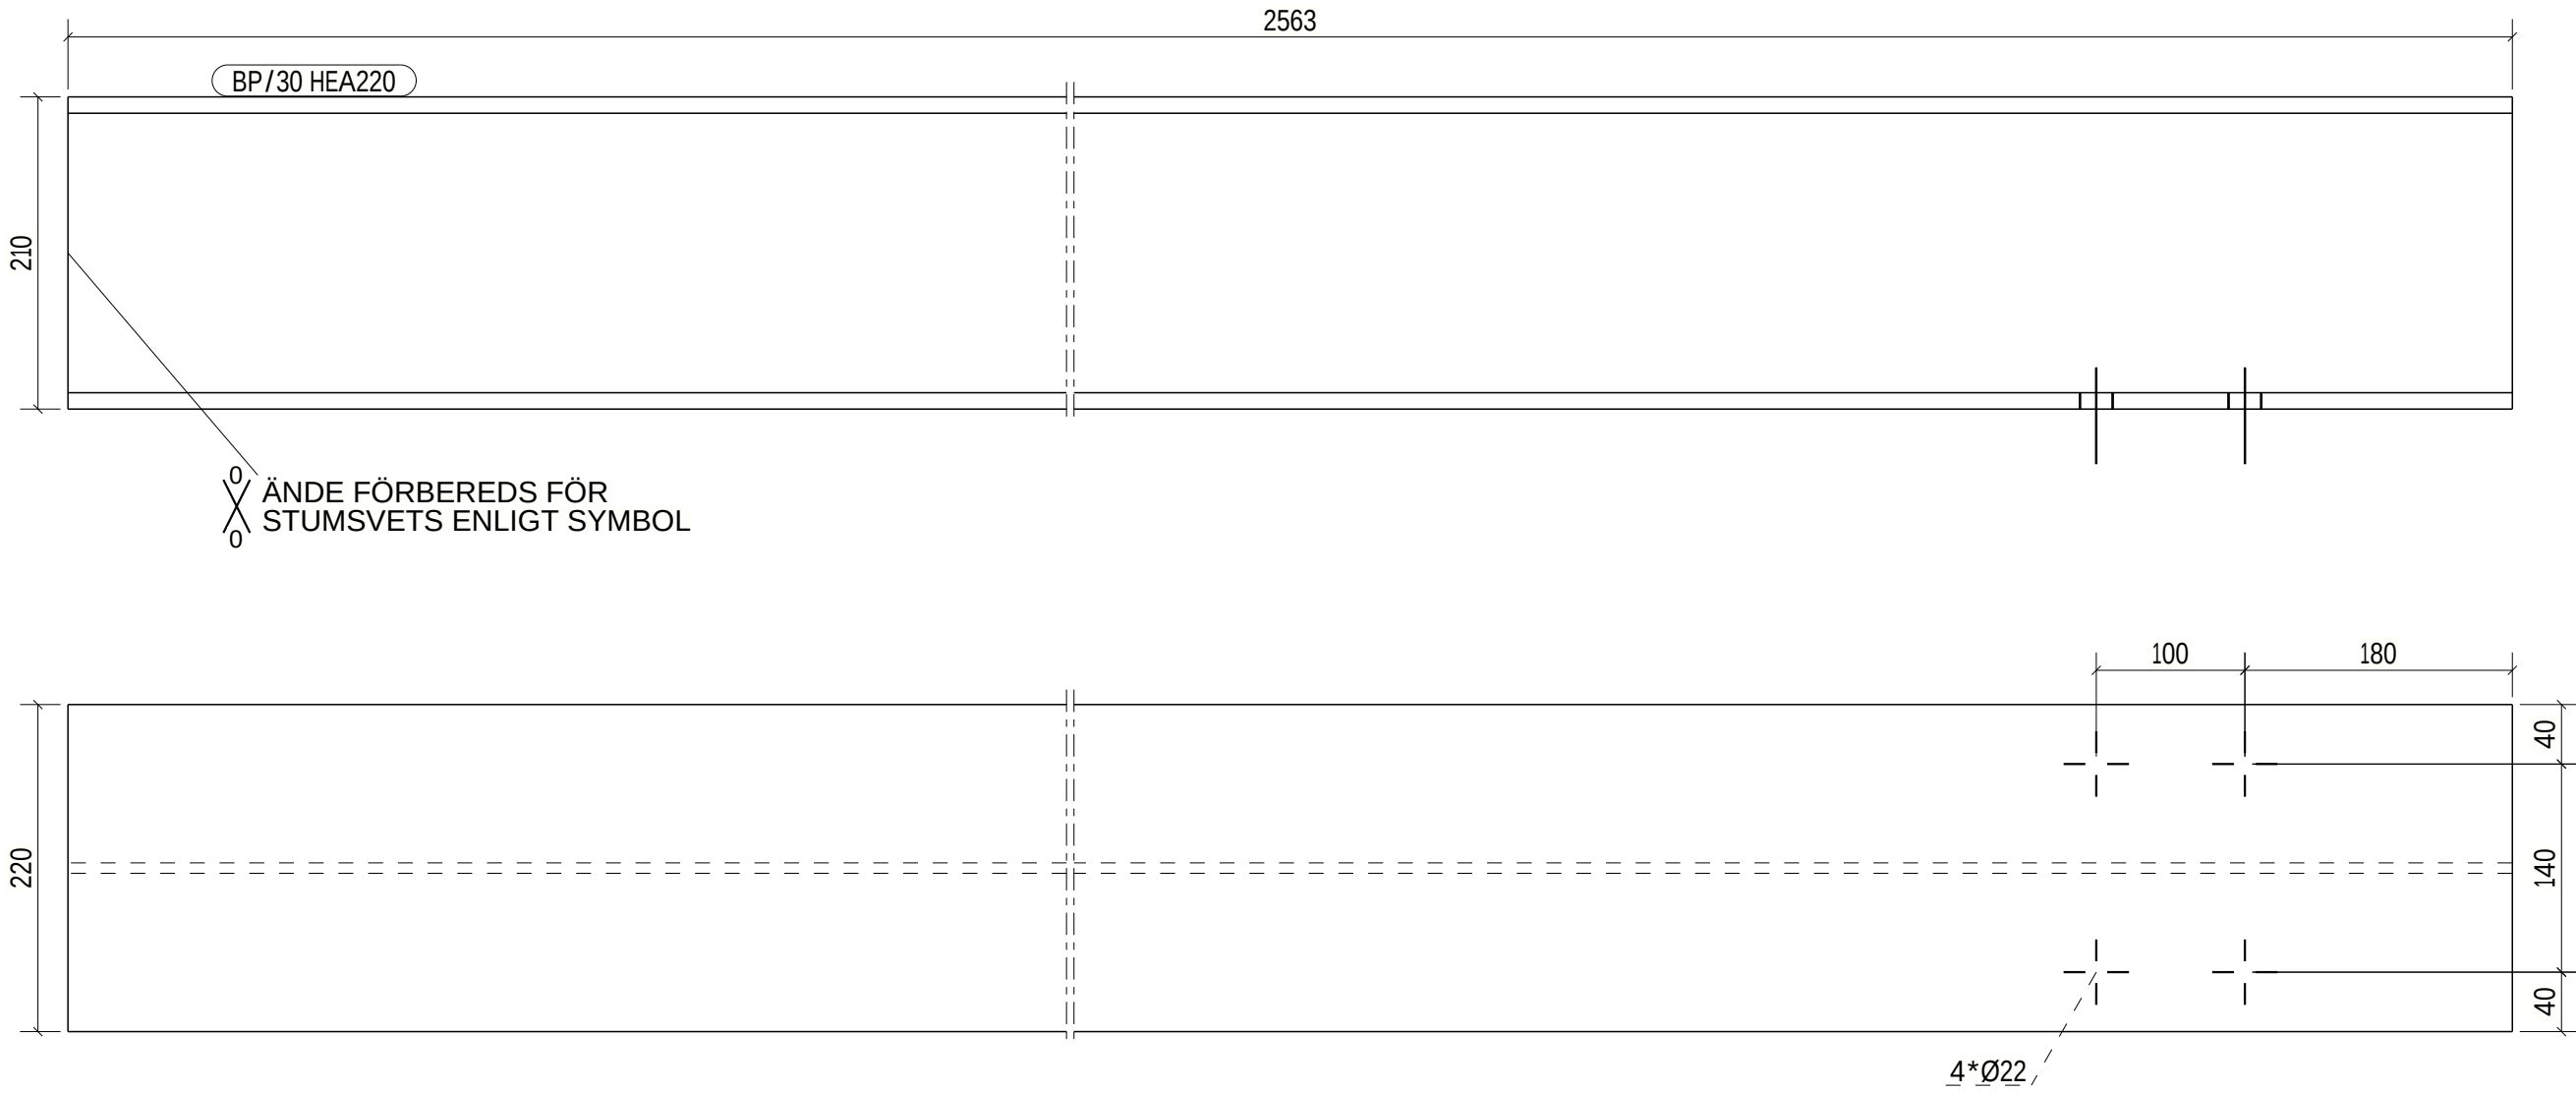

ANTAL	MONTAGEDEL
1	B/6

BP/30	HEA220	S355J2	1	2563.0	3.22	129.5
MÄRKE	PROFIL	MATERIAL	ANTAL	LÄNGD	AREA	VIKT
MATERIALLISTA				TOTALT	3.22	129.5

Norconsult 		ANSVARIG PART	PROJEKT		FÖRFRÅGNINGSUNDERLAG		STATUS		
BJÖRN LIDSTRÖM			CENTRALKÖK ROBERTSFORS KOMMUN		BYGGHANDLING			HANDLING	
			TILLVERKNINGSRITNINGAR STÅL		RITNINGSKATEGORI			ÄNDRING	FORMAT
					INNEHÅLL	2024-12-20		DATUM	SKALA
					BP/30		NUMMER	BET	
BJÖRN LIDSTRÖM							A3		
ARVID WENNERBERG			PARTS						