


ANTAL	MONTAGEDEL
1	B/28

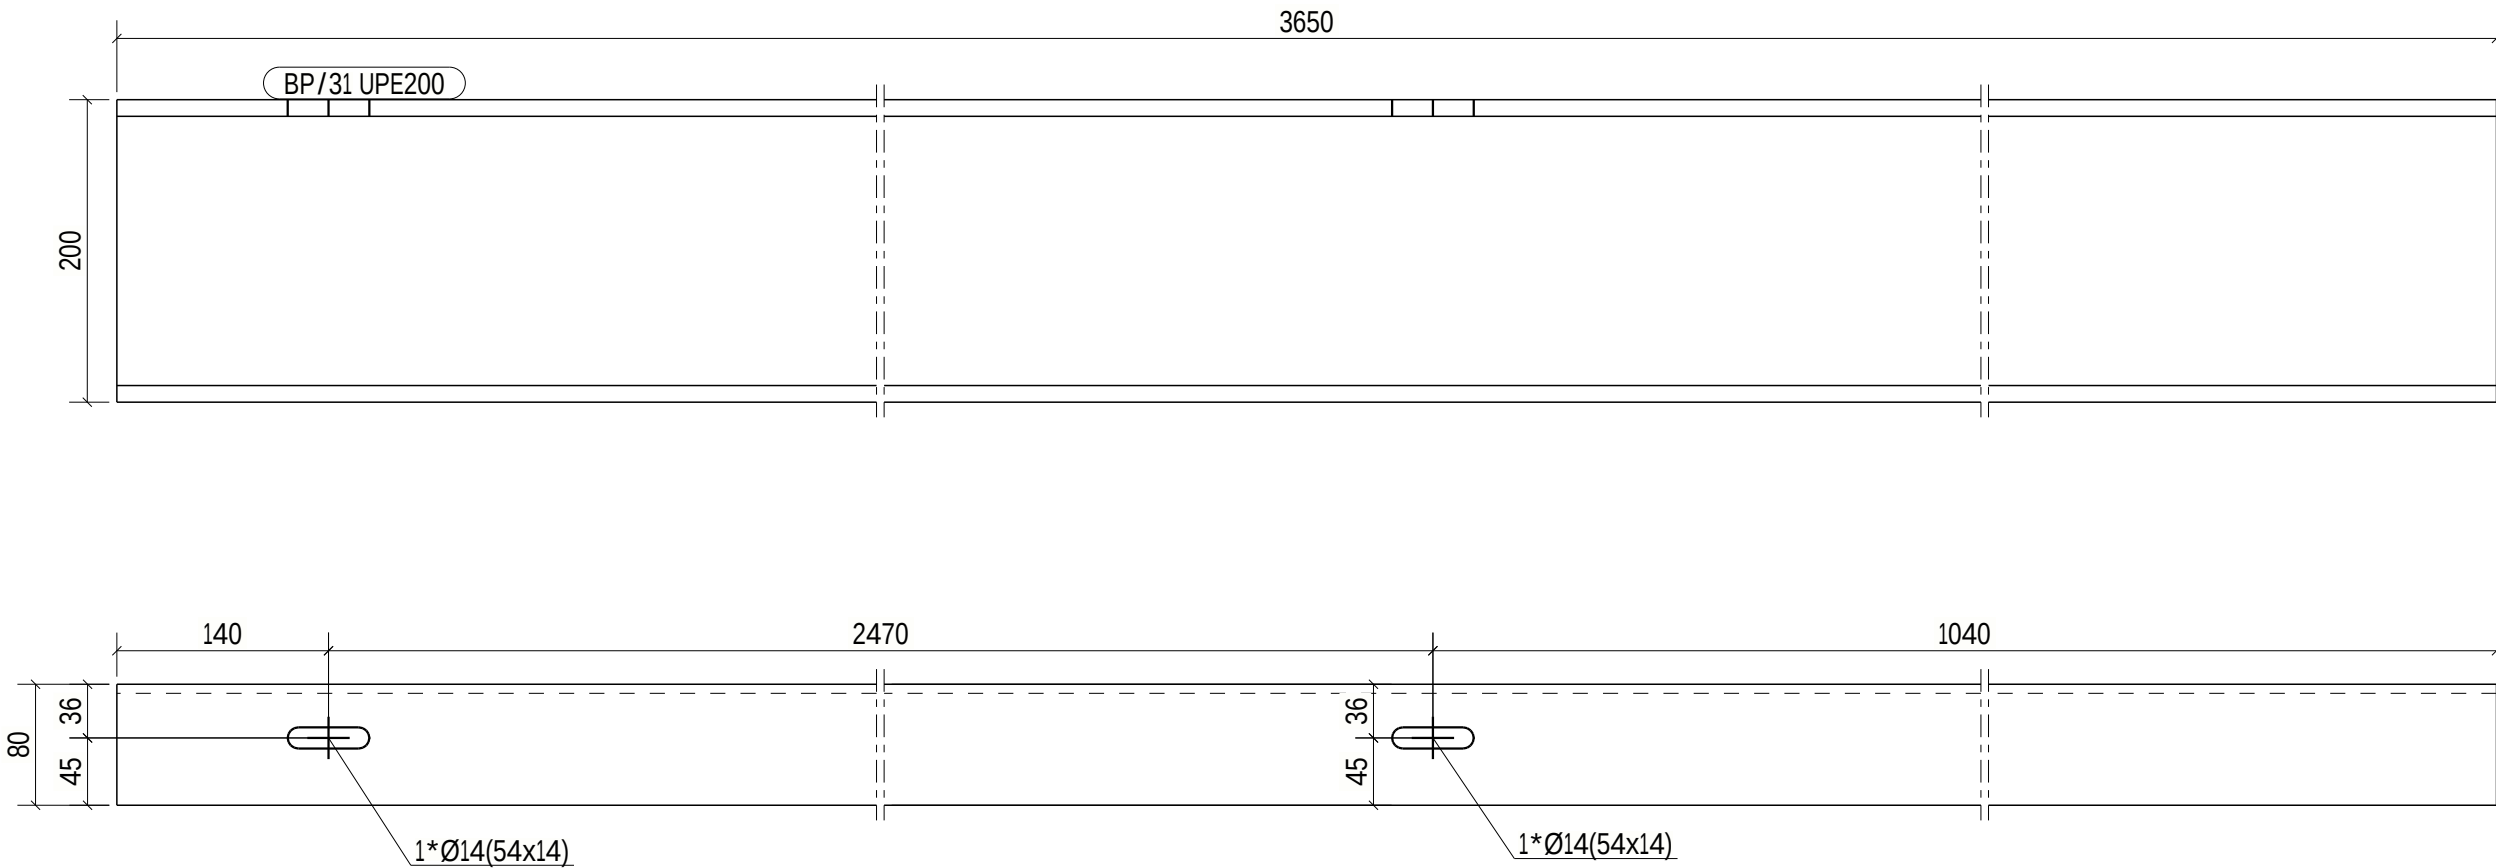

BP/31	UPE200	S355J2	1	3650.0	2.54	83.1
MÄRKE	PROFIL	MATERIAL	ANTAL	LÄNGD	AREA	VIKT
MATERIALLISTA				TOTALT	2.54	83.1

Norconsult ANSVARIG PART BJÖRN LIDSTRÖM BJÖRN LIDSTRÖM ARVID WENNERBERG	PROJEKT CENTRALEKÖK ROBERTSFORS KOMMUN RITNINGSKATEGORI TILLVERKNINGSRITNINGAR STÅL INNEHÅLL PARTS	FÖRFRÅGNINGSUNDERLAG		STATUS	
		BYGGHANDLING		HANDLING	
		ÄNDRING	FORMAT	A3	SKALA
		2024-12-20	DATUM	1:5	BET