


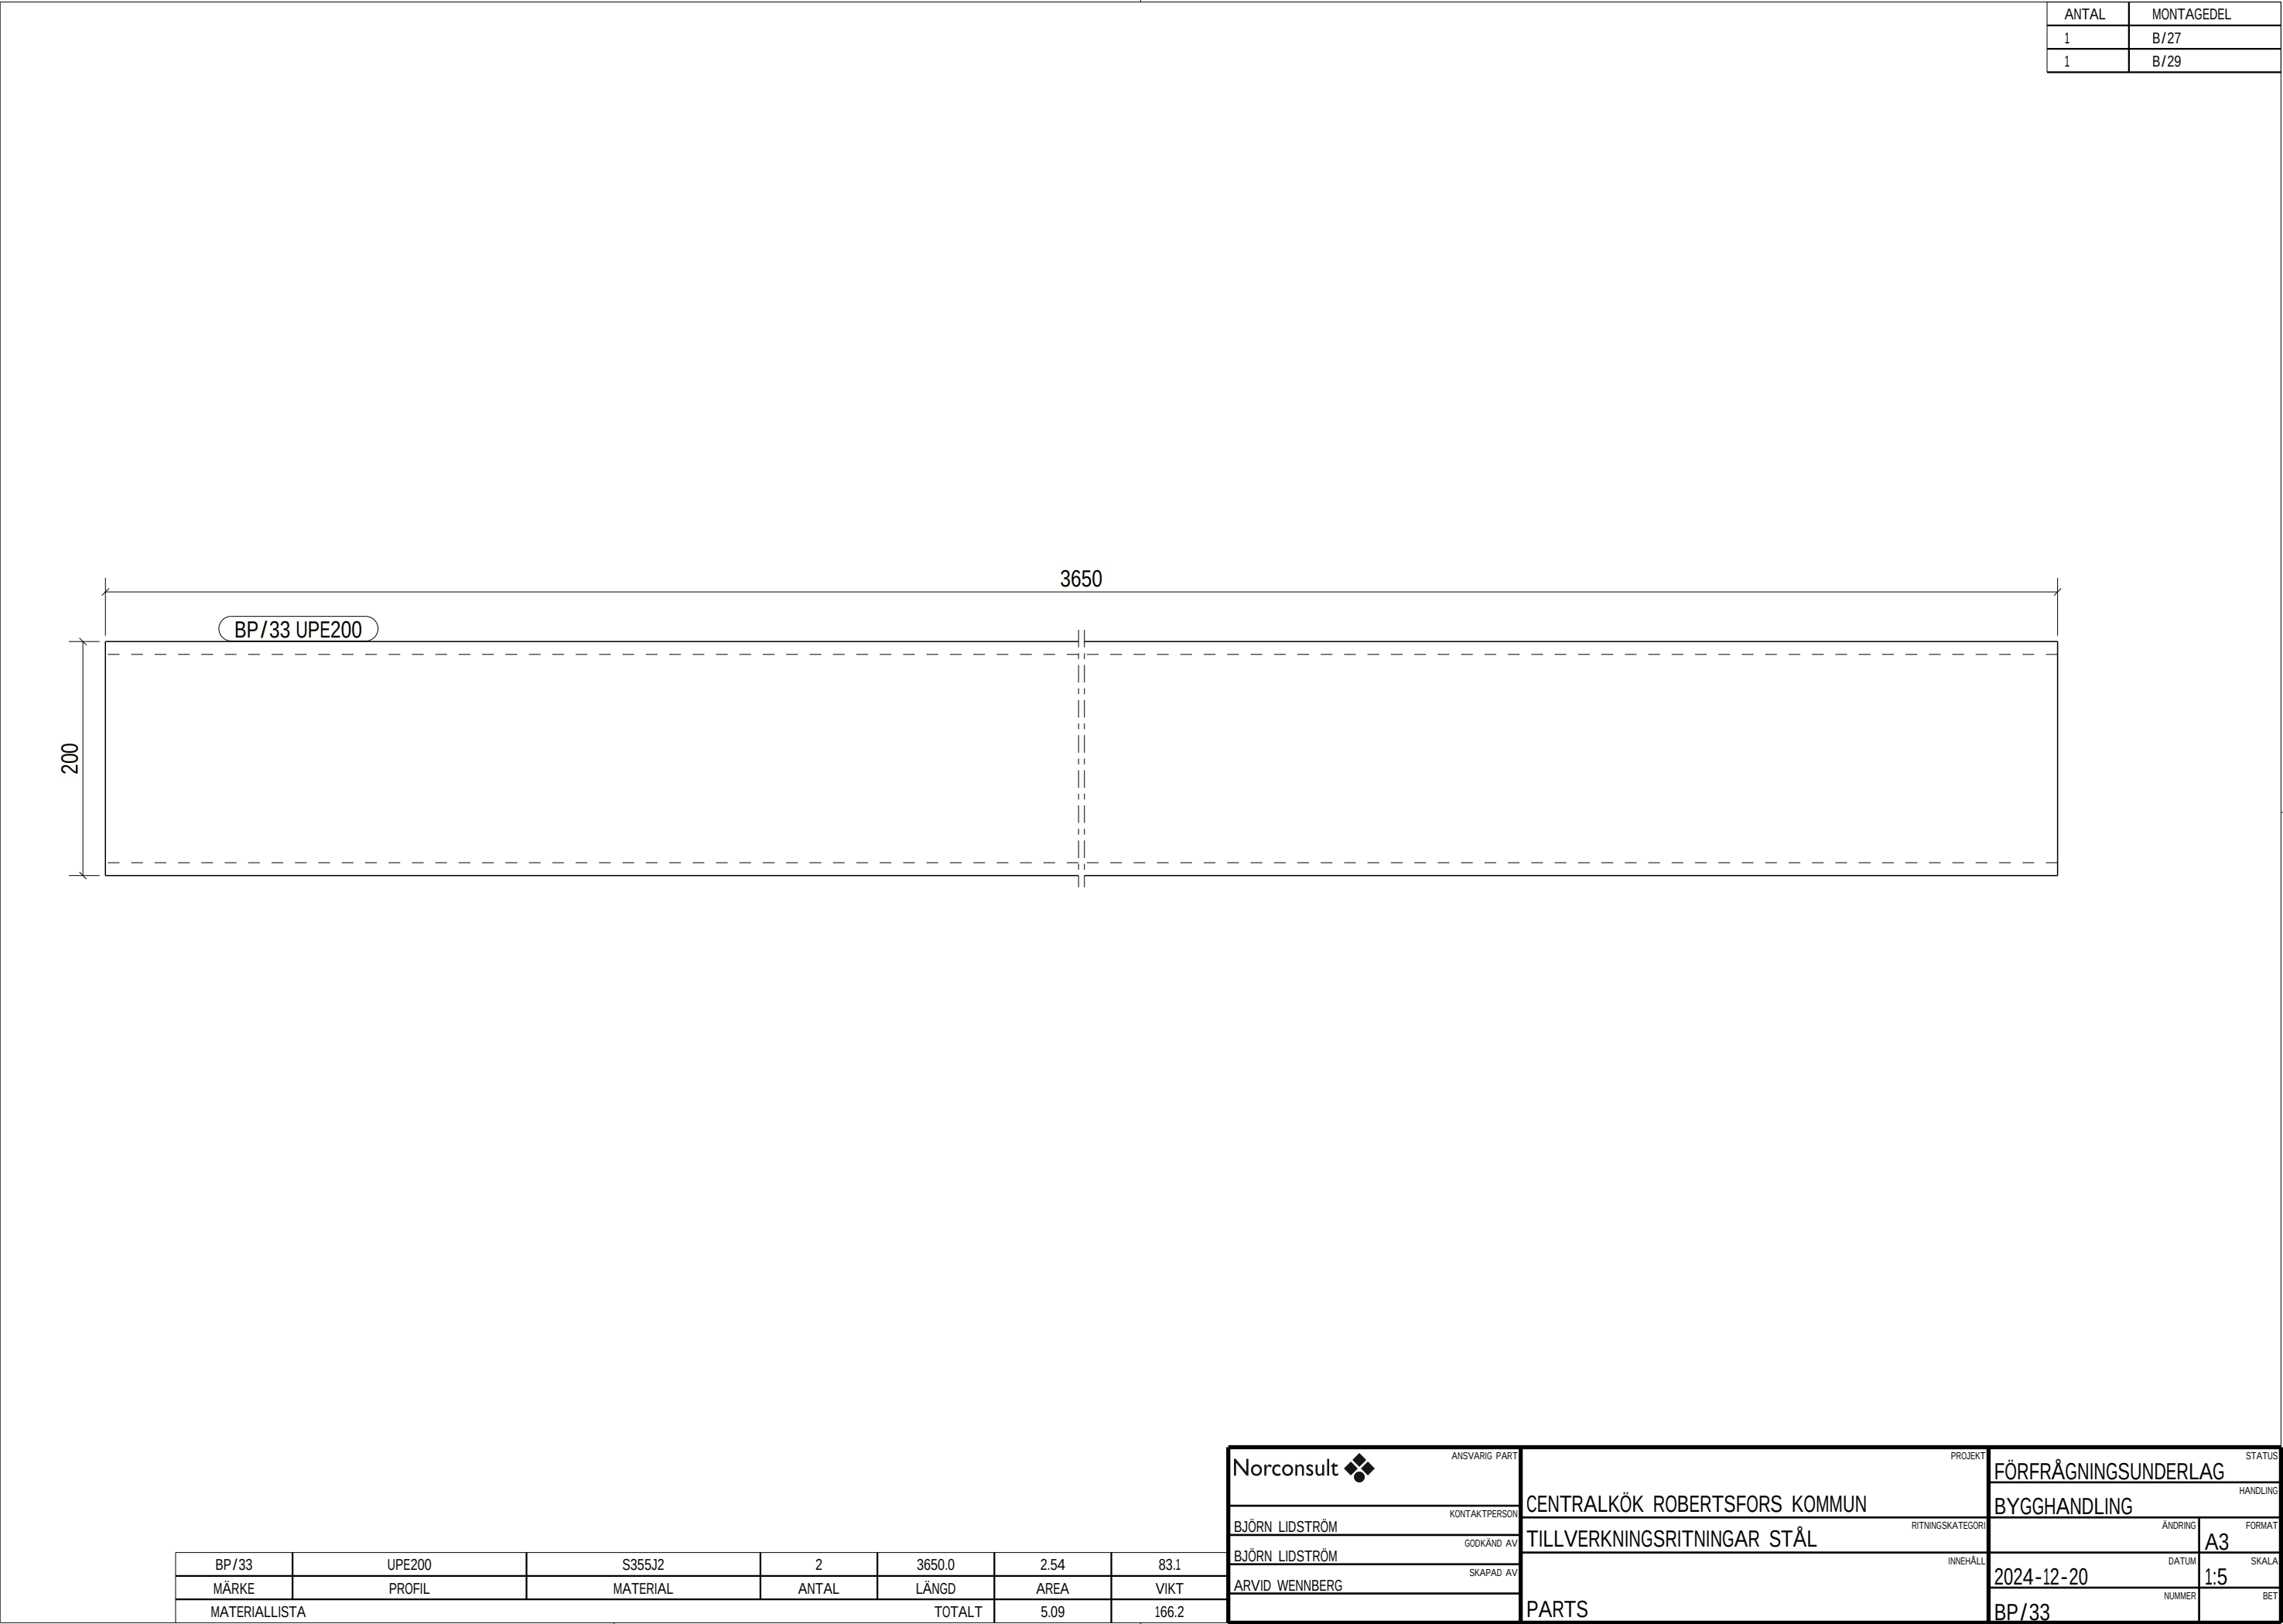

BP/33	UPE200	S355J2	2	3650.0	2.54	83.1
MÄRKE	PROFIL	MATERIAL	ANTAL	LÄNGD	AREA	VIKT
MATERIALLISTA				TOTALT	5.09	166.2

Norconsult		CENTRALEKÖK ROBERTSFORS KOMMUN		FÖRFRÅGNINGSUNDERLAG	
BJÖRN LIDSTRÖM		TILLVERKNINGSRITNINGAR STÅL		BYGGHANDLING	
ARVID WENNERBERG		PARTS		2024-12-20	A3
				1:5	SKALA
				BP/33	BET