


ANTAL	MONTAGEDEL
1	B/5

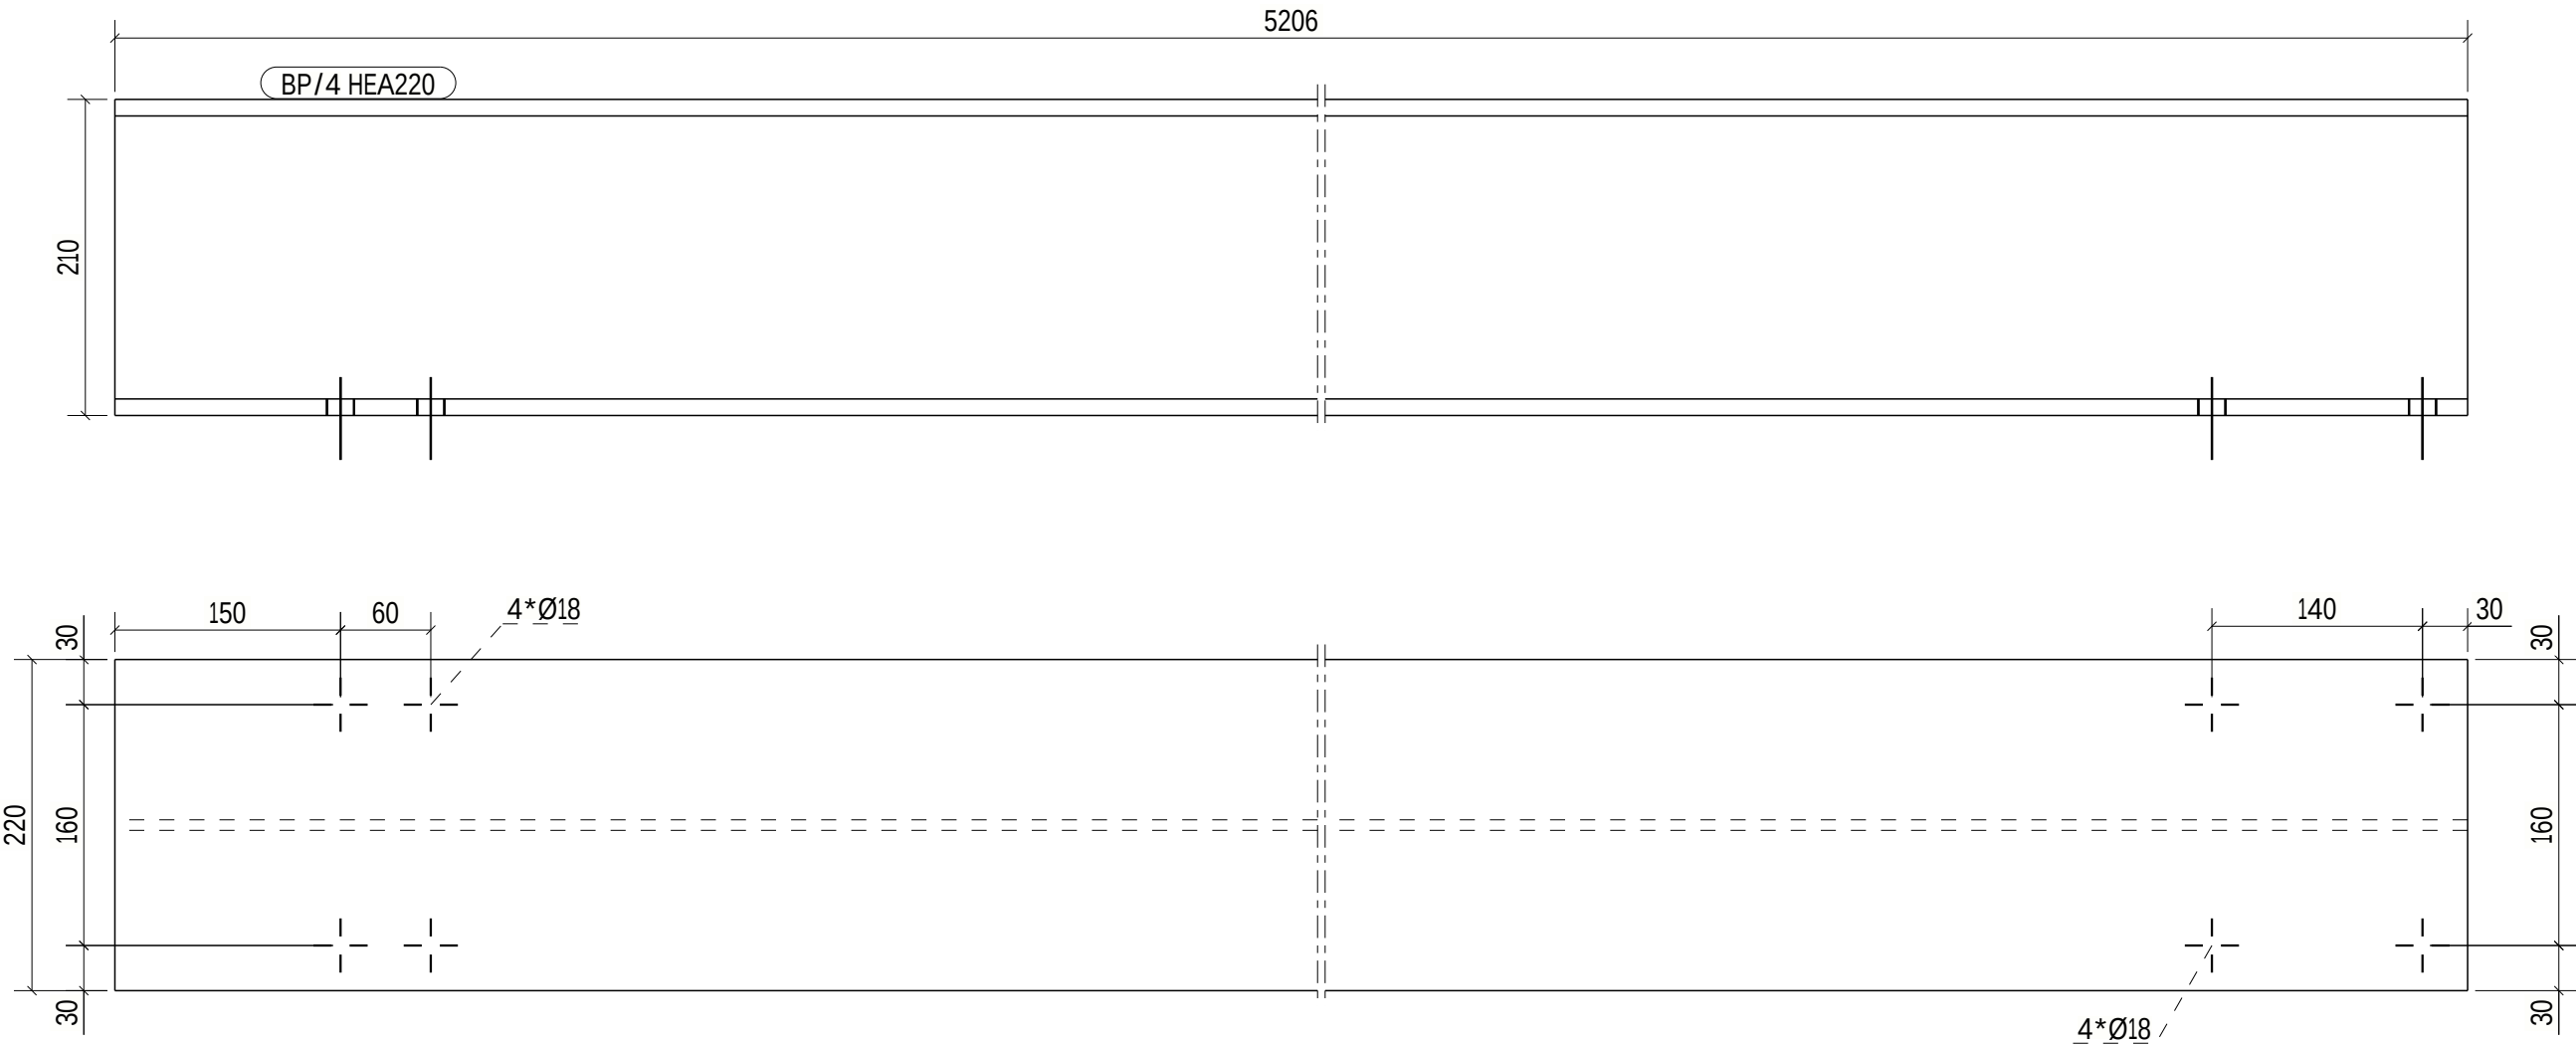

BP/4	HEA220	S355J2	1	5206.0	6.53	262.9
MÄRKE	PROFIL	MATERIAL	ANTAL	LÄNGD	AREA	VIKT
MATERIALLISTA				TOTALT	6.53	262.9

Norconsult		ANSVARIG PART	PROJEKT		STATUS	
BJÖRN LIDSTRÖM BJÖRN LIDSTRÖM ARVID WENNERBERG			CENTRALKÖK ROBERTSFORS KOMMUN		FÖRFRÅGNINGSUNDERLAG	
			TILLVERKNINGSRITNINGAR STÅL		BYGGHANDLING	
			PARTS		BP/4	
			TILLVERKNINGSRITNINGAR STÅL		BYGGHANDLING	
KONTAKTPERSON			RITNINGSKATEGORI		ANDRING	
GODKÄND AV			INNEHÅLL		FORMAT	
SKAPAD AV					A3	
					SKALA	
			2024-12-20		1:5	
					BET	
			NUMMER			