


ANTAL	MONTAGEDEL
1	B/7

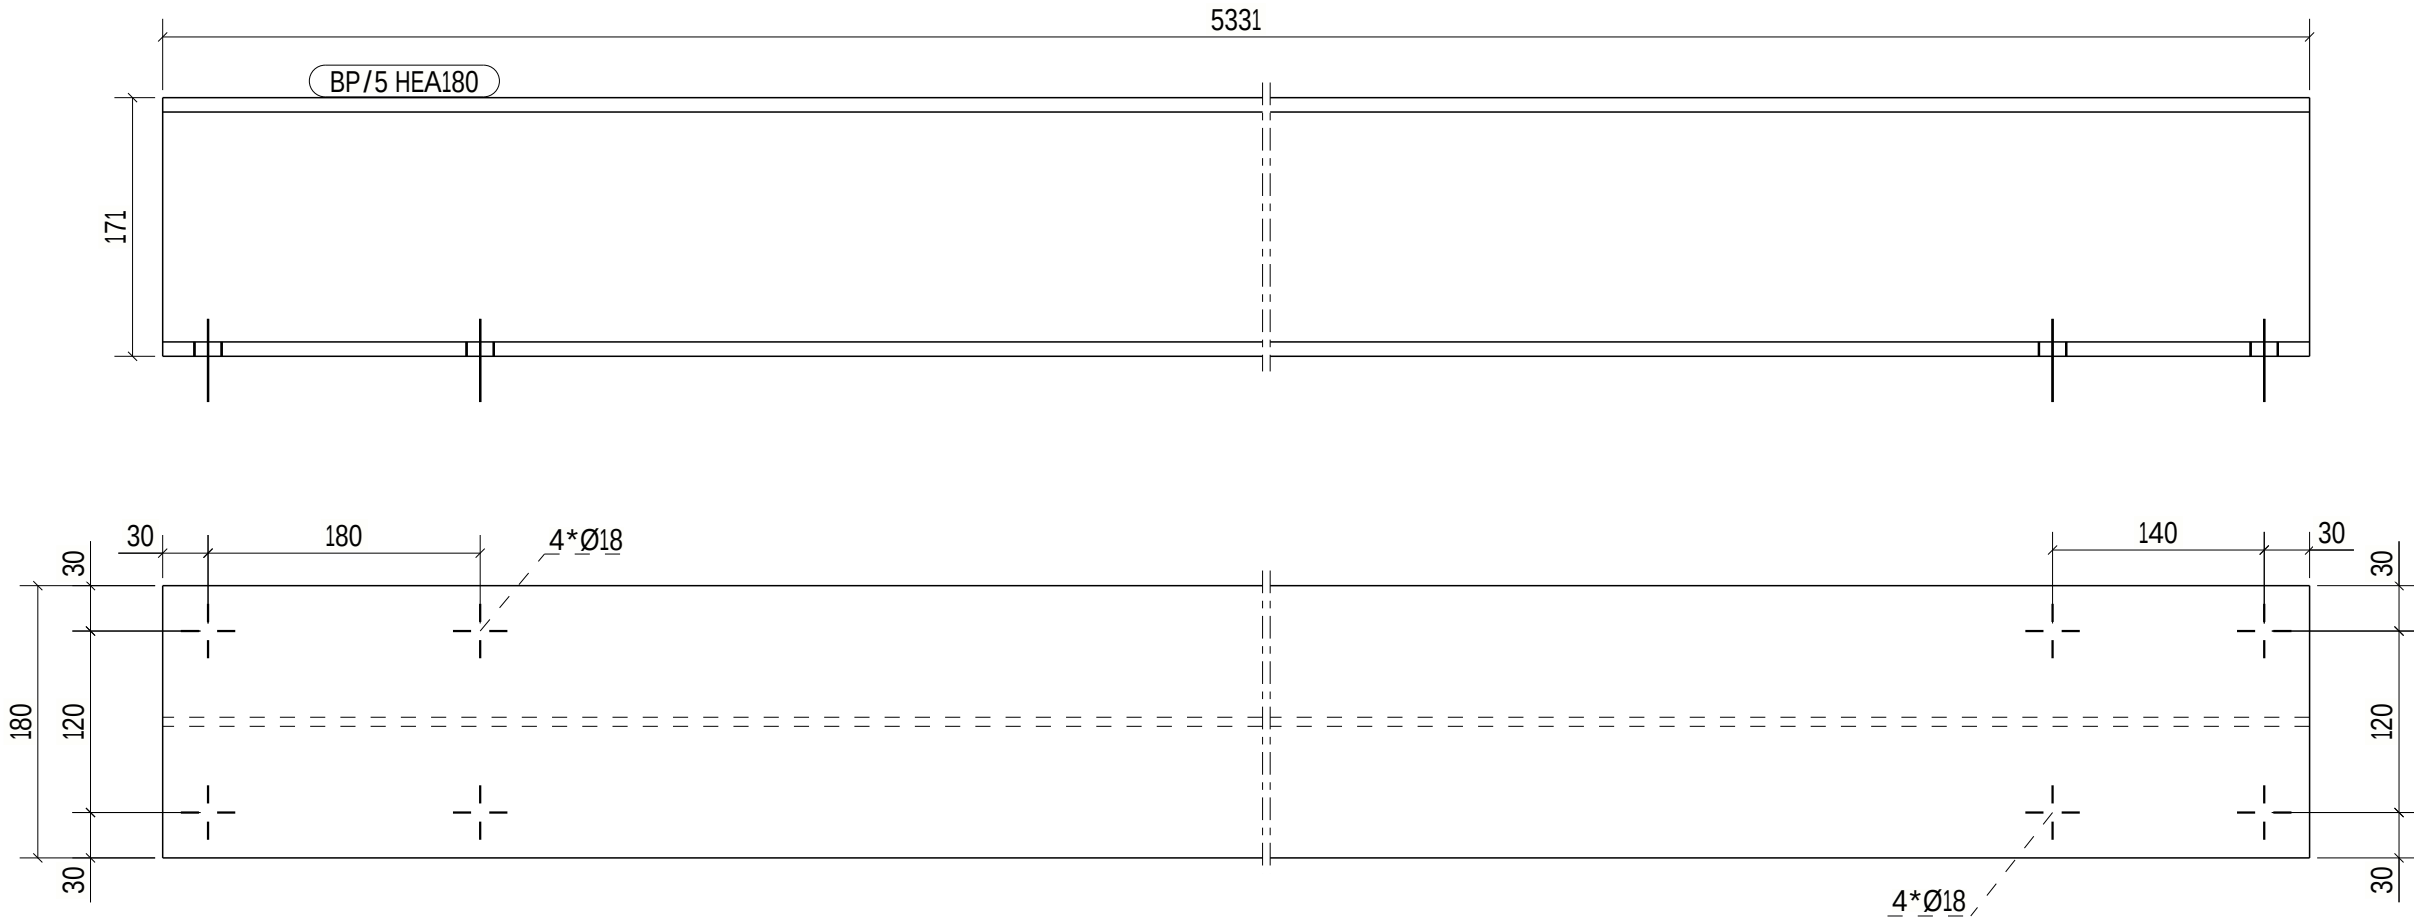

BP/5	HEA180	S355J2	1	5331.0	5.46	189.4
MÄRKE	PROFIL	MATERIAL	ANTAL	LÄNGD	AREA	VIKT
MATERIALLISTA				TOTALT	5.46	189.4

Norconsult	ANSVARIG PART	CENTRALKÖK ROBERTSFORS KOMMUN	PROJEKT	FÖRFRÅGNINGSUNDERLAG		STATUS			
	KONTAKTPERSON		TILLVERKNINGSRITNINGAR STÅL	RITNINGSKATEGORI	BYGGHANDLING		HANDLING		
	BJÖRN LIDSTRÖM				ÄNDRING	FORMAT	A3		
	BJÖRN LIDSTRÖM							DATUM	SKALA
	ARVID WENNERBERG								
	SKAPAD AV	PARTS	INNEHÅLL	NUMMER	BET	BP/5			