


ANTAL	MONTAGEDEL
1	B/2

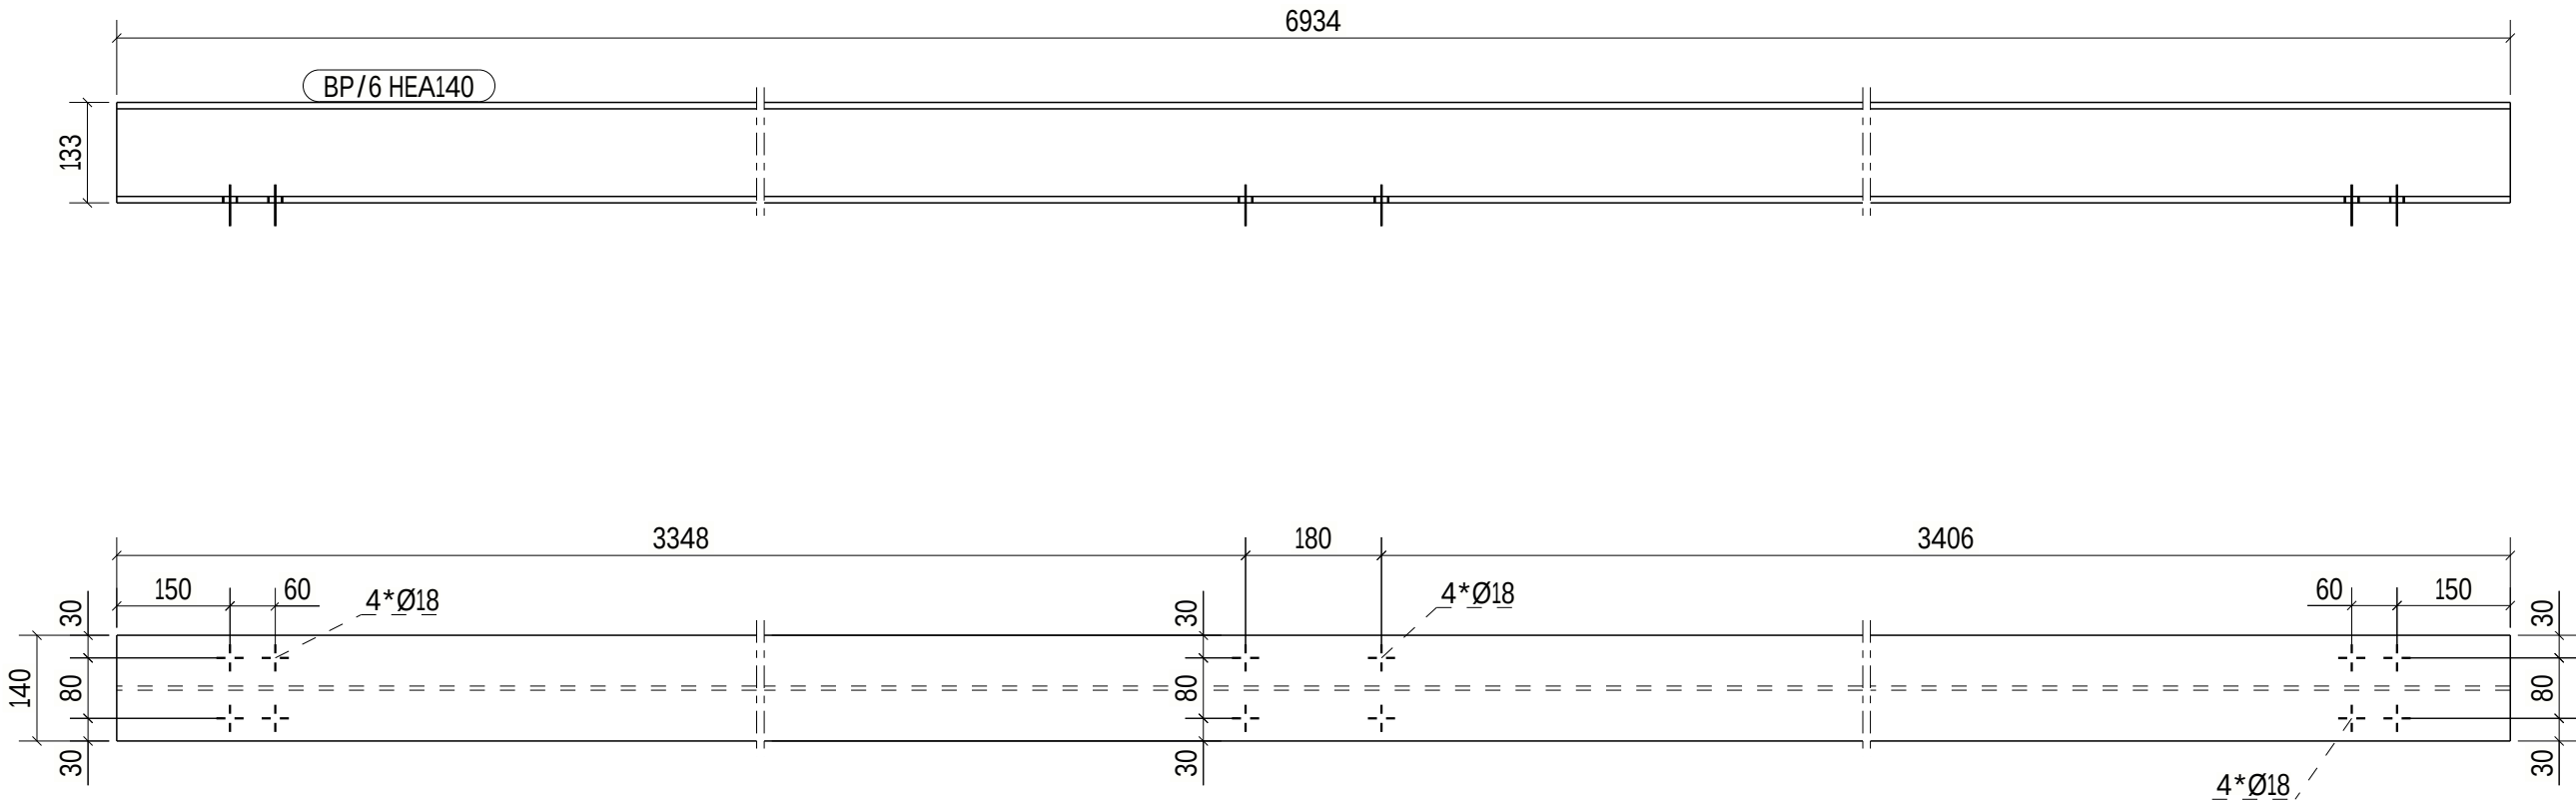

BP/6	HEA140	S355J2	1	6934.0	5.51	171.0
MÄRKE	PROFIL	MATERIAL	ANTAL	LÄNGD	AREA	VIKT
MATERIALLISTA				TOTALT	5.51	171.0

Norconsult	ANSVARIG PART	PROJEKT	FÖRFRÅGNINGSUNDERLAG		STATUS
	KONTAKTPERSON	CENTRALEKÖK ROBERTSFORS KOMMUN	BYGGHANDLING		HANDLING
	GODKÄND AV	TILLVERKNINGSRITNINGAR STÅL	ÄNDRING		FORMAT
BJÖRN LIDSTRÖM		SKAPAD AV	INNEHÅLL		DATUM
ARVID WENNERBERG		PARTS	2024-12-20		1:10
			NUMMER		BET
			BP/6		