


ANTAL	MONTAGEDEL
1	B/19

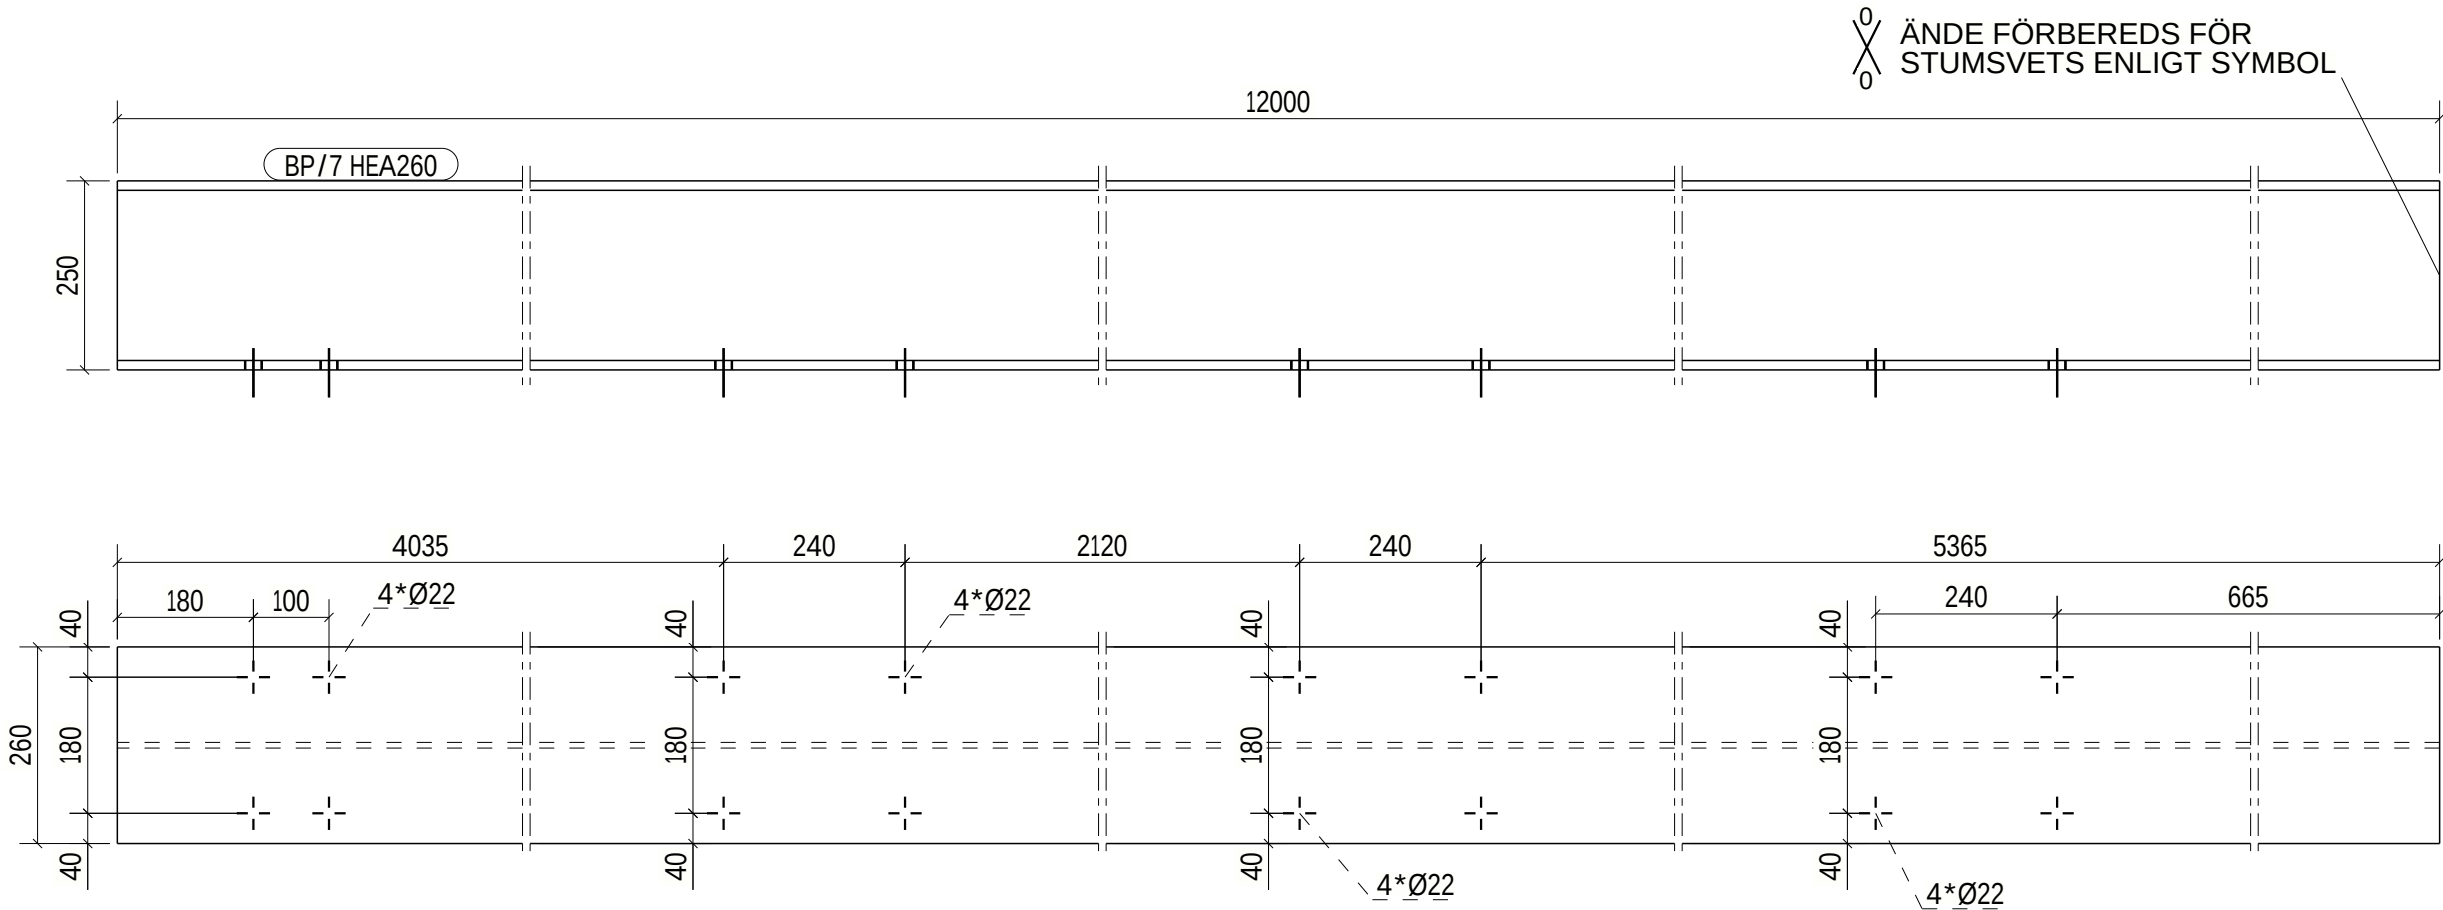

BP/7	HEA260	S355J2	1	12000.0	17.81	817.8
MÄRKE	PROFIL	MATERIAL	ANTAL	LÄNGD	AREA	VIKT
MATERIALLISTA				TOTALT	17.81	817.8

Norconsult		CENTRALE KÖK ROBERTSFORS KOMMUN		FÖRFRÅGNINGSUNDERLAG	
BJÖRN LIDSTRÖM		TILLVERKNINGSRITNINGAR STÅL		BYGGHANDLING	
ARVID WENNERBERG		PARTS		2024-12-20	
				A3	
				1:10	
				BP/7	